


Revision Schedule			
Rev	Date	Description	Drn By
C1	27.11.25	Construction Issue	-

Part O requirements:-
Safety Rail to be installed at 1100mm, which may be omitted if
Build Tolerance to window opening is within a range of maximum
1100mm and minimum 1000mm

500mm loft quilt required for 2021 regulations (100 between trusses / 200 / 200).

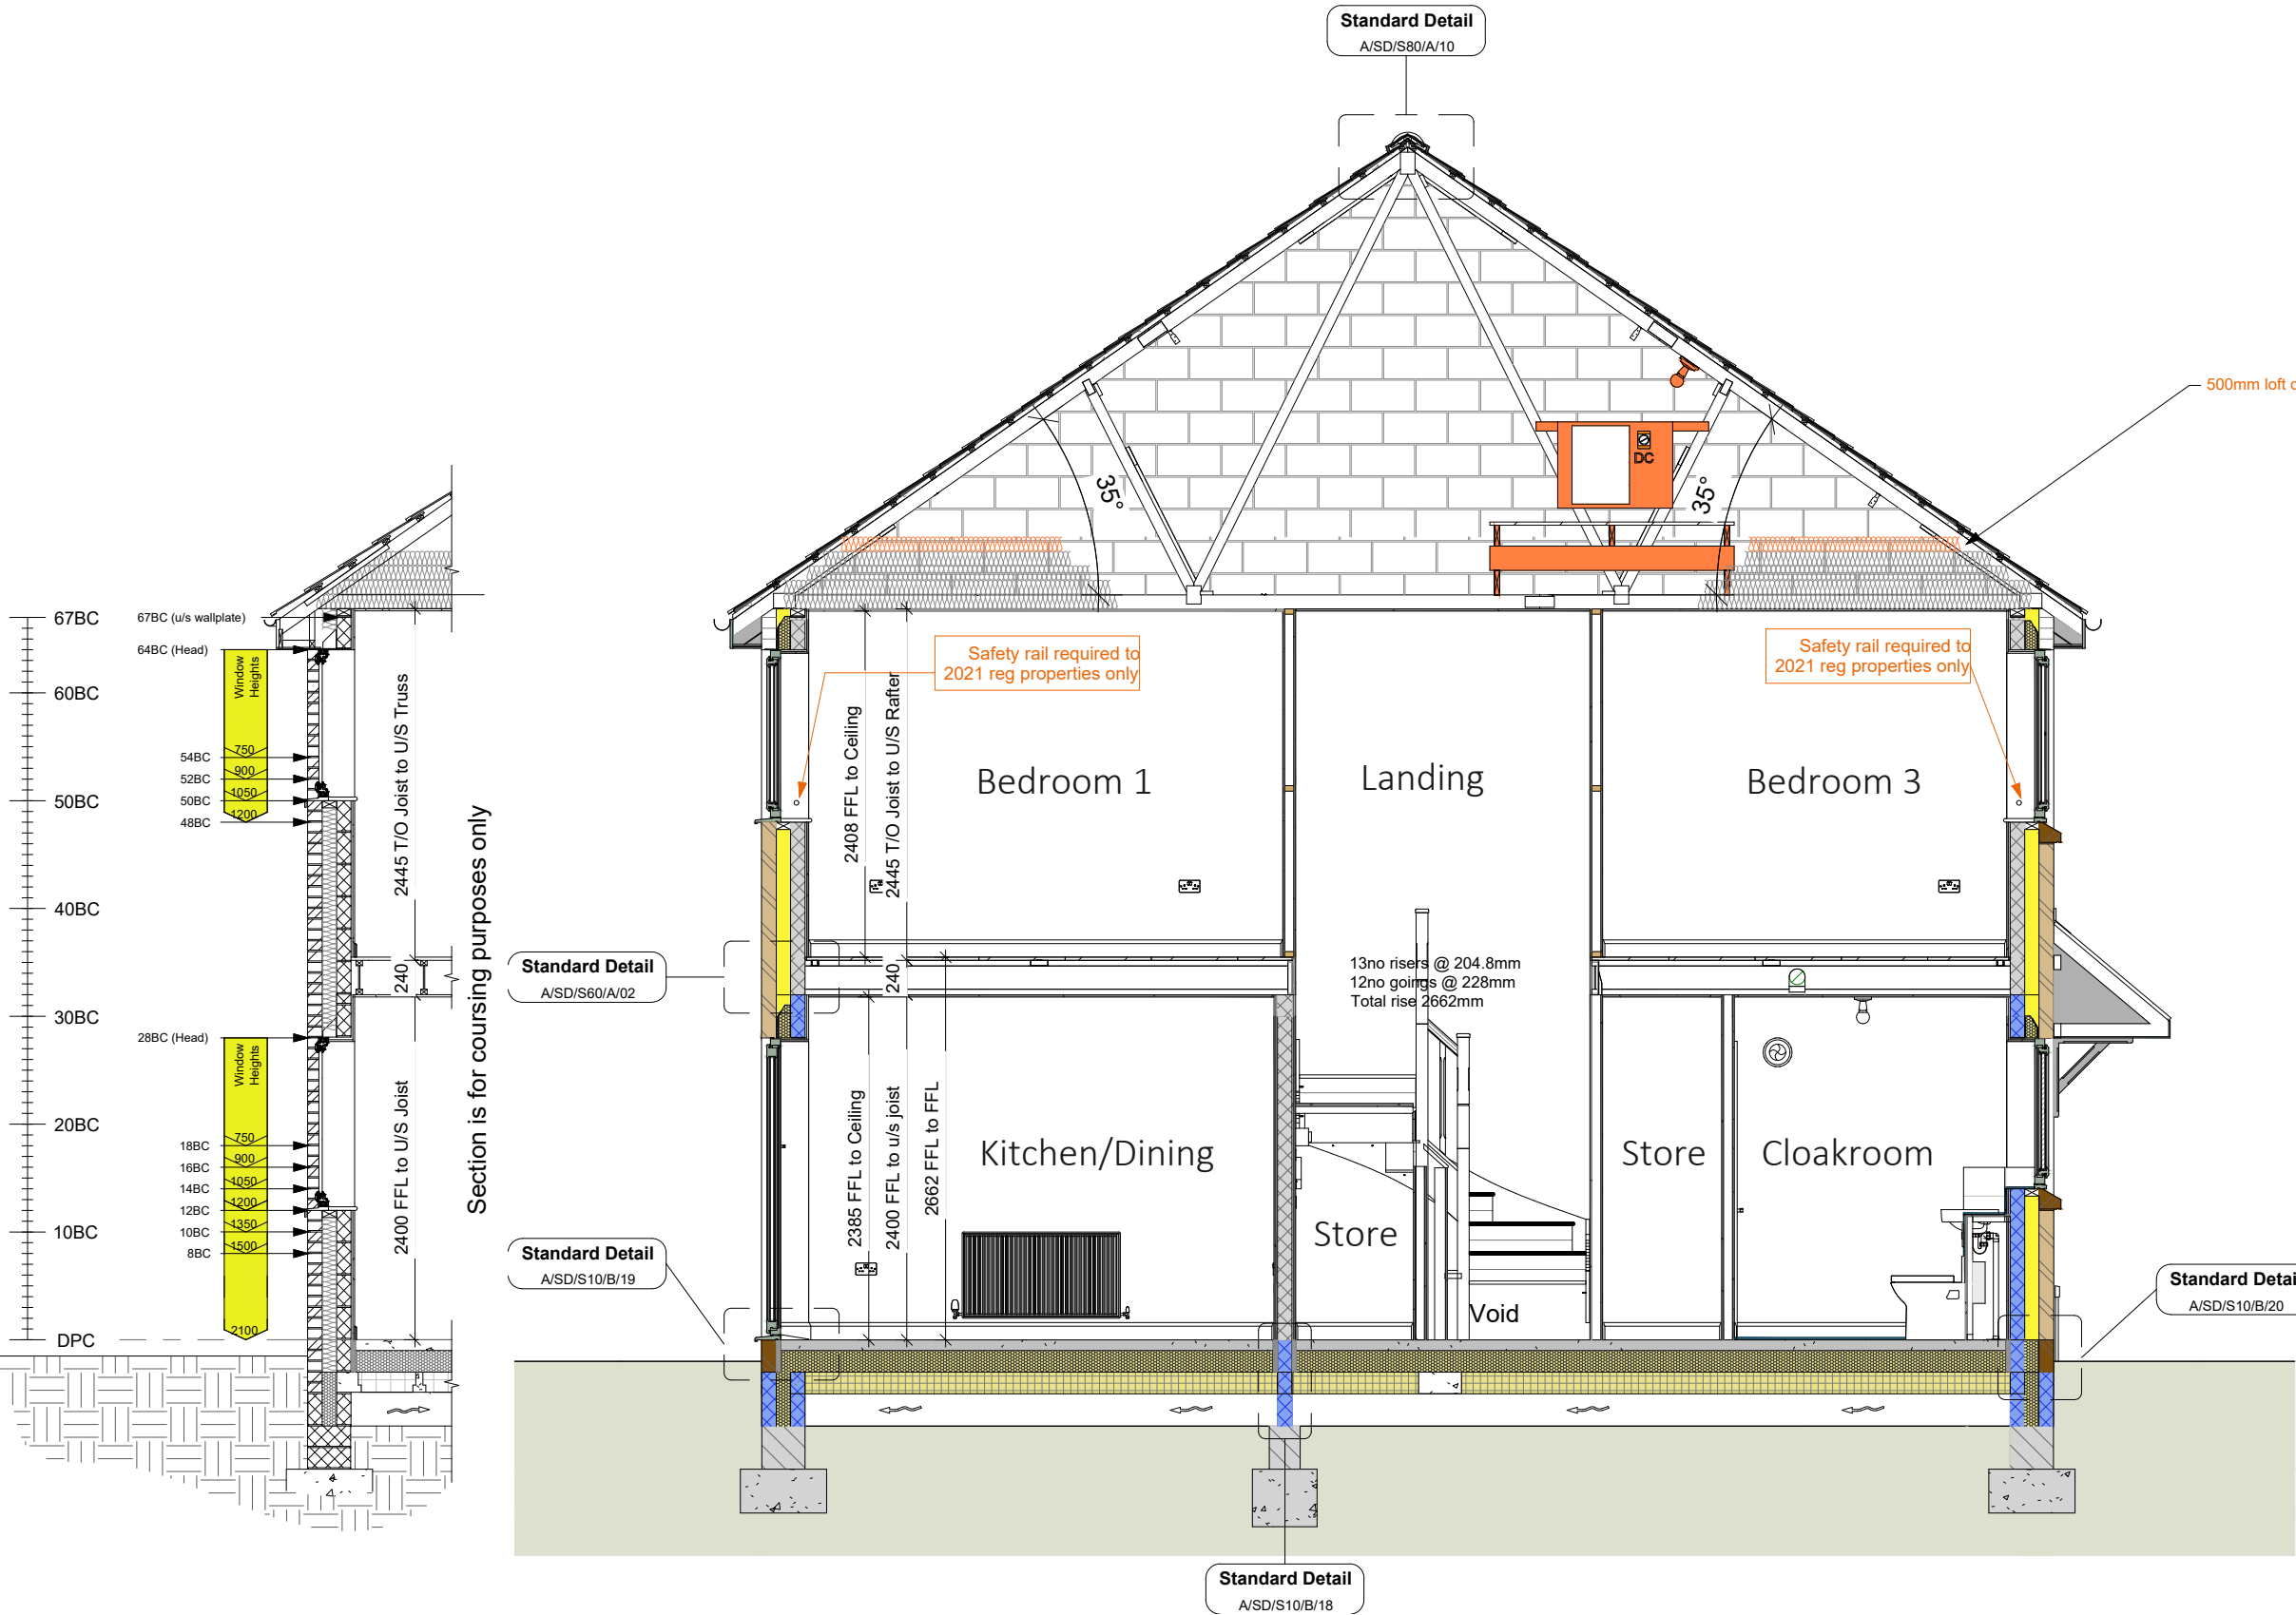

B Section B - B
1 : 50

CONSTRUCTION **Bellway**
www.bellway.co.uk

Bellway Homes (Eastern Counties)
Building 2030, Cambourne Business Park,
Cambridgeshire CB23 6DW
Tel: 01480 425 200

Project
Somersham
St Ives Road
Working Drawings

Drawing Title
The Coppersmith-Life CSL-3B-2S-AT
1026 ft² | 3b Det / Semi | All Traditional Variants
Section B-B

Drawing Created By Group	First Issue Date April '25	Scale(s) 1 : 50
Project No BI01	Drng Status Construction	Revision C1
Drawing No. BI01/1026CSL/20/AT/02		

Plots 08, 14, 50 (AS) & 01, 03, 09, 18, 19, 49 OPP

Do not scale - if in doubt, ask