


Revision Schedule			
Rev	Date	Description	Drn By
C1	08.12.25	Construction Issue	-

2021 Regulations
All fixed panes* in habitable rooms to become openable to satisfy Approved Document O requirements, as indicated by orange dashed lines (*excludes fixed panes to French Door sidelights, and entrance door sidelights).

Part O requirements:-
Safety Rail to be installed at 1100mm, which may be omitted if Build Tolerance to window opening is within a range of maximum 1100mm and minimum 1000mm

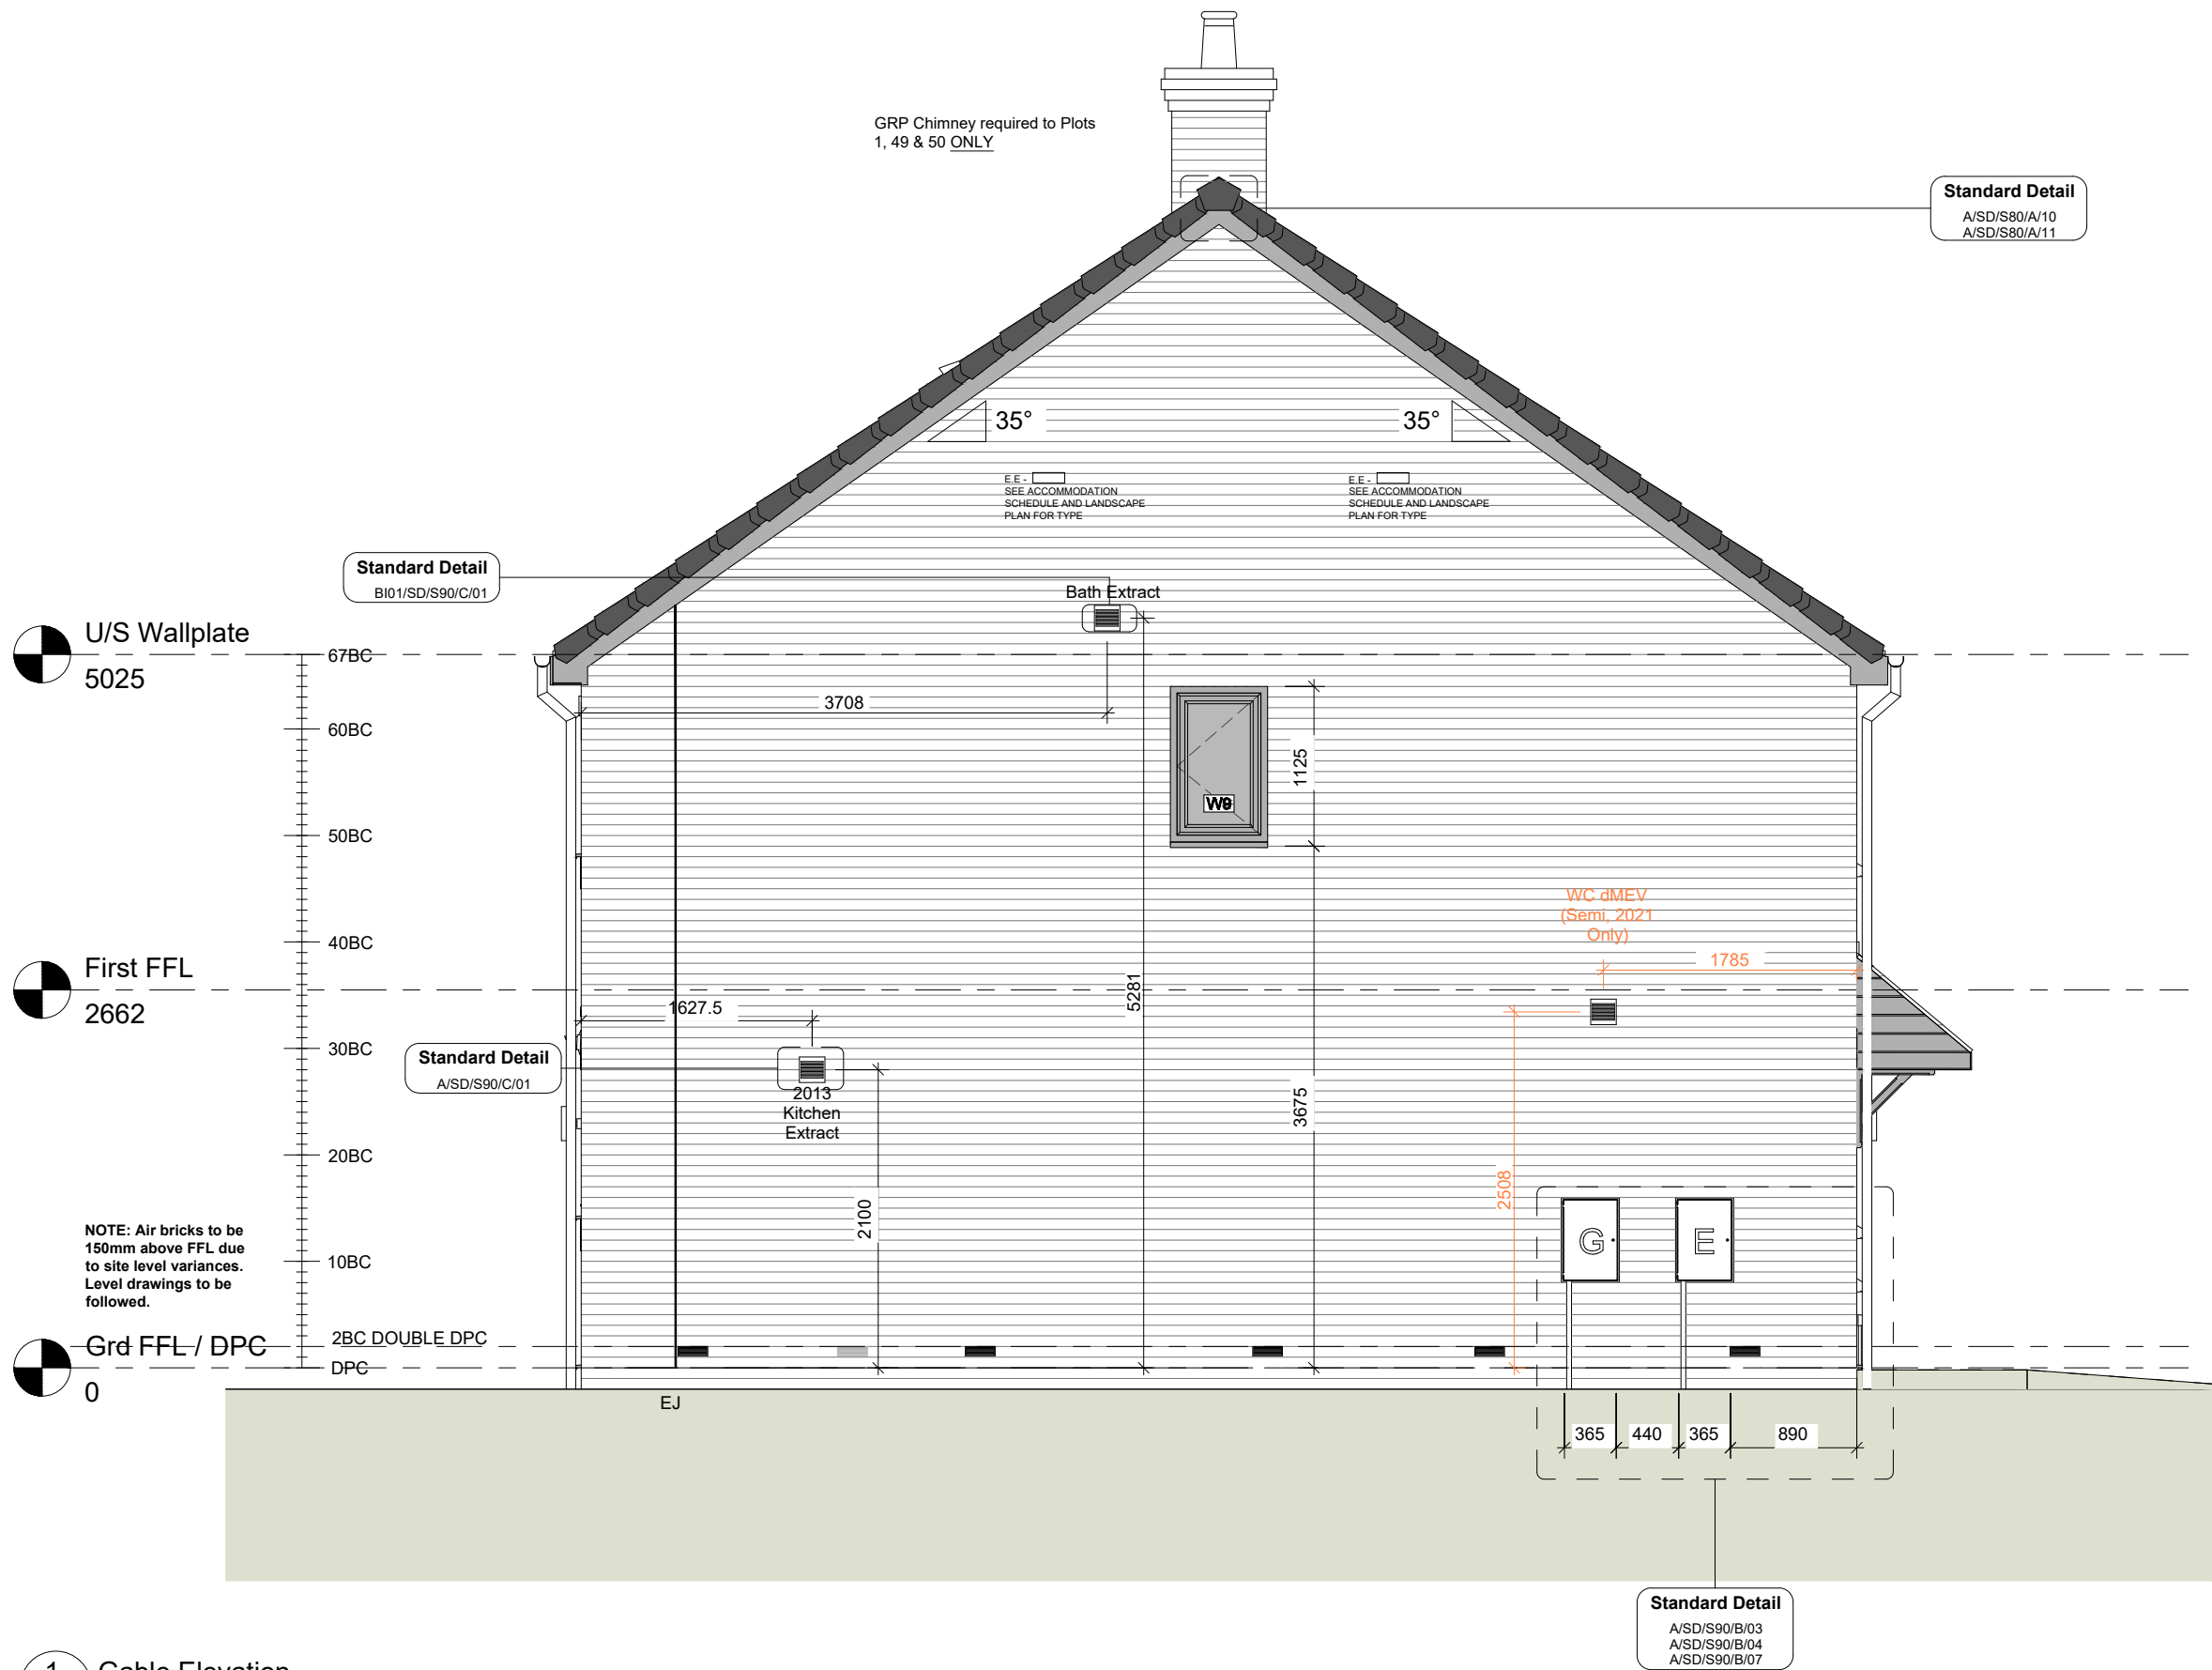

CONSTRUCTION **Bellway**
www.bellway.co.uk

Bellway Homes (Eastern Counties)
Building 2030, Cambourne Business Park,
Cambridgeshire CB23 6DW
Tel: 01480 425 200

Project
Somersham
St Ives Road
Working Drawings

Drawing Title
The Coppersmith-Life **CSL-3B-2S-CB**
1026 ft² | 3b Det / Semi | Country Brick
Gable Elevation

Drawing Created By Group	First Issue Date April '25	Scale(s) 1 : 50
Project No BI01	Drg Status Construction	Revision C1
Drawing No. BI01/1026CSL/25/CB/03		

Plots 08, 14, 50 (AS) & 01, 03, 09, 18, 19, 49 OPP

Do not scale - if in doubt, ask