



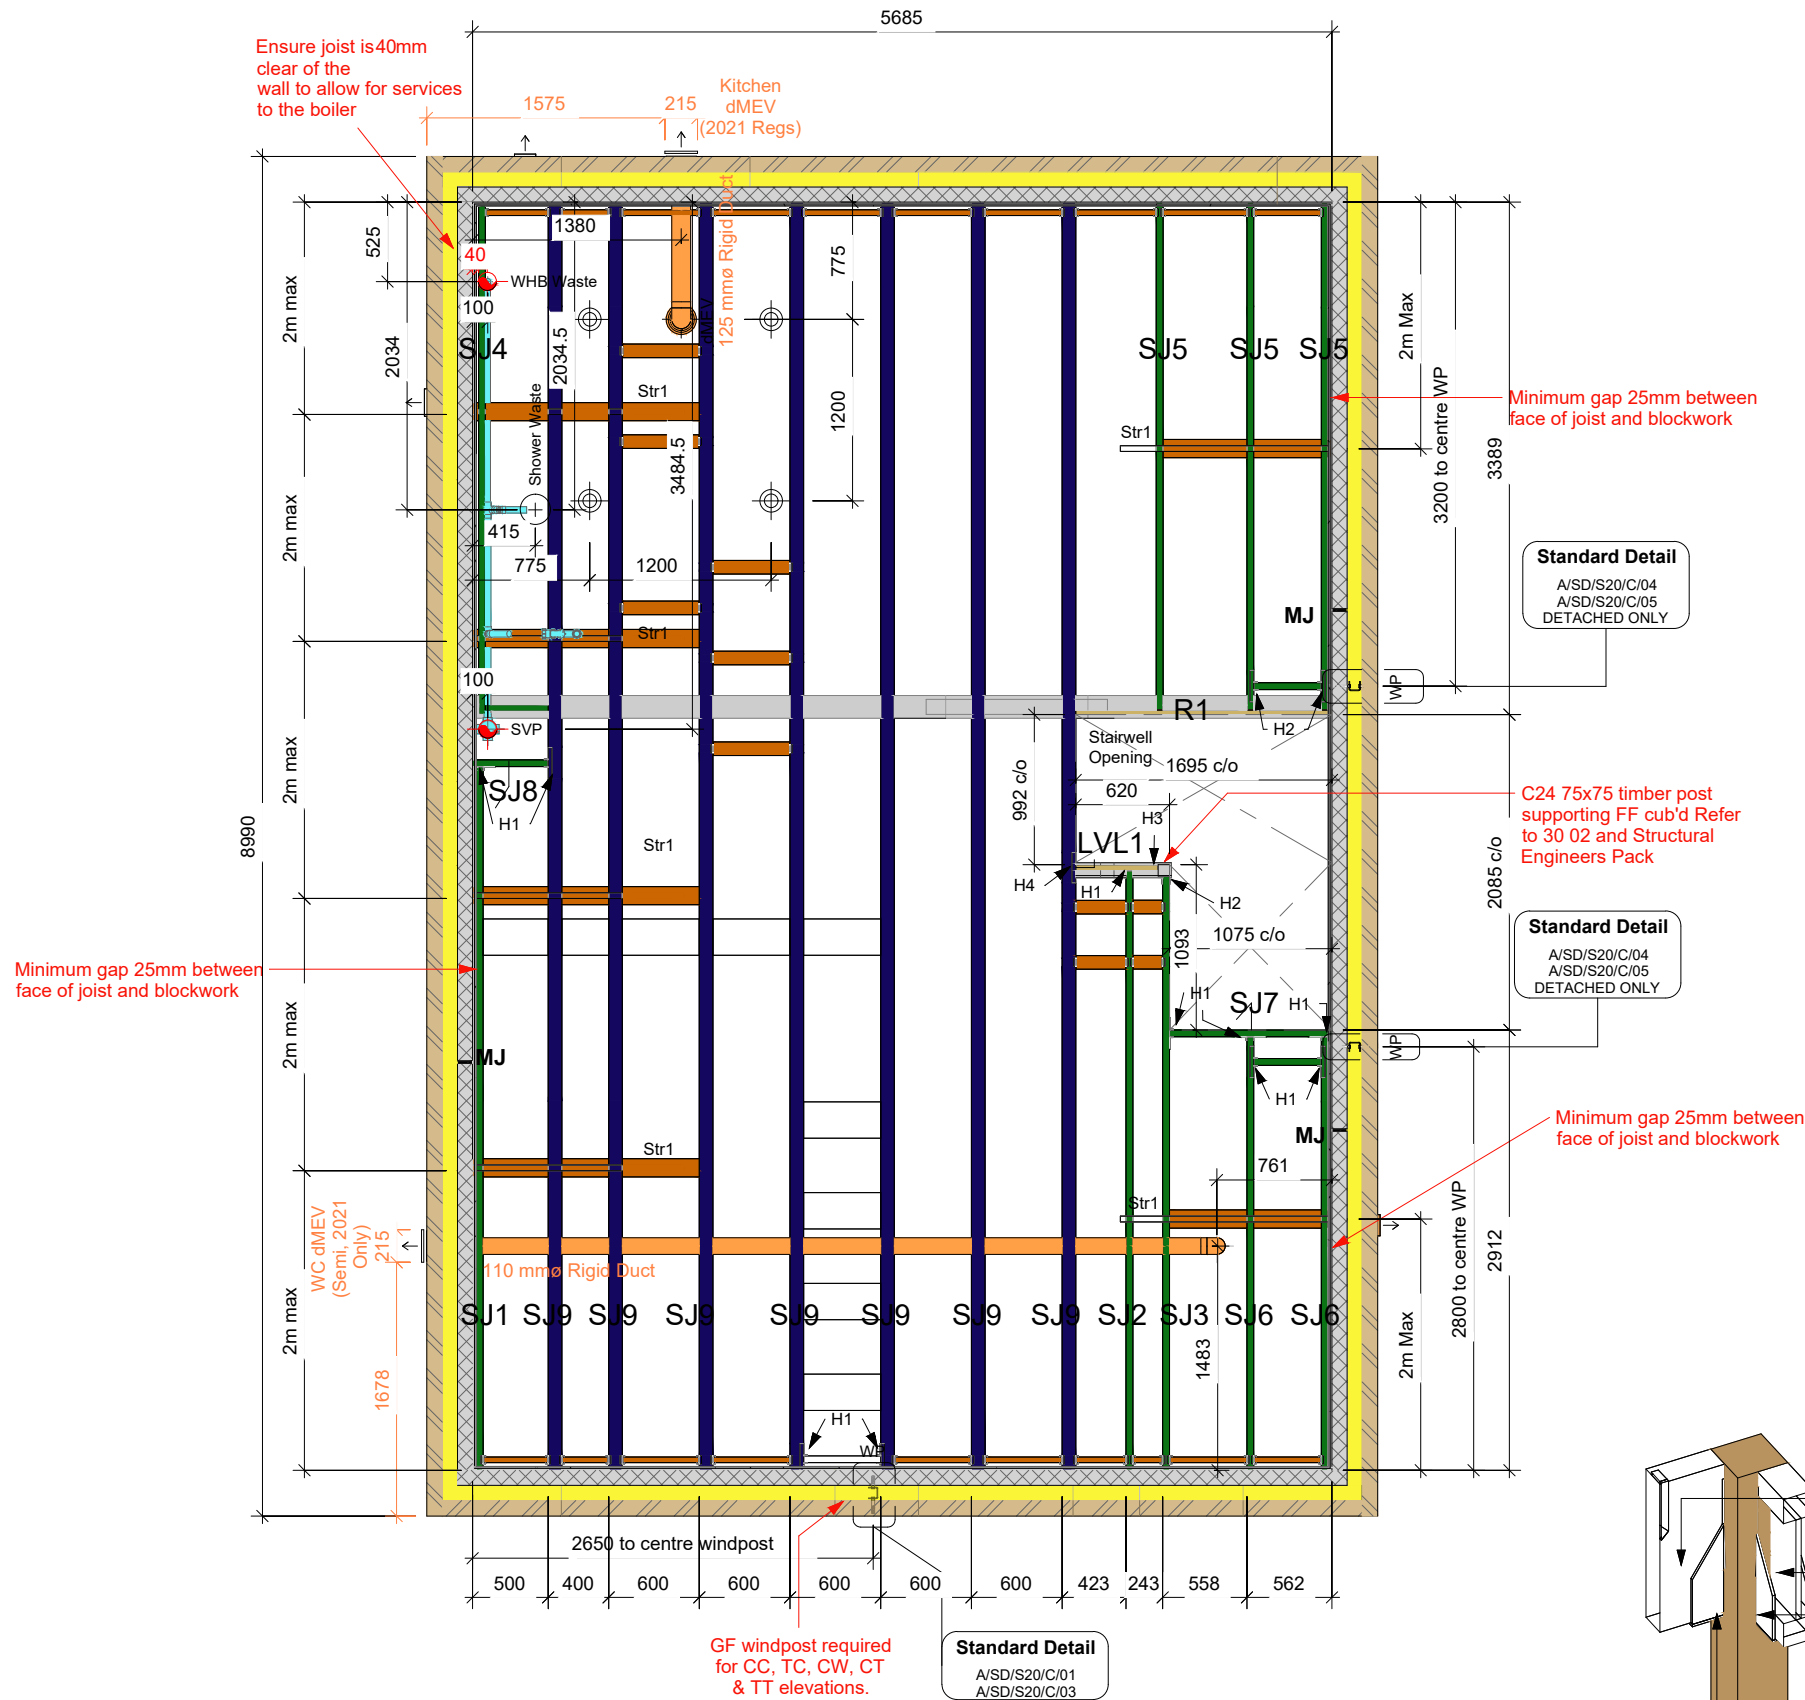

1 First Floor Joists
1 : 50

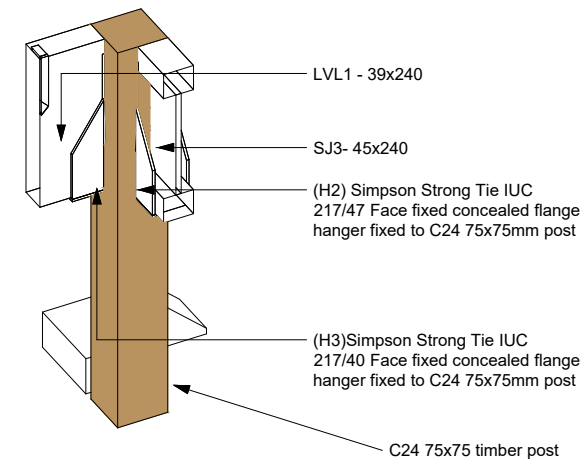

2 Post Head Connection

Plots 08, 14, 50 (AS) & 01, 03, 09, 18, 19, 49 OPP

Steico First Floor Joists & Blocking

Qty	Ref	Length	Description
Beam/Joist			
1	LVL1	545mm	ST4022 STEICO LVL R - 39x240mm
1	SJ1	4752mm	ST4119 SJL 45 - 240mm
1	SJ2	4066mm	ST4119 SJL 45 - 240mm
1	SJ3	4030mm	ST4119 SJL 45 - 240mm
1	SJ4	3488mm	ST4119 SJL 45 - 240mm
3	SJ5	3459mm	ST4119 SJL 45 - 240mm
2	SJ6	2967mm	ST4119 SJL 45 - 240mm
1	SJ7	1175mm	ST4119 SJL 45 - 240mm
1	SJ8	600mm	ST4119 SJL 45 - 240mm
7	SJ9	8585mm	ST4132 SJL 90 - 240mm

Blocking			
7	BLK1	592mm	ST4022 STEICO LVL R - 39x240mm
7	BLK2	510mm	ST4022 STEICO LVL R - 39x240mm
1	BLK3	489mm	ST4022 STEICO LVL R - 39x240mm
1	BLK4	430mm	ST4022 STEICO LVL R - 39x240mm
1	BLK5	392mm	ST4022 STEICO LVL R - 39x240mm
1	BLK6	310mm	ST4022 STEICO LVL R - 39x240mm
1	BLK7	510mm	ST4029 STEICO LVL R - 45x240mm
2	BLK8	448mm	ST4119 SJL 45 - 240mm
1	BLK9	415mm	ST4119 SJL 45 - 240mm

Noggin			
20	CN1		G7002 38x38 Nogging
10	PN1		G7000 Partition Nogging (38x90)
22	SN1		G7055 38x120mm Nogging - Plank

Rimboard			
1	R1	1795mm	ST1157 STEICO LVL X - 30x240mm

Steico First Floor Accessories

Ref	Description	Qty
ZS38N Z Clip 38mm		60

End Device		
SES158/45	End Device	11
SES158/89	End Device	14

Hanger		
H1	EWB(T)235/47	12
H2	IUC217/47	1
H3	IUC217/40	1
H4	EWB(T)235/40	1

Strap		
Str1	G8304 Simpson HES15B10	6

Revision Schedule			
Rev	Date	Description	Drn By
C1	27.11.25	Construction Issue	-

Project Information		STEICO COPPERSMITH	
File Name		JUL 2024 - NHBC 2023 - EC5	
Design Date		Analytics.skd	
Software Version No.		29 Jul 2024	
Design Information		UK	
Region		EC5	
Design Code		A - Residential Upper Floor	
Application		Service Class 1	
Service Class			
Load and Deflection Settings			
Dead Load (kN/m²)		0.40 - Permanent	
Partitions Load (kN/m²)		0.35 - Permanent	
Floor Imposed UD Load (kN/m²)		1.50 - Medium Term	
Floor Imposed Concentrated Load (kN)		2.00 - Medium Term	
Instantaneous Deflection		333 - 12mm	
Net Final Deflection		250 -	
Additional Information			
Decking Type		Particle Board - 22mm P5	
Direct Applied Ceiling		Yes	
Ceiling Material		15mm - Ceiling (Gypsum board)	



CONSTRUCTION

Bellway
www.bellway.co.uk

Bellway Homes (Eastern Counties)
Building 2030, Cambourne Business Park,
Cambridgeshire CB23 6DW
Tel: 01480 425 200

Project
Somersham
St Ives Road
Working Drawings

Drawing Title
The Coppersmith-Life **CSL-3B-2S-0**

1026 ft² | 3b Det / Semi | All Variants
Joist Plan and Take Off

Drawing Created By	First Issue Date	Scale(s)
Group	April '25	1 : 50
Project No	Drg Status	Revision
BI01	Construction	C1
Drawing No.		BI01/1026CSL/40/0/02

Do not scale - if in doubt, ask