


Revision Schedule			
Rev	Date	Description	Drn By
C1	27.11.25	Construction Issue	-

Detached Roof

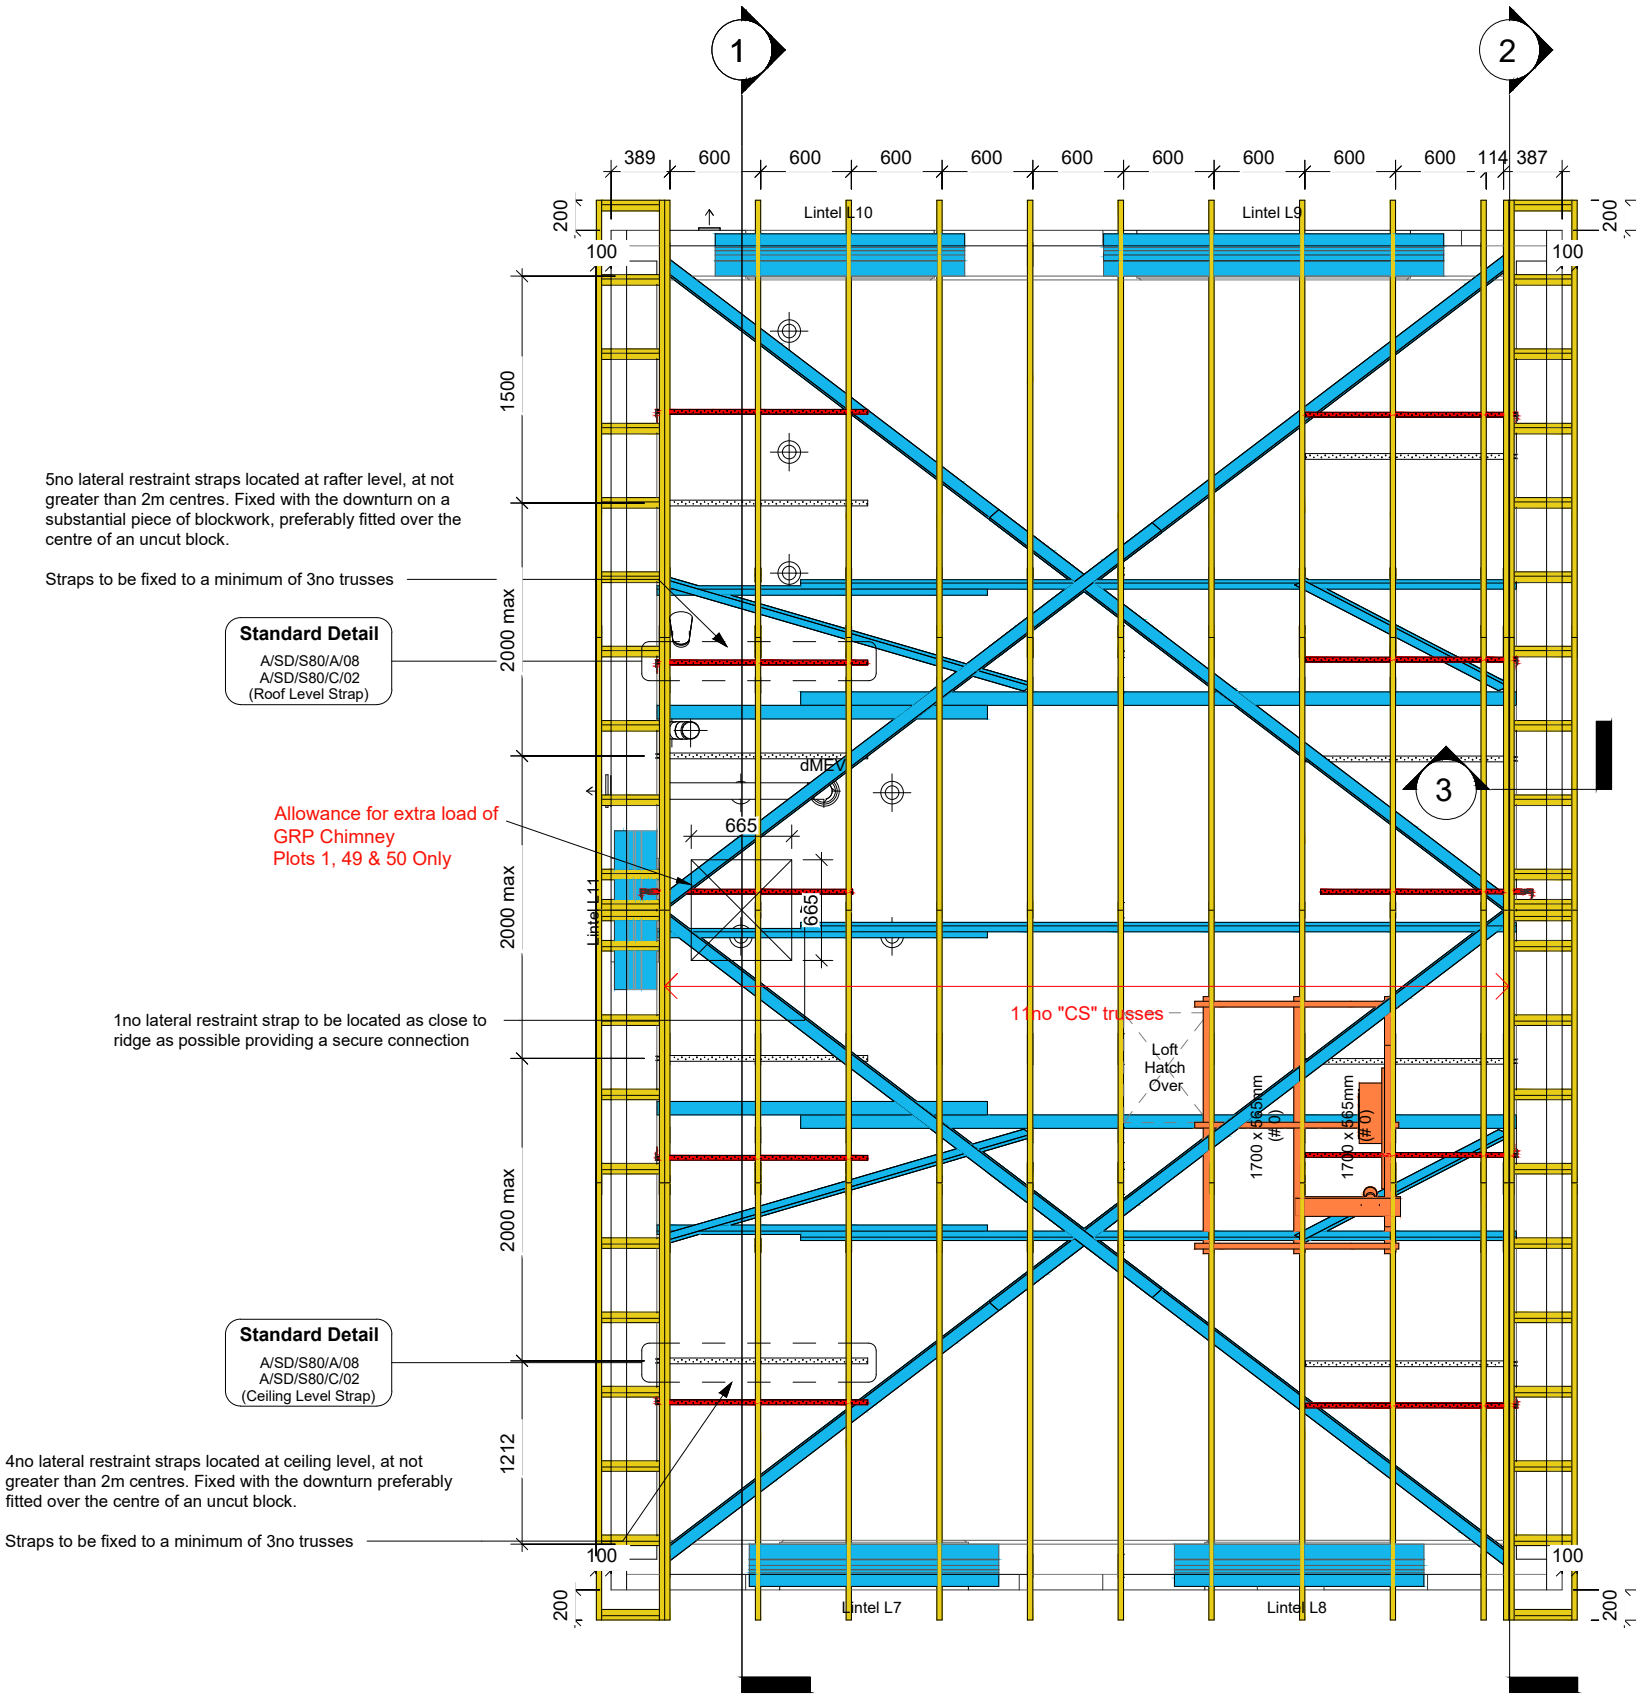

1 Detached Roof Trusses (Boxed Eaves) 1-50
1 : 50

CONSTRUCTION

Bellway
www.bellway.co.uk

Bellway Homes (Eastern Counties)
Building 2030, Cambourne Business Park,
Cambridgeshire CB23 6DW
Tel: 01480 425 200

Project
Somersham
St Ives Road
Working Drawings

Drawing Title
The Coppersmith-Life **CSL-3B-2S-0**
1026 ft² | 3b Det / Semi | All Variants
Detached Roof Layout

Drawing Created By Group	First Issue Date April '25	Scale(s) 1 : 50
Project No BI01	Drq Status Construction	Revision C1
Drawing No. BI01/1026CSL/60/0/01		

Plots 08, 14, 50 (AS) & 01, 03, 09, 18, 19, 49 OPP

Do not scale - if in doubt, ask