


Revision Schedule			
Rev	Date	Description	Drn By
C1	27.11.25	Construction Issue	-

Detached Roof

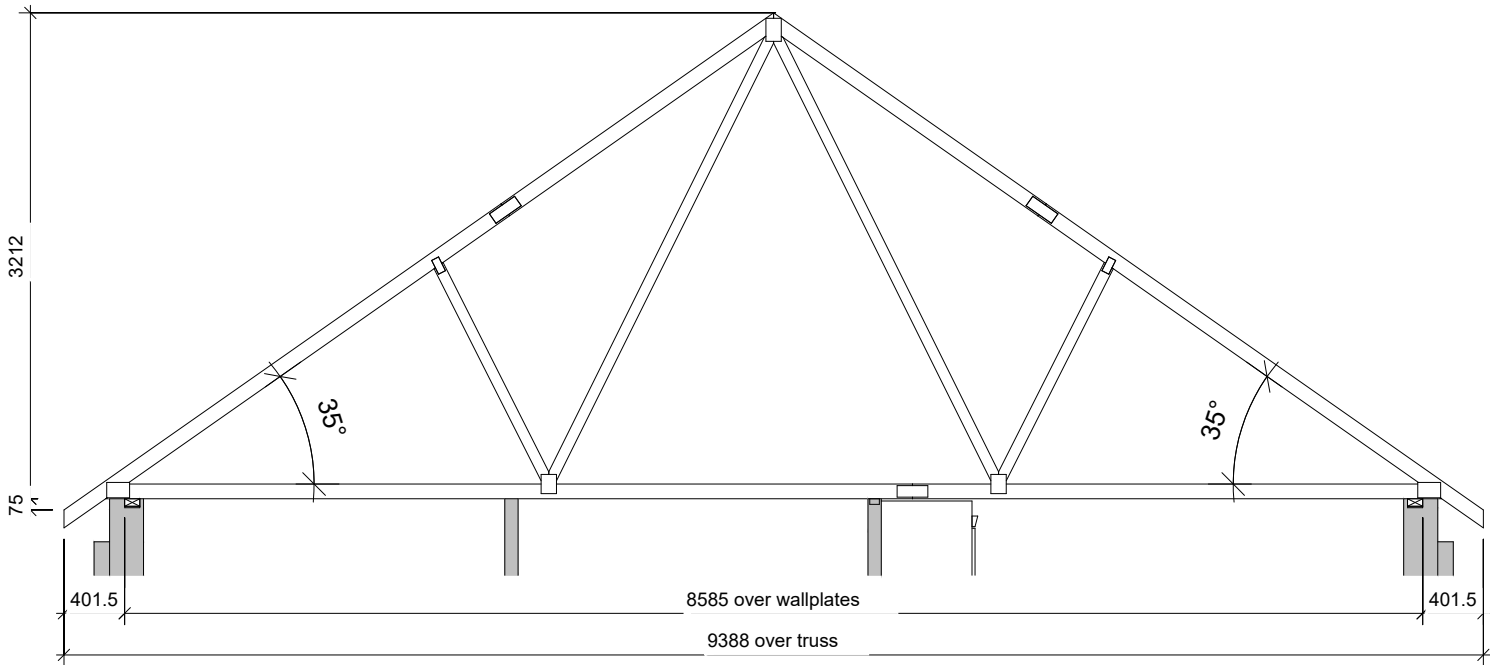

1 Truss "CS" - 11no reqd (1ply, 57kg)
1 : 50

CONSTRUCTION

Bellway

www.bellway.co.uk

Bellway Homes (Eastern Counties)
Building 2030, Cambourne Business Park,
Cambridgeshire CB23 6DW
Tel: 01480 425 200

Project
Somersham
St Ives Road
Working Drawings

Drawing Title

The Coppersmith-Life

CSL-3B-2S-0

1026 ft² | 3b Det / Semi | All Variants
Detached Roof Trusses

Drawing Created By	First Issue Date	Scale(s)
Group	April '25	1 : 50
Project No	Drg Status	Revision
BI01	Construction	C1
Drawing No.	BI01/1026CSL/60/0/02	