


Revision Schedule			
Rev	Date	Description	Drn By
C1	27.11.25	Construction Issue	-



1 Front Elevation
1 : 20

Elevations for dimensional purposes only.
Read with A/SD/S100/A/01 for canopy
fixing and construction details.

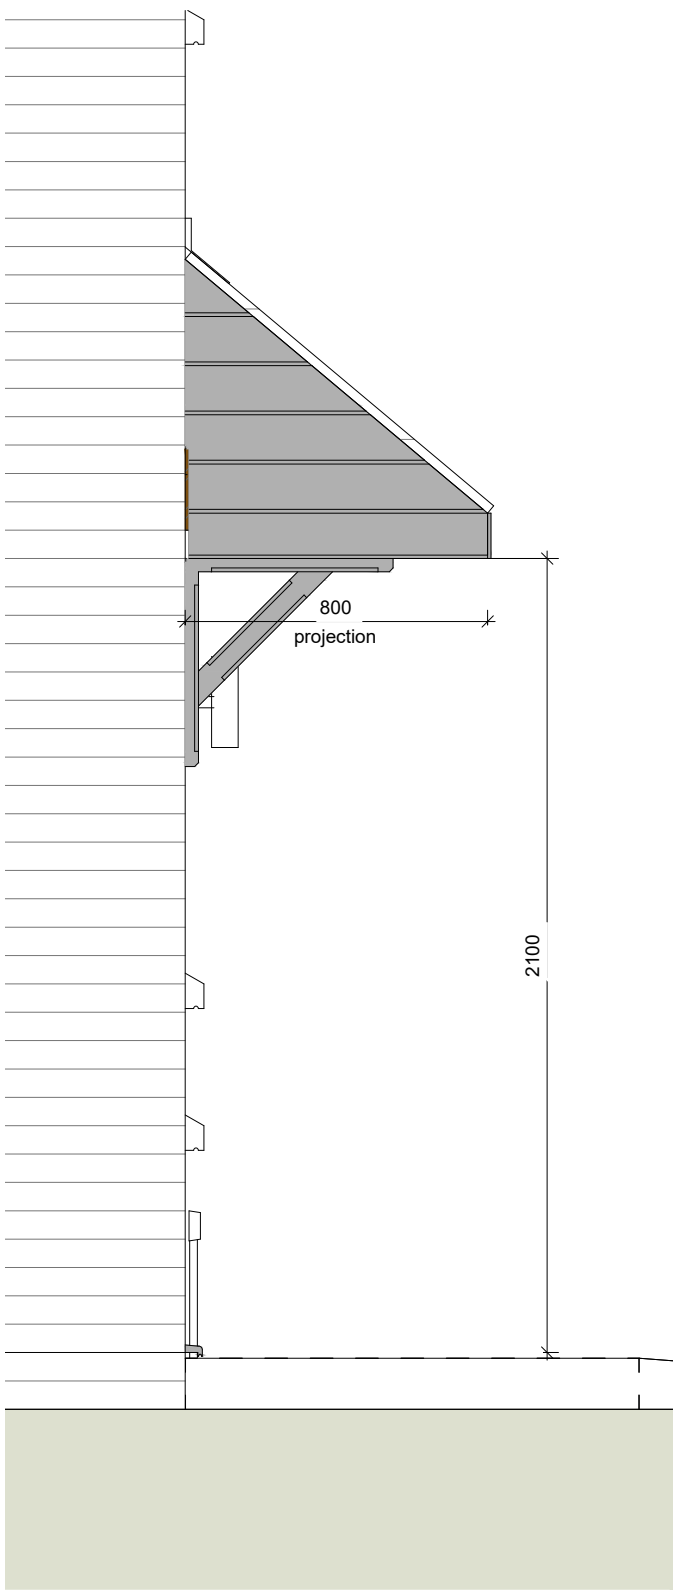

2 Gable Elevation
1 : 20

CONSTRUCTION **Bellway**
www.bellway.co.uk

Bellway Homes (Eastern Counties)
Building 2030, Cambourne Business Park,
Cambridgeshire CB23 6DW
Tel: 01480 425 200

Project
Somersham
St Ives Road
Working Drawings

Drawing Title
The Coppersmith-Life **CSL-3B-2S-CB**
1026 ft² | 3b Det / Semi | Country Brick
Canopy Details

Drawing Created By Group	First Issue Date April '25	Scale(s) 1 : 20
Project No BI01	Drg Status Construction	Revision C1
Drawing No.		BI01/1026CSL/65/CB/01

Plots 08, 14, 50 (AS) & 01, 03, 09, 18, 19, 49 OPP

Do not scale - if in doubt, ask