


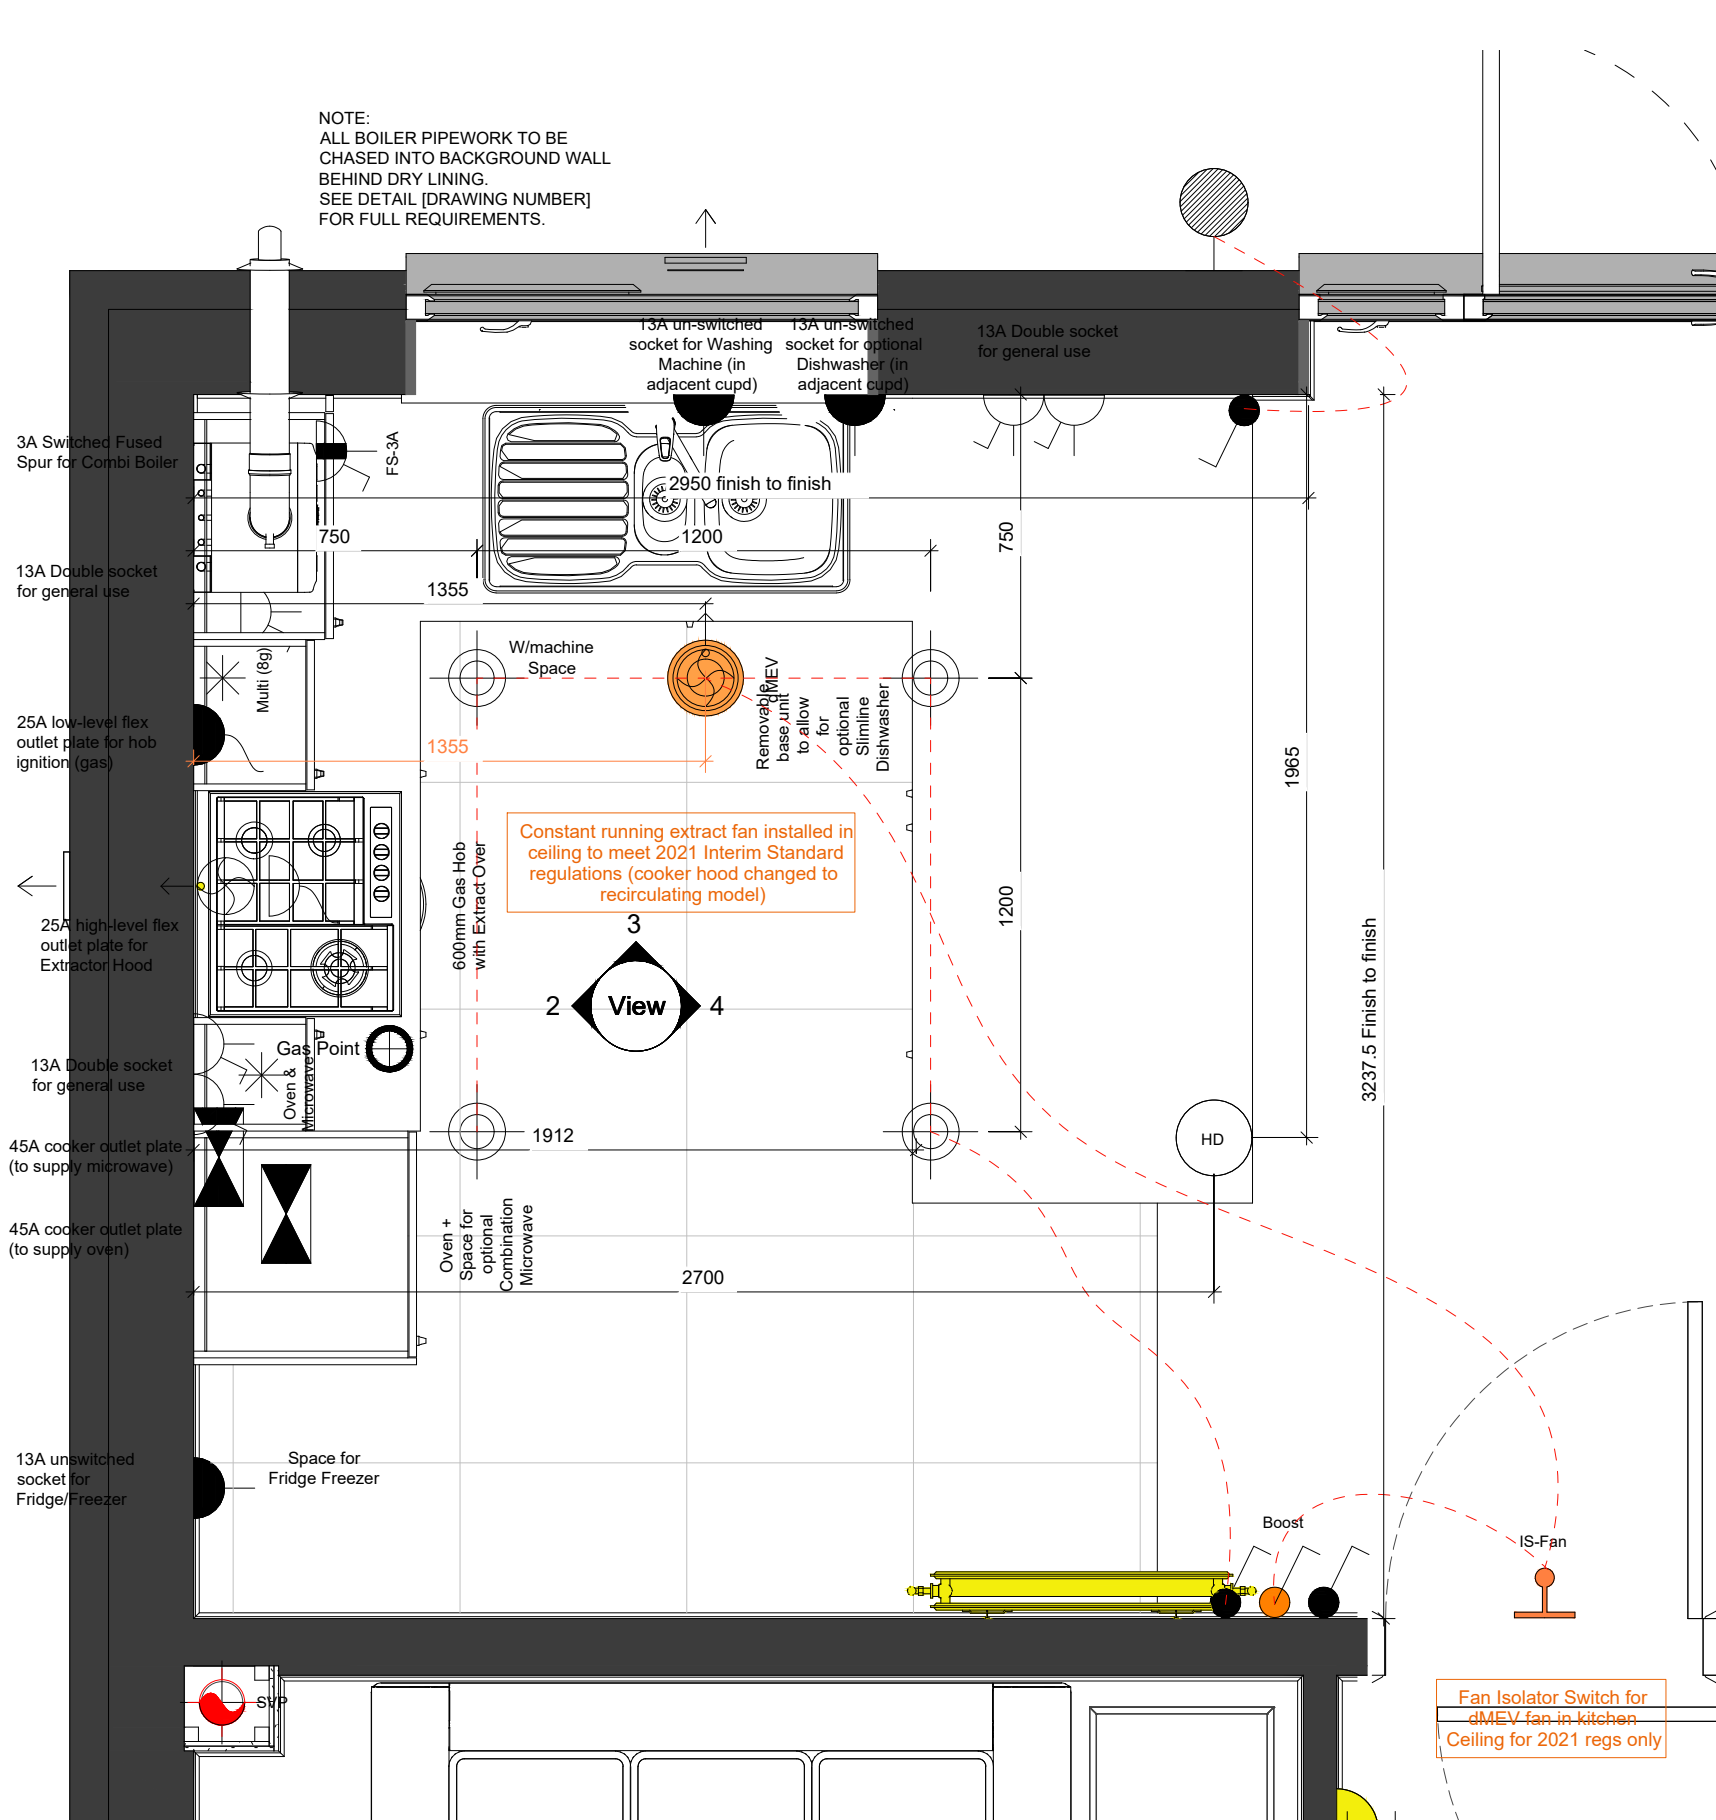

| Revision Schedule |          |                    |        |
|-------------------|----------|--------------------|--------|
| Rev               | Date     | Description        | Drn By |
| C1                | 27.11.25 | Construction Issue | -      |

### Kitchen Electrical Legend

|                                                                                     |                                                                |                                                                                  |                                                                                     |                                                                                                |                                                                                     |                                                                                     |                                                                                     |                                                                            |
|-------------------------------------------------------------------------------------|----------------------------------------------------------------|----------------------------------------------------------------------------------|-------------------------------------------------------------------------------------|------------------------------------------------------------------------------------------------|-------------------------------------------------------------------------------------|-------------------------------------------------------------------------------------|-------------------------------------------------------------------------------------|----------------------------------------------------------------------------|
|  | Pendant light fitting                                          |                                                                                  |  | Light switch - Intermediate <sup>(1)</sup>                                                     |                                                                                     |  | Wall mounted CO detector<br>(installed @ 2000mm above FFL)                          |                                                                            |
|  | Batten holder fitting                                          |                                                                                  |  | AC isolator switch for solar panels                                                            |                                                                                     |  |  | 25A Flex outlet plate high level <sup>(2)</sup>   low level <sup>(3)</sup> |
|  | IP65 recessed spotlight                                        |                                                                                  |  | Fan isolator switch (installed to centreline of door, 2150mm above FFL to underside of switch) |                                                                                     |  | Cooker outlet plate <sup>(3)</sup> with 6mm Ø cable to 45A double pole switch       |                                                                            |
|  | IP65 recessed spotlight to be supplied with Fire Hood / Shroud |                                                                                  |  | 13A Single Un-switched fused spur connection                                                   |                                                                                     |  | 45A double pole switch <sup>(2)</sup> with 6mm Ø cable to distribution board        |                                                                            |
|  | External Wall mounted light fitting                            |                                                                                  |  |             | Double pole switched fused spur connection (13A   3A)                               |  | Consumer unit (underside of unit installed 1350mm above FFL)                        |                                                                            |
|  | Multi (8g)                                                     | Remote switches to unswitched sockets <sup>(2)</sup><br>Single   Multi (8no max) |  |             | Single unswitched socket (13A) high level <sup>(2)</sup>   low level <sup>(3)</sup> |  |  | Ceiling mounted detector Smoke   Heat                                      |
|  | Light switch 1 way <sup>(1)</sup><br>1   2   3 gang            |                                                                                  |  |             | Single switched socket (13A) high level <sup>(2)</sup>   low level <sup>(3)</sup>   |  |  | Room thermostat <sup>(1)</sup><br>Zone 1   Zone 2                          |
|  | Light switch 2 way <sup>(1)</sup><br>1   2   3 gang            |                                                                                  |  |             | Double switched socket (13A) high level <sup>(2)</sup>   low level <sup>(3)</sup>   |                                                                                     |                                                                                     |                                                                            |

- <sup>(1)</sup> Switches / controls installed @ 1200mm above FFL to top of fitting  
<sup>(2)</sup> Switches installed @ 1050mm above FFL to underside of fitting (sockets located in kitchen islands to be mounted @ 750mm above FFL)  
<sup>(3)</sup> Switches installed @ 450mm above FFL to underside of fitting
- General Note - sockets located 400mm from internal corners of rooms to centrelines of sockets, unless otherwise stated

|  |   |
|--|---|
|  | Ceiling mounted extract fan (arrow indicates ducting direction, RT = roof terminal)<br><br>Yellow = intermittent fan for 2013 regs, dMEV fan for 2021 regs.<br><br>Orange = dMEV for 2021 regs only; no fan required for 2013 regs.<br>(dMEV = Decentralised Mechanical Extract Ventilation - System 3)<br><br>See 95/0/02 for details of individual fan requirements |
|  | Wall mounted extract fan (installed @ 2000mm above FFL to centreline).<br><br>Yellow = intermittent fan for 2013 regs, dMEV fan for 2021 regs.<br><br>Orange = dMEV for 2021 regs only; no fan required for 2013 regs.<br>(dMEV = Decentralised Mechanical Extract Ventilation - System 3)<br><br>See 95/0/02 for details of individual fan requirements              |
|  | Orange Boost Switch - lightswitch to control boost function of dMEV fan (2021 specification only)   |
|  | Orange Isolator Switch - 2021 specification switch only.<br>Text identifies use (IS - Fan = Extract Fan Isolator   AC Solar = Solar Inverter AC Isolator)   |

**2021 Regulations**  
All radiators sizes illustrated here are to satisfy 2021 regulations.

All Radiators and Extract Fan locations shown in orange are to be provided for 2021 Regulation properties only.

Refer to 80 series drawings for Radiator schedules and sizes, and refer to 95 series for Extract Fan schedules for both 2013 and 2021 regulations.

CONSTRUCTION

**Bellway**  
www.bellway.co.uk

**Bellway Homes (Eastern Counties)**  
Building 2030, Cambourne Business Park,  
Cambridgeshire CB23 6DW  
Tel: 01480 425 200

Project  
**Somersham**  
St Ives Road  
Working Drawings

Drawing Title  
**The Coppersmith-Life** **CSL-3B-2S-0**

1026 ft² | 3b Det / Semi | All Variants  
Kitchen Layout - Standard

|                             |                               |                          |
|-----------------------------|-------------------------------|--------------------------|
| Drawing Created By<br>Group | First Issue Date<br>April '25 | Scale(s)<br>As indicated |
| Project No<br>BI01          | Drg Status<br>Construction    | Revision<br>C1           |
| Drawing No.                 |                               | BI01/1026CSL/70/0/S/01   |

Plots 08, 14, 50 (AS) & 01, 03, 09, 18, 19, 49 OPP