


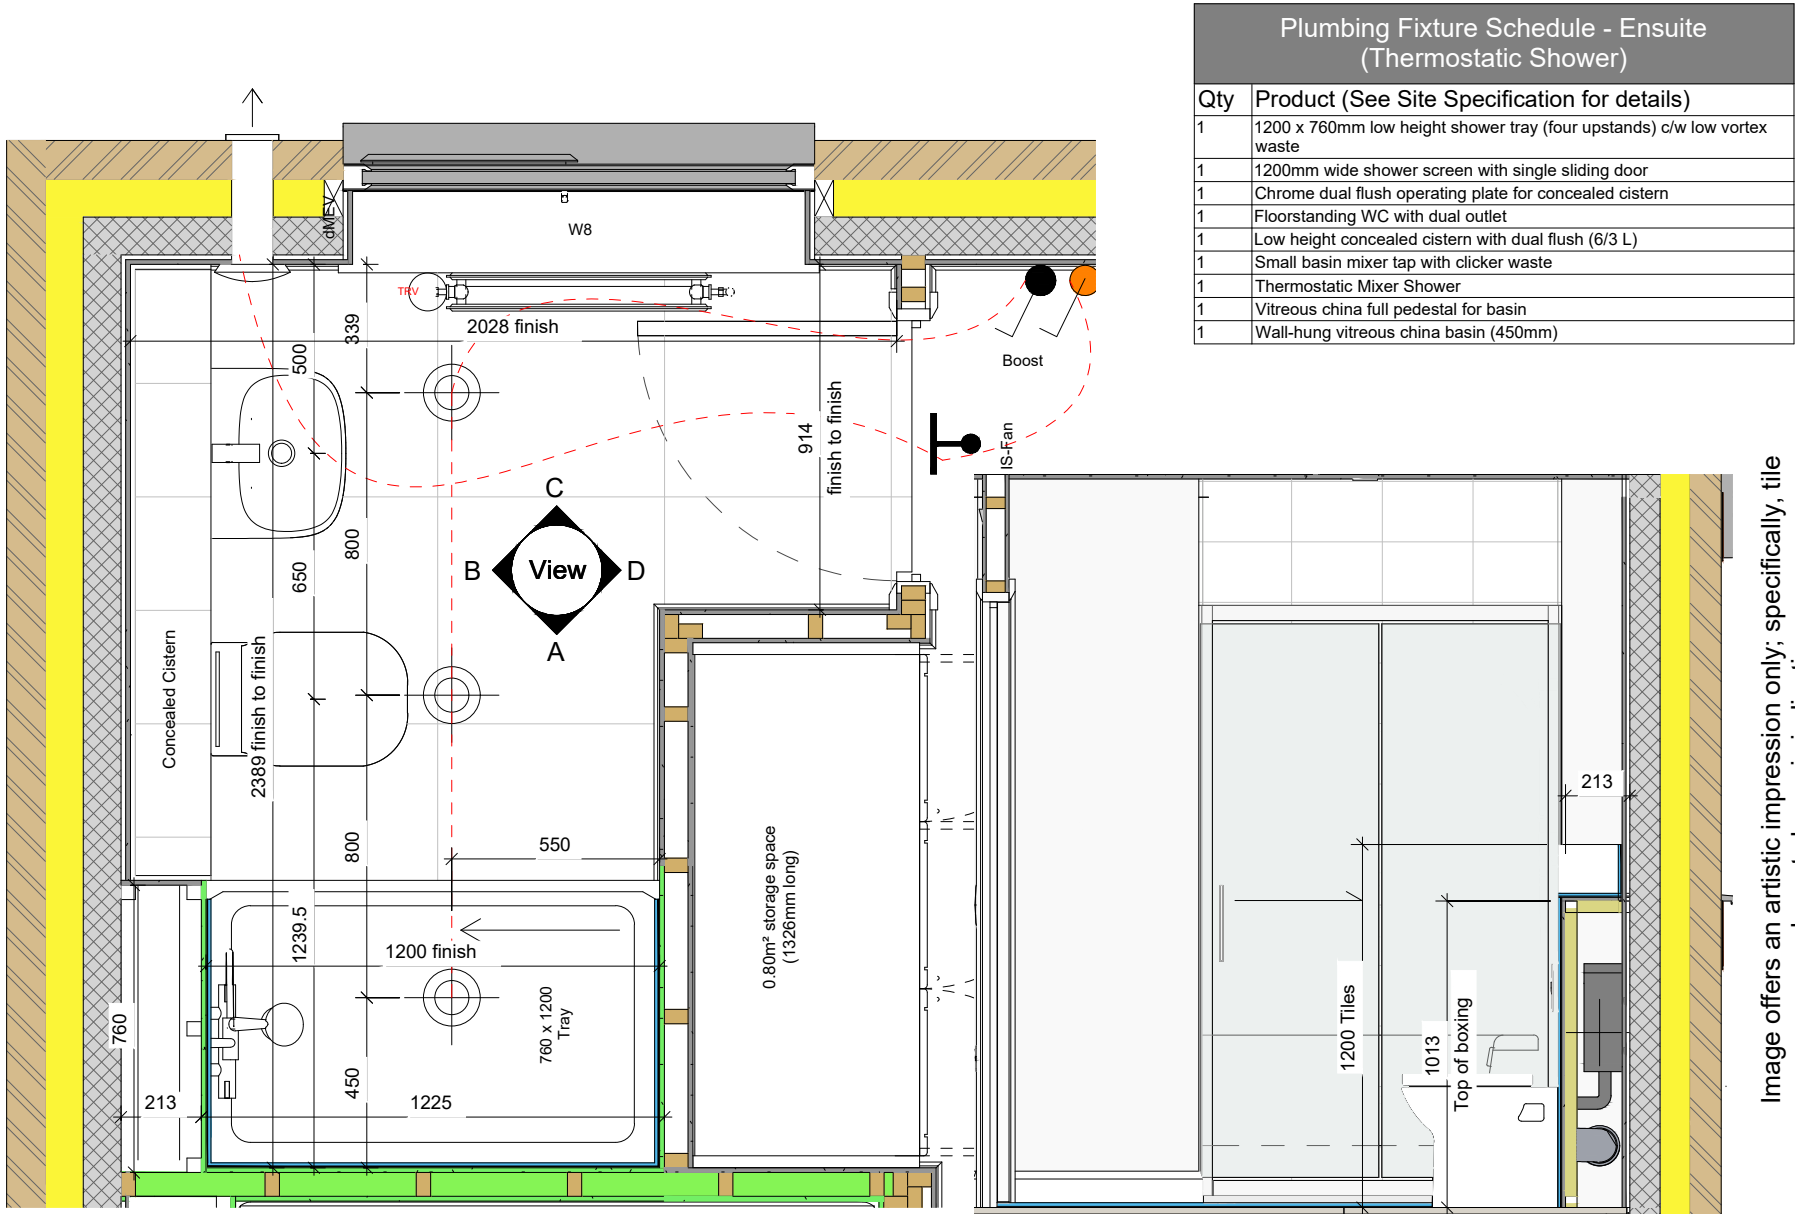

Plumbing Fixture Schedule - Ensuite (Thermostatic Shower)	
Qty	Product (See Site Specification for details)
1	1200 x 760mm low height shower tray (four upstands) c/w low vortex waste
1	1200mm wide shower screen with single sliding door
1	Chrome dual flush operating plate for concealed cistern
1	Floorstanding WC with dual outlet
1	Low height concealed cistern with dual flush (6/3 L)
1	Small basin mixer tap with clicker waste
1	Thermostatic Mixer Shower
1	Vitreous china full pedestal for basin
1	Wall-hung vitreous china basin (450mm)

2021 Regulations
All radiators sizes illustrated here are to satisfy 2021 regulations.

All Radiators and Extract Fan locations shown in orange are to be provided for 2021 Regulation properties only.

Refer to 80 series drawings for Radiator schedules and sizes, and refer to 95 series for Extract Fan schedules for both 2013 and 2021 regulations.

Revision Schedule			
Rev	Date	Description	Drn By
C1	27.11.25	Construction Issue	-

Notes

Artisan Collection 3 bedroom properties with a bathroom and ensuite are available with four heating options:-

Combination Boiler

Default (Base Specification) - No shower over bath (bath taps fitted with flow restrictors), thermostatic shower in ensuite.

Option 1 - Thermostatic shower over bath, plus thermostatic shower in ensuite.
Option 2 - No shower over bath, electric shower in ensuite.

Heat Only Boiler with Hot Water Cylinder *

4) No shower over bath, thermostatic shower in ensuite.

For bathroom and ensuite layouts pertaining to the above numbered options, please see the following drawings.

<u>Combination Boiler</u>		
Option No. Drawing No.	Bathroom Drawing No.	Ensuite
1) Default	75/0/A/02	75/0/A/03
2) Option 1	75/0/B/02	75/0/A/03
3) Option 2	75/0/A/02	75/0/B/03

<u>Heat Only Boiler with Hot Water Cylinder *</u>		
Option No. Drawing No.	Bathroom Drawing No.	Ensuite
4)	75/0/A/02	75/0/A/03

* Heating designs for 3 bed properties with Heat Only Boilers and Hot Water Cylinders should be taken from 80 series drawings, affixed "CYL" - i.e., "A/123/80/AT/CYL/01"

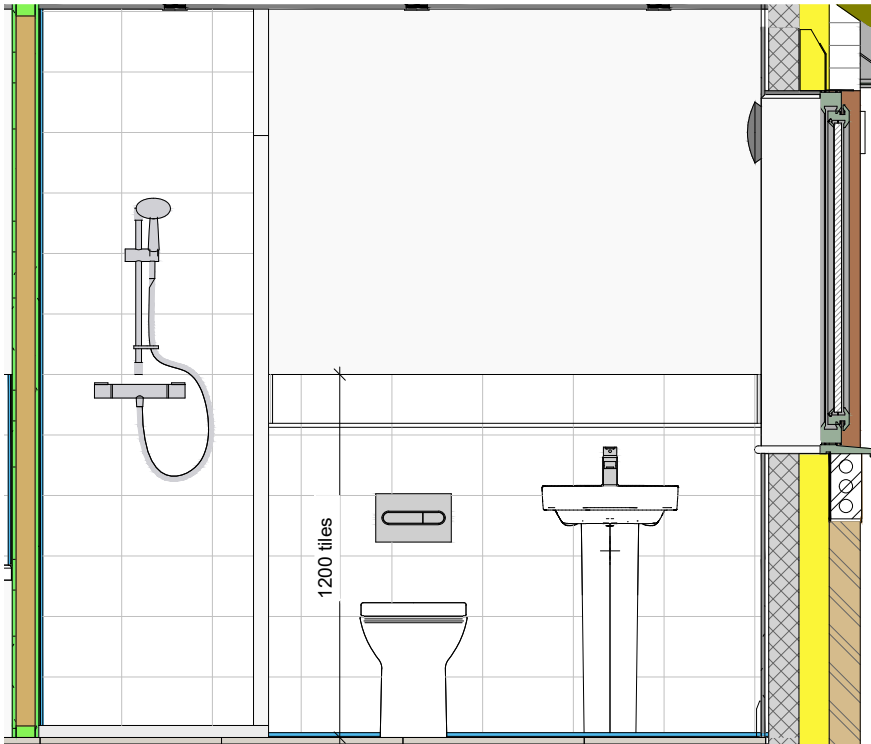


Image offers an artistic impression only; specifically, tile layout shown is indicative


1 Ensuite Layout
1 : 20

A Ensuite - View A
1 : 25


2 Ensuite (Thermostatic Shower) - 3D View
NTS



B Ensuite - View B
1 : 25

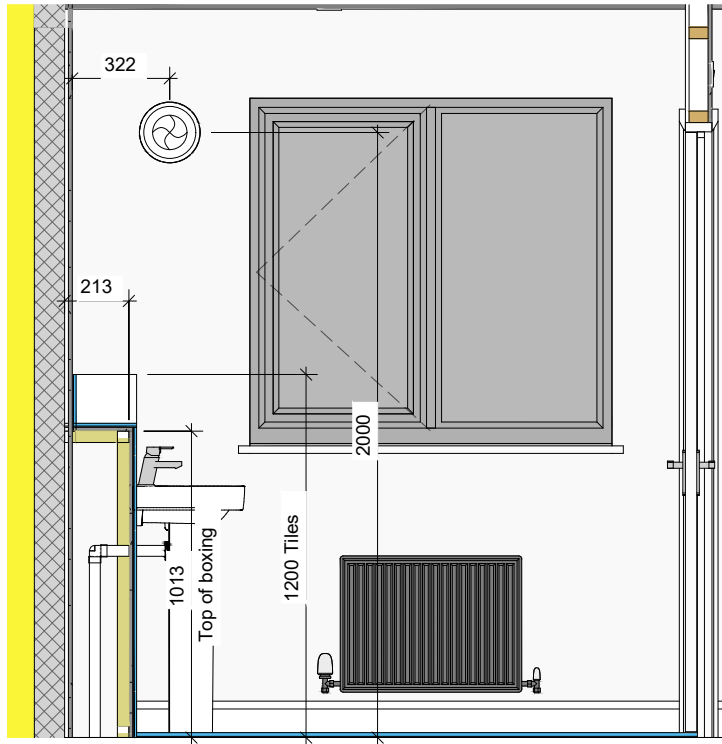

C Ensuite - View C
1 : 25

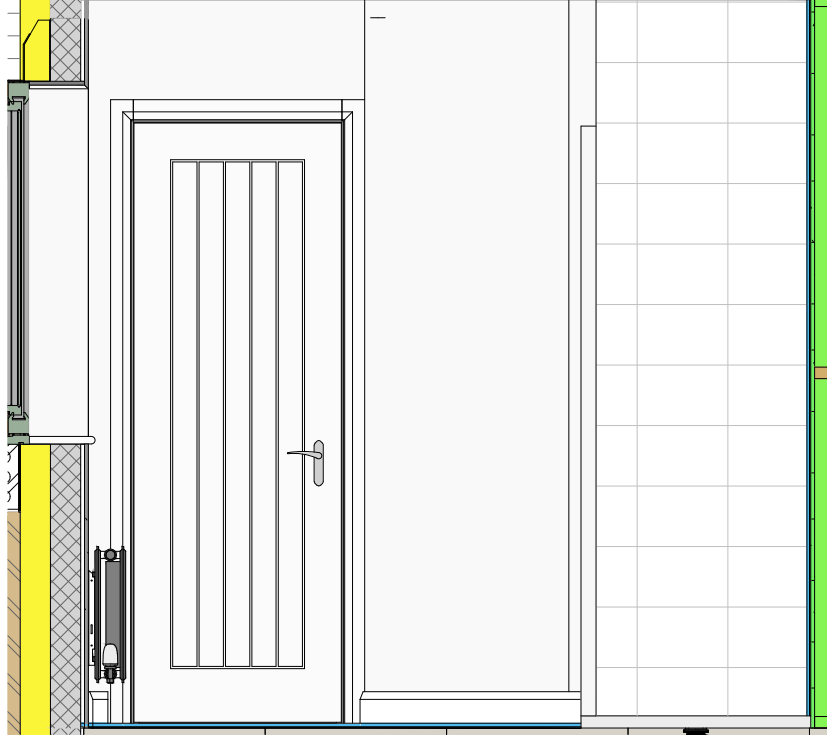

D Ensuite - View D
1 : 25

Plots 08, 14, 50 (AS) & 01, 03, 09, 18, 19, 49 OPP

CONSTRUCTION


www.bellway.co.uk

Bellway Homes (Eastern Counties)

Building 2030, Cambourne Business Park,
Cambridgeshire CB23 6DW
Tel: 01480 425 200

Project

Somersham
St Ives Road
Working Drawings

Drawing Title

The Coppersmith-Life

CSL-3B-2S-0

1026 ft² | 3b Det / Semi | All Variants

Ensuite Layout (Thermostatic Shower)

Drawing Created By	First Issue Date	Scale(s)
Group	April '25	As indicated
Project No	Drg Status	Revision
BI01	Construction	C1
Drawing No.	BI01/1026CSL/75/0/A/03	

Do not scale - if in doubt, ask