


Revision Schedule			
Rev	Date	Description	Drn By
C1	28.11.25	Construction Issue	-

Part O requirements:-
Safety Rail to be installed at 1100mm, which may be omitted if
Build Tolerance to window opening is within a range of maximum
1100mm and minimum 1000mm

Refer to the civil engineering drawings for individual plot levels.

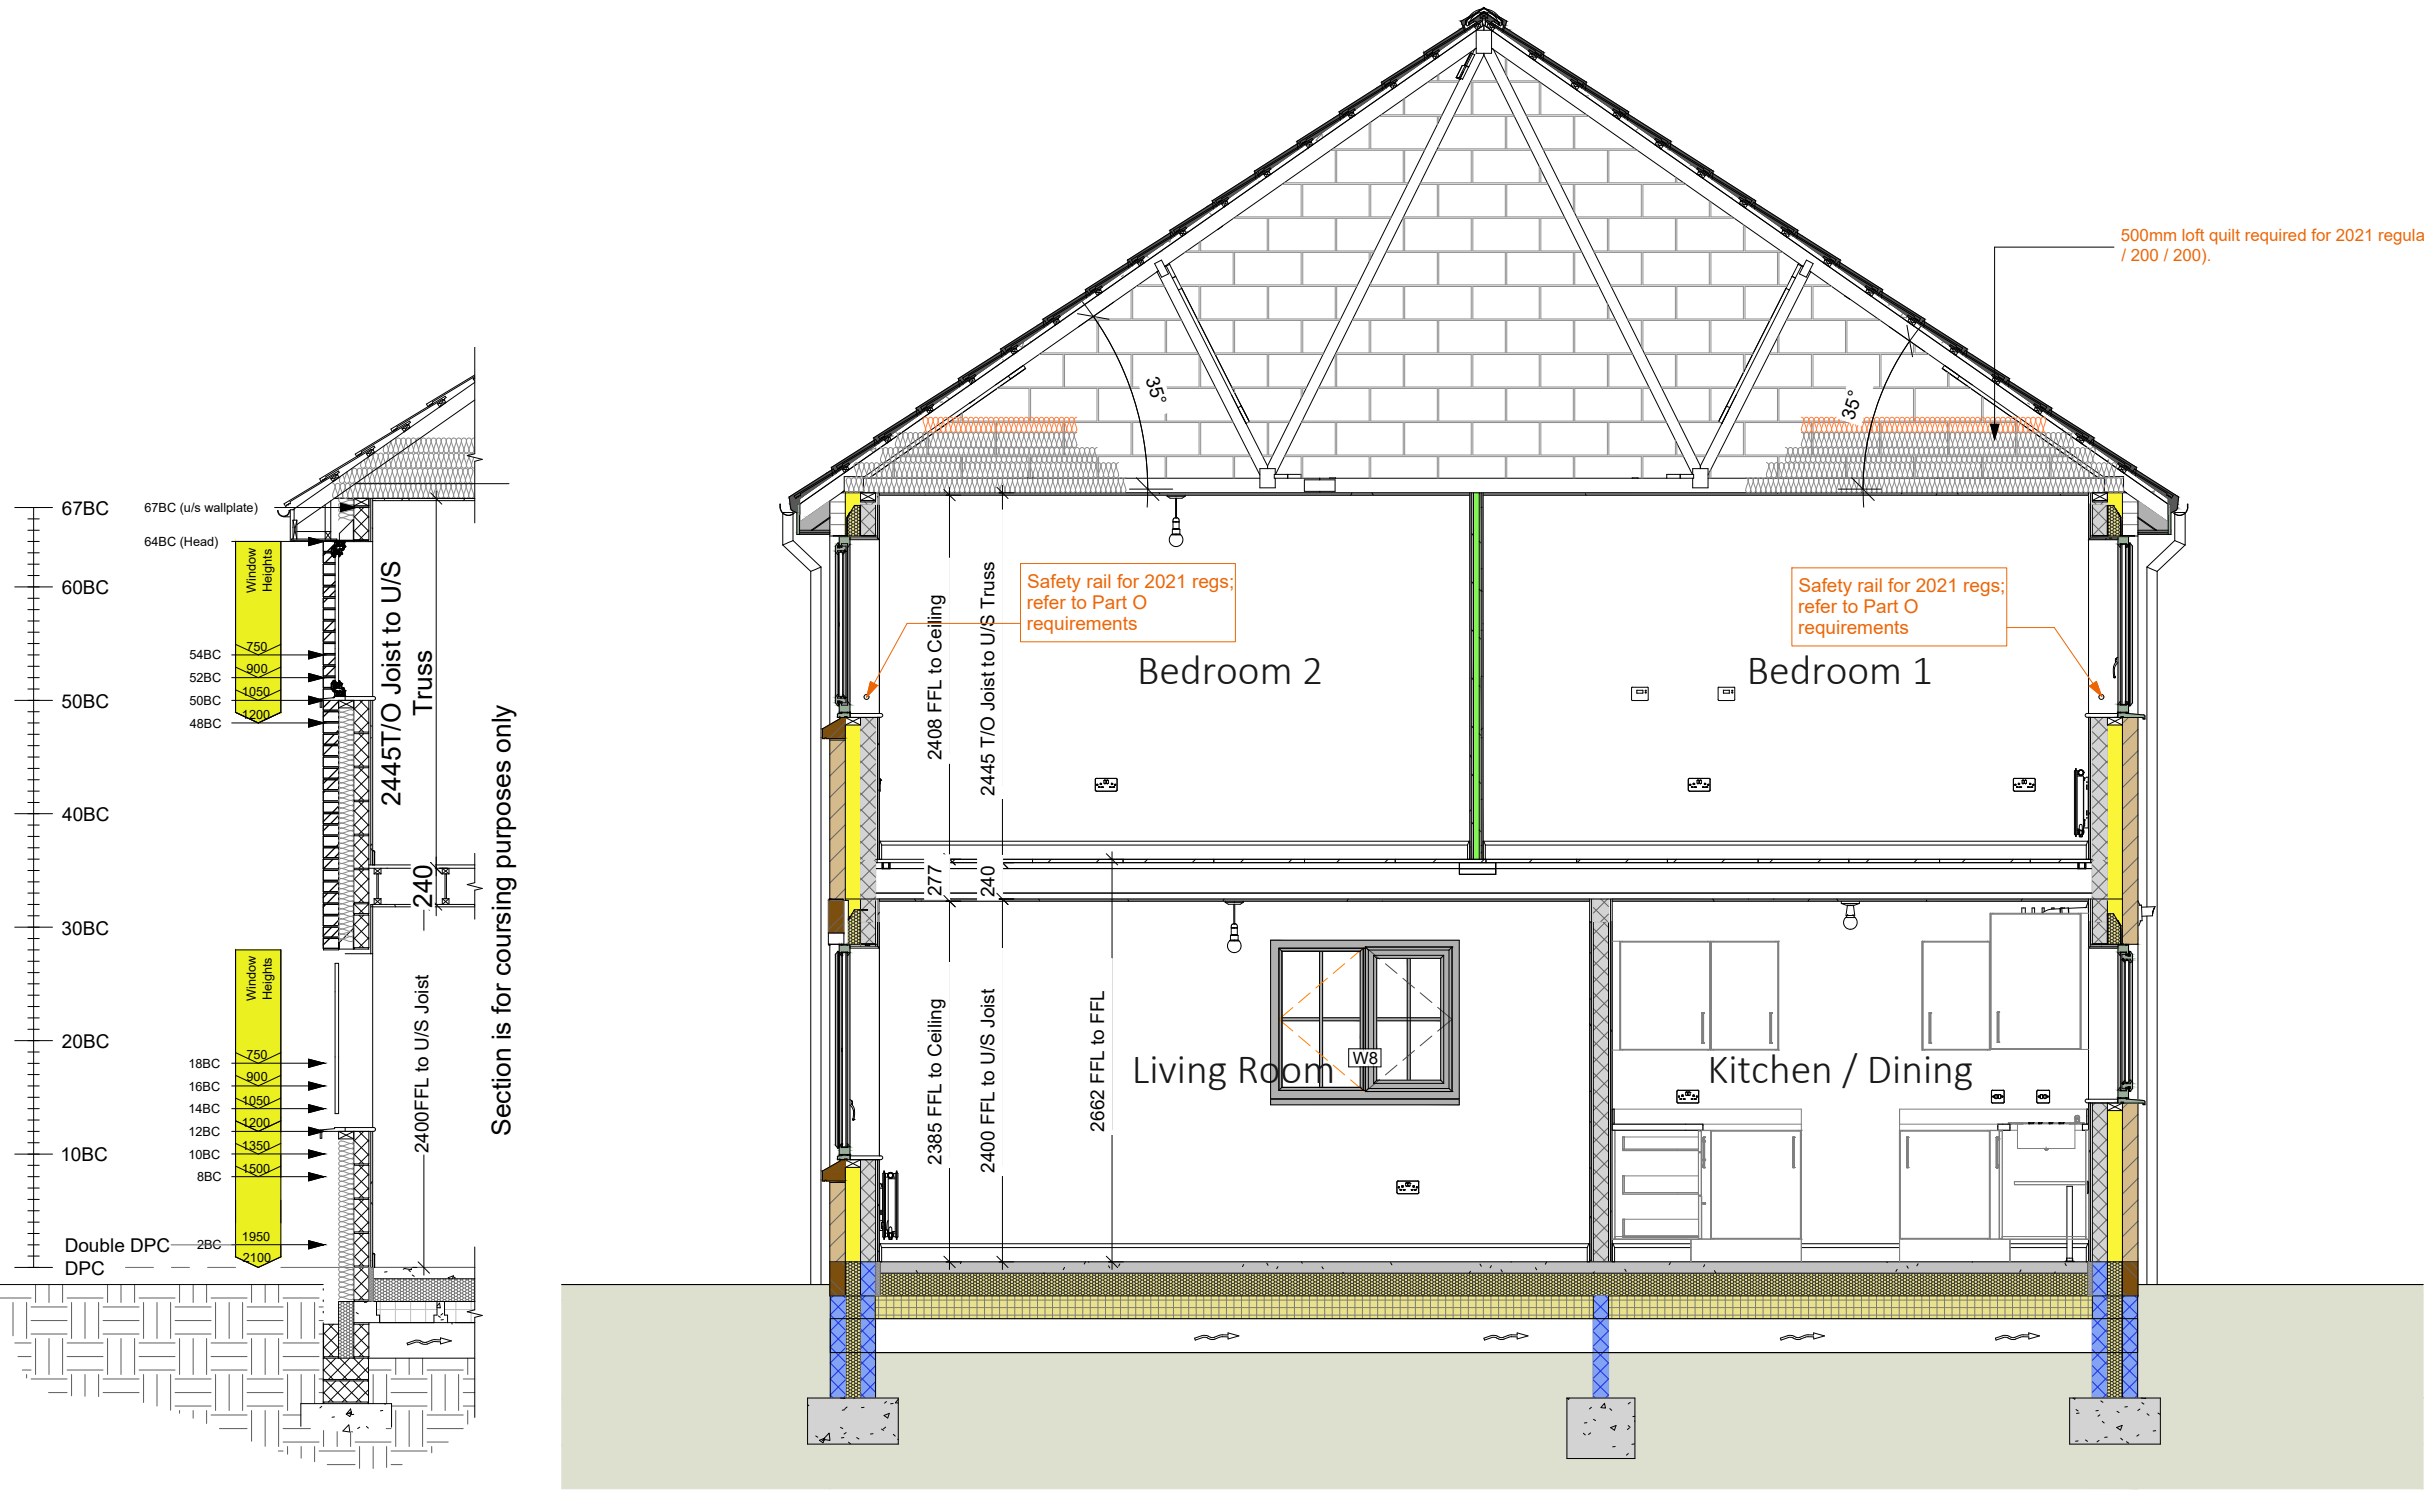

A Section A - A
1 : 50

CONSTRUCTION **Bellway**
www.bellway.co.uk

Bellway Homes (Eastern Counties)
Building 2030, Cambourne Business Park,
Cambridgeshire CB23 6DW
Tel: 01480 425 200

Project
Somersham
St Ives Road
Working Drawings

Drawing Title
The Draftsman-Life DML-3B-2S-AT

934 ft² | 3b Semi/Mid | All Traditional Variants
Section A-A

Drawing Created By Group	First Issue Date April '25	Scale(s) 1 : 50
Project No BI01	Drg Status Construction	Revision C1
Drawing No. BI01/934DML/20/AT/01		

Plots 32, 34, 36, 46 (AS) & 33, 35, 47 (OPP)

Do not scale - if in doubt, ask