


Revision Schedule			
Rev	Date	Description	Drn By
C1	28.11.25	Construction Issue	-


Substructure Wall Legend (100mm Cavity)

	Standard External Insulated Cavity Wall (Below Ground) 100mm blocks (3.6N/mm²) upto 150mm below external ground level, then class B engineering brickwork (102.5mm) to DPC level 100mm cavity with expanded polystyrene board (thermal conductivity 0.038 W/m²/K) 100mm aerated concrete block / coursing bricks (3.6N/mm²)
	External Uninsulated Cavity Wall (To Garage etc - Below Ground) 100mm blocks (3.6N/mm²) upto 150mm below external ground level, then class B engineering brickwork (102.5mm) to DPC level 100mm cavity 100mm aerated concrete block / coursing bricks (3.6N/mm²)
	Party Wall (Below Ground) 100mm aircrete block (3.6N/mm²) 100mm cavity with expanded polystyrene board (thermal conductivity 0.038 W/m²/K) 100mm aircrete block (3.6N/mm²)
	Internal Blockwork Partition (Below Ground) 100mm aerated concrete block (3.6N/mm²) (Suspended ground floor beam manufacturer's coursing blocks / bricks as required)
	Sleeper Wall 100mm aerated concrete block (3.6N/mm²) to underside of suspended ground floor beams

Refer to current Construction Specification for further details

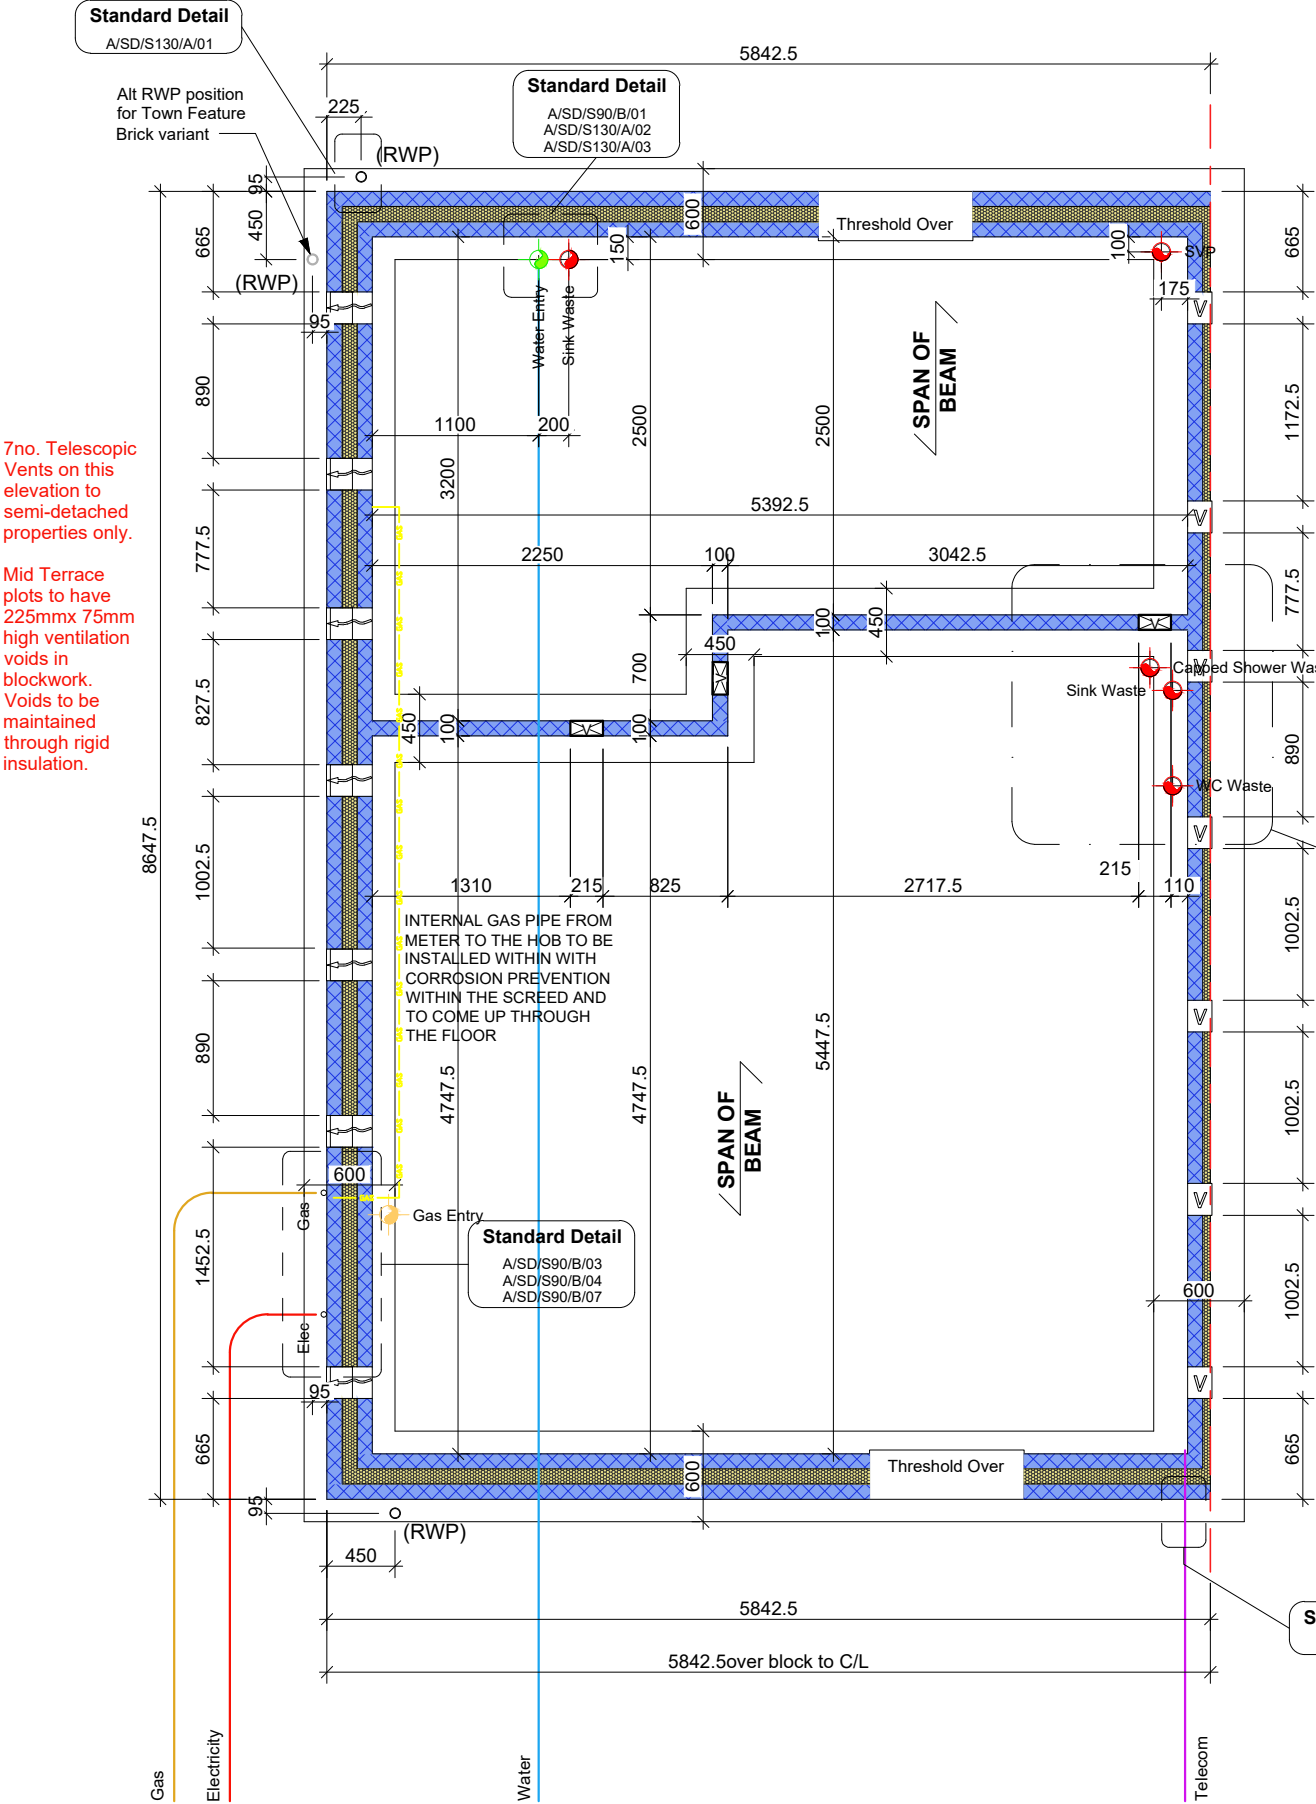


1 Foundation Plan with Semi Detached Service Entry Points
1 : 50

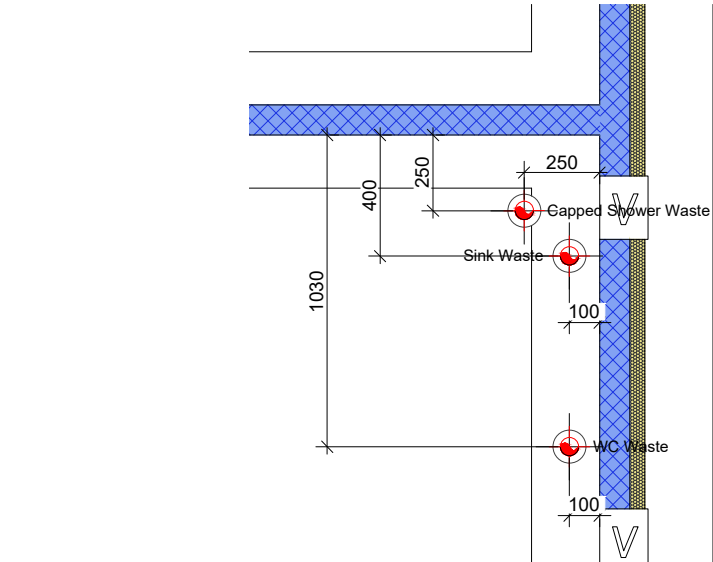

2 Mid Terrace Alternative Service Entry Points
1 : 50

3 Ground Floor WC Drainage Callout
1 : 25

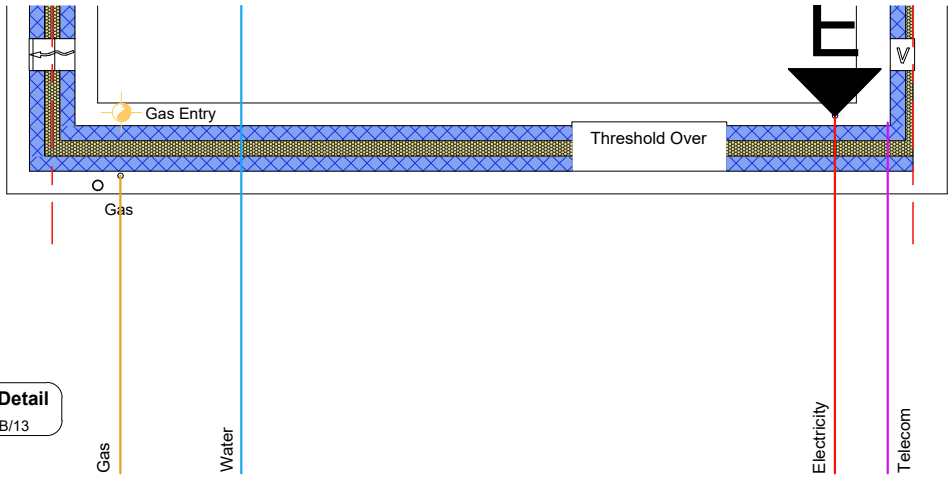

7no. Telescopic Vents on this elevation to semi-detached properties only.

Mid Terrace plots to have 225mmx 75mm high ventilation voids in blockwork. Voids to be maintained through rigid insulation.

Mid Terrace & Semi plots to have 7no. 225mm x 75mm high ventilation voids in blockwork. Voids to be maintained through rigid insulation.

Plots 32, 33, 34, 35, 37, 46 (AS) & 35, 36, 47 (OPP)

CONSTRUCTION

www.bellway.co.uk

Bellway Homes (Eastern Counties)
Building 2030, Cambourne Business Park,
Cambridgeshire CB23 6DW
Tel: 01480 425 200

Project
Somersham
St Ives Road
Working Drawings

Drawing Title
The Draftsman-Life
934 ft² | 3b Semi/Mid | All Variants
Foundation Layout

DML-3B-2S-0

Drawing Created By Group	First Issue Date 28.03.25	Scale(s) As indicated
Project No BI01	Drg Status Construction	Revision C1
Drawing No.		BI01/934DML/30/0/01

Do not scale - if in doubt, ask