


Revision Schedule			
Rev	Date	Description	Drn By
C1	28.11.25	Construction Issue	-

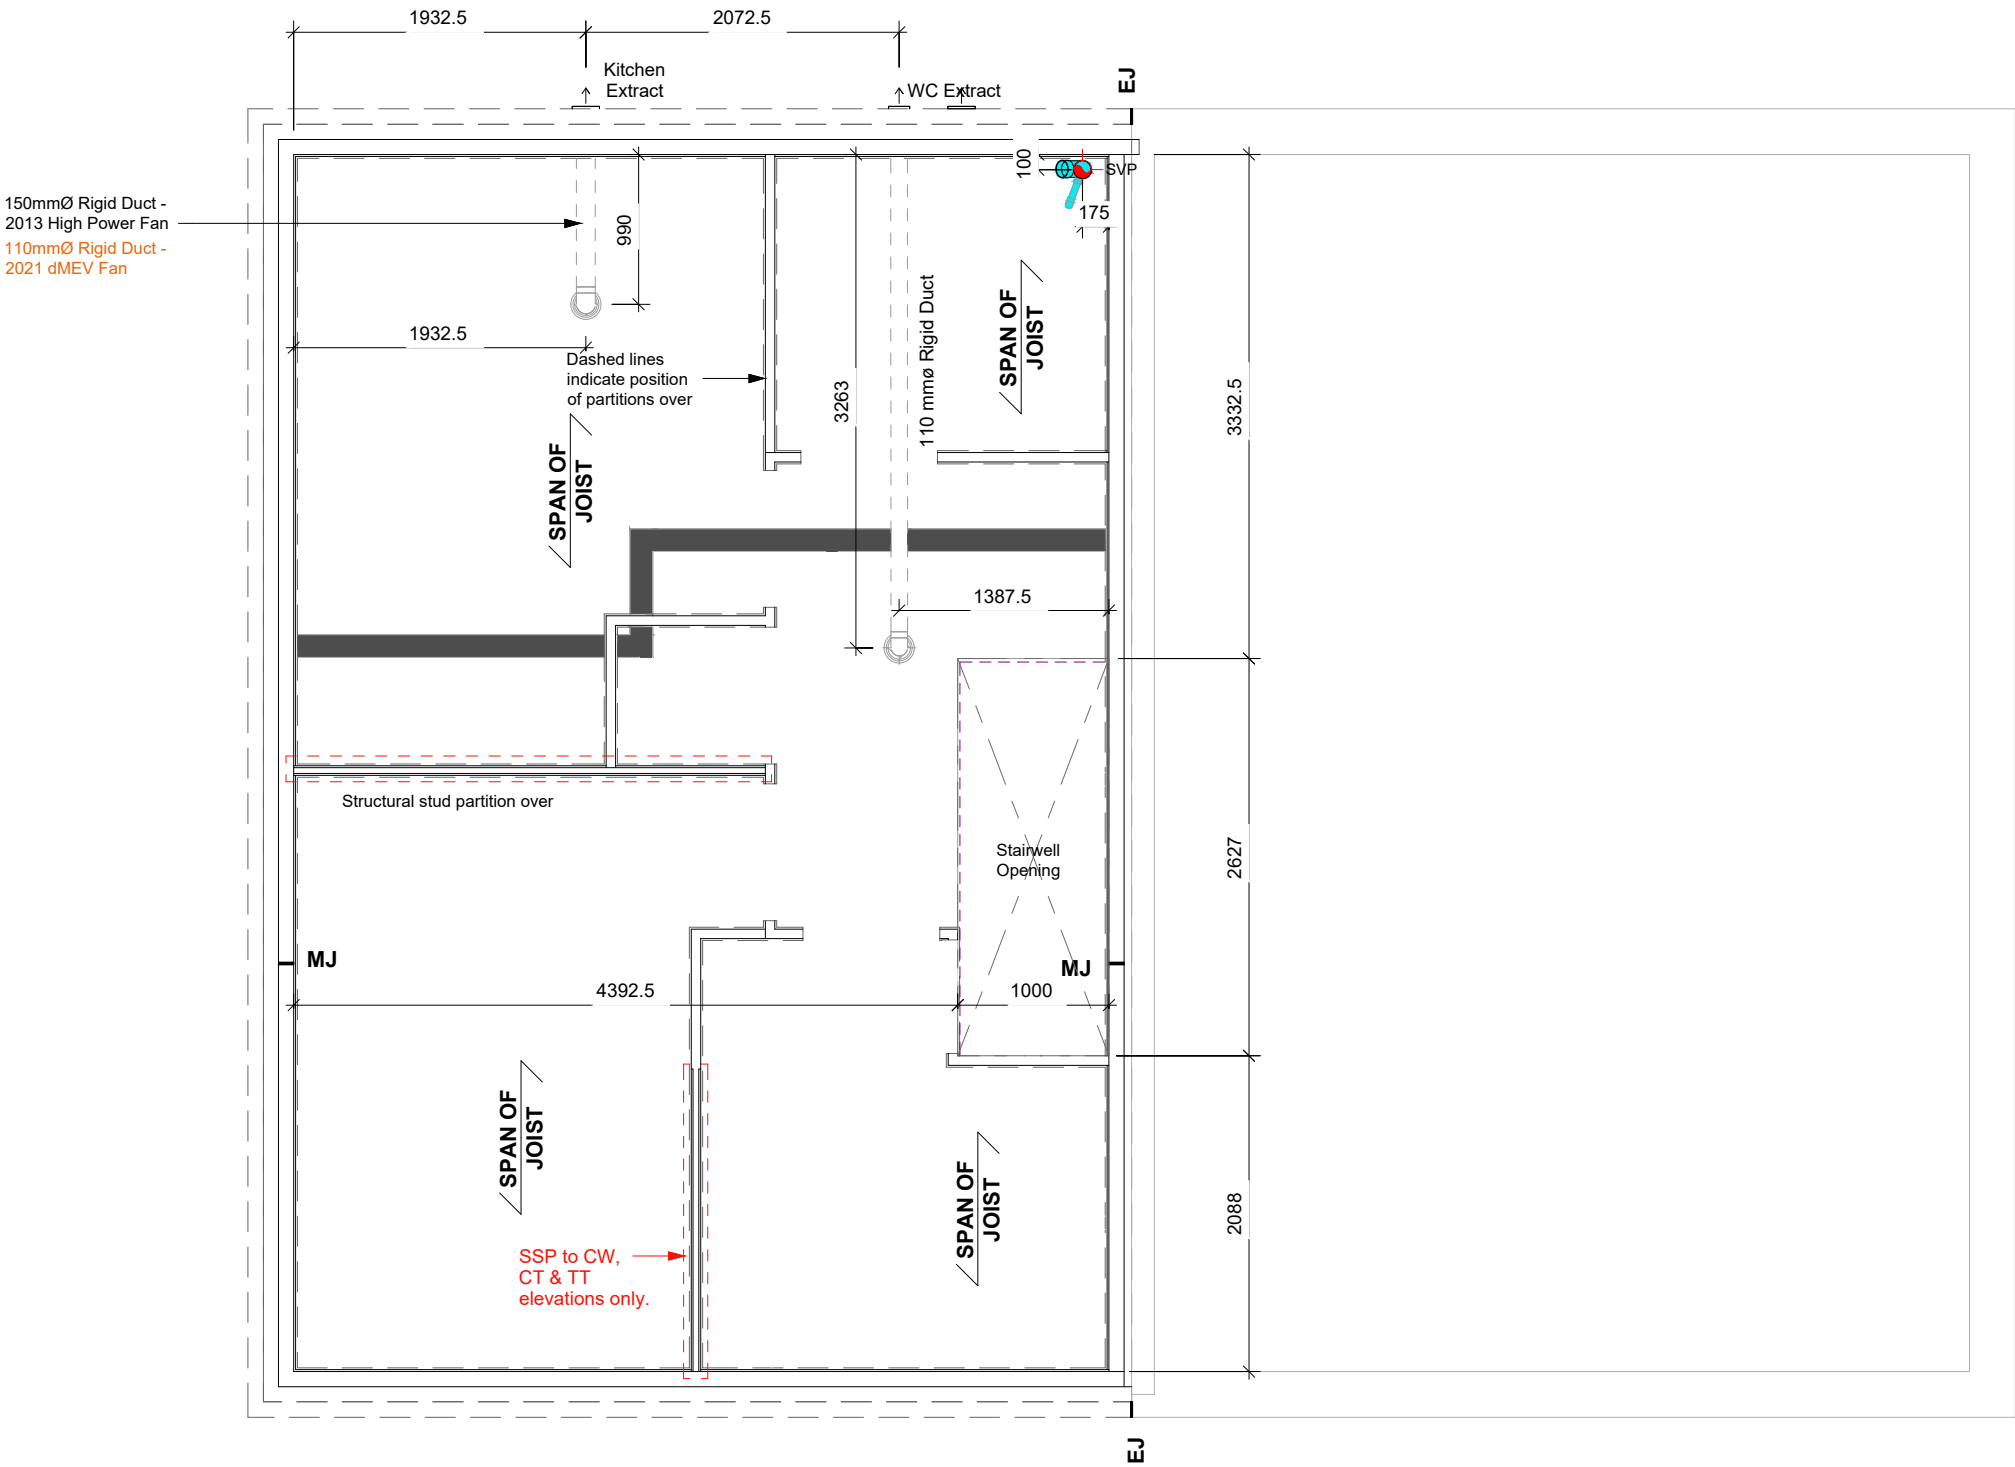

1 First Floor Joist Setting Out
1 : 50

Plots 32, 34, 36, 46 (AS) & 33, 35, 47 (OPP)

CONSTRUCTION

Bellway

www.bellway.co.uk

Bellway Homes (Eastern Counties)

Building 2030, Cambourne Business Park,
Cambridgeshire CB23 6DW
Tel: 01480 425 200

Project

Somersham
St Ives Road
Working Drawings

Drawing Title
The Draftsman-Life **DML-3B-2S-0**
934 ft² | 3b Semi/Mid | All Variants
First Floor Joist Setting Out

Drawing Created By Group	First Issue Date April '25	Scale(s) 1 : 50
Project No BI01	Drg Status Construction	Revision C1
Drawing No.		BI01/934DML/40/0/01

Do not scale - if in doubt, ask