


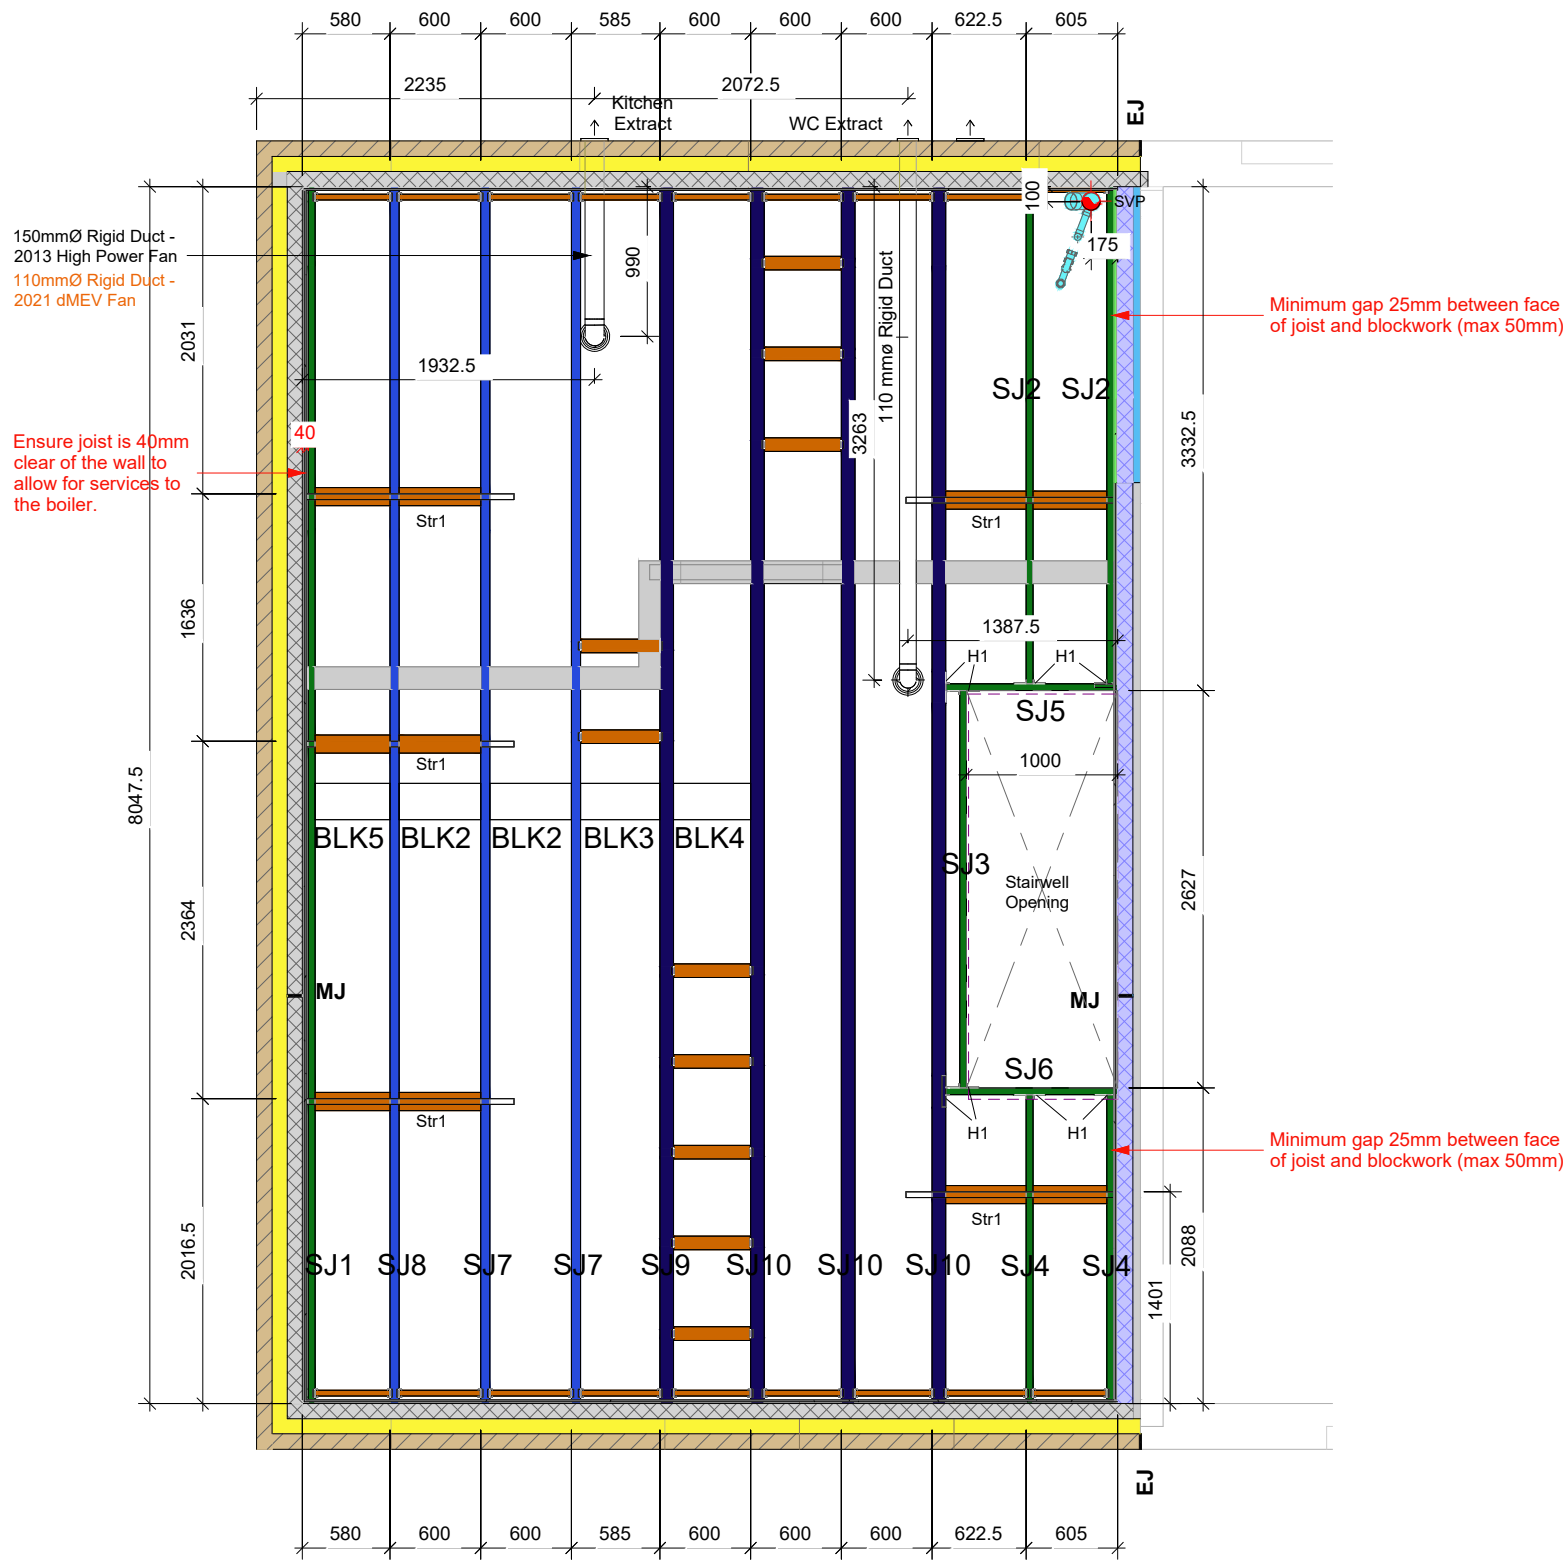

1 First Floor Joists
1 : 50

Steico First Floor Joists & Blocking

Qty	Ref	Length	Description
Beam/Joist			
1	SJ1	8248mm	ST4119 SJL 45 - 240mm
2	SJ2	3387mm	ST4119 SJL 45 - 240mm
1	SJ3	2627mm	ST4119 SJL 45 - 240mm
2	SJ4	2143mm	ST4119 SJL 45 - 240mm
1	SJ5	1238mm	ST4119 SJL 45 - 240mm
1	SJ6	1237mm	ST4119 SJL 45 - 240mm
2	SJ7	8248mm	ST4125 SJL 60 - 240mm
1	SJ8	8248mm	ST4125 SJL 60 - 240mm
1	SJ9	8248mm	ST4132 SJL 90 - 240mm
3	SJ10	8247mm	ST4132 SJL 90 - 240mm

Blocking			
4	BLK1	592mm	ST4022 STEICO LVL R - 39x240mm
3	BLK2	540mm	ST4022 STEICO LVL R - 39x240mm
1	BLK3	525mm	ST4022 STEICO LVL R - 39x240mm
1	BLK4	510mm	ST4022 STEICO LVL R - 39x240mm
1	BLK5	496mm	ST4022 STEICO LVL R - 39x240mm

Noggin			
18	CN1		G7002 38x38 Nogging
10	PN1		G7000 Partition Nogging (38x90)
15	SN1		G7055 38x120mm Nogging - Plank

Steico First Floor Accessories

Ref	Description	Qty
ZS38N Z Clip 38mm		
		56
End Device		
SES158/45	End Device	8
SES158/58	End Device	6
SES158/89	End Device	8
Hanger		
H1	EW(H)235/47	8
Strap		
Str1	G8304 Simpson HES15B10	5

Revision Schedule

Rev	Date	Description	Drn By
C1	28.11.25	Construction Issue	-

Project Information

File Name	STEICO DRAFTSMAN JUL 2024 - NHBC 2023 EC5 Analytics.skd 19 Jul 2024 1.0.222
Design Date	
Software Version No.	

Design Information

Region	UK
Design Code	EC5
Application	A - Residential Upper Floor
Service Class	Service Class 1

Load and Deflection Settings

Dead Load (kN/m²)	0.40 - Permanent
Partitions Load (kN/m²)	0.35 - Permanent
Floor Imposed UD Load (kN/m²)	1.50 - Medium Term
Floor Imposed Concentrated Load (kN)	2.00 - Medium Term

Instantaneous Deflection	333	-	12mm
Net Final Deflection	250	-	

Additional Information

Decking Type	Particle Board - 22mm P5
Direct Applied Ceiling	Yes
Ceiling Material	15mm - Ceiling (Gypsum board)



CONSTRUCTION



Bellway Homes (Eastern Counties)

Building 2030, Cambourne Business Park,
Cambridgeshire CB23 6DW
Tel: 01480 425 200

Project

Somersham

St Ives Road
Working Drawings

Drawing Title

The Draftsman-Life

DML-3B-2S-0

934 ft² | 3b Semi/Mid | All Variants
Joist Plan and Take Off

Drawing Created By	First Issue Date	Scale(s)
Group	April '25	1 : 50
Project No	Drg Status	Revision
BI01	Construction	C1
Drawing No.	BI01/93DML4/40/0/02	