


Revision Schedule			
Rev	Date	Description	Drn By
C1	28.11.25	Construction Issue	-

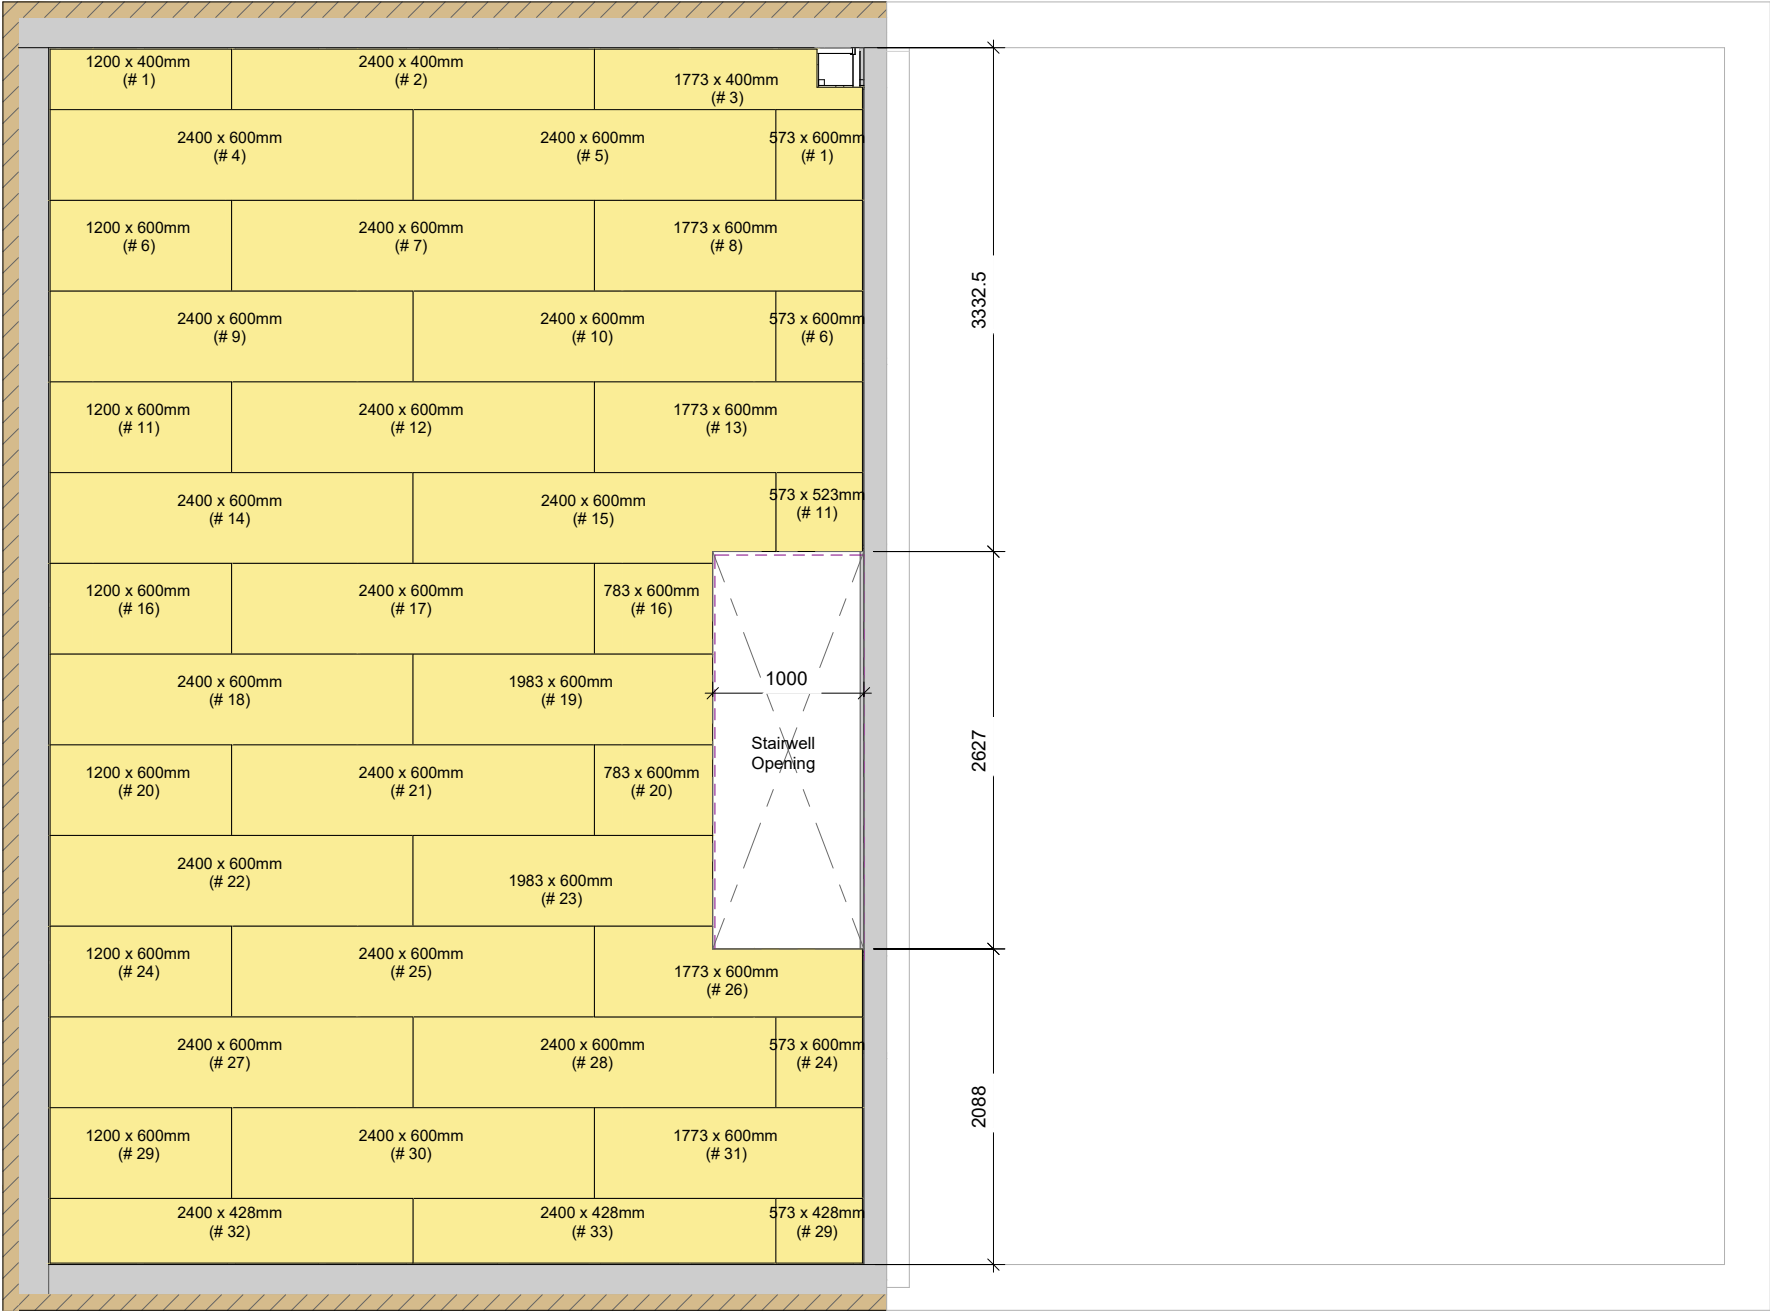

Floorboard Schedule	
Qty	Description
33	22mm thick tongue and grooved chipboard floor board (2400 x 600mm)

CONSTRUCTION

Bellway

www.bellway.co.uk

Bellway Homes (Eastern Counties)

Building 2030, Cambourne Business Park,
Cambridgeshire CB23 6DW
Tel: 01480 425 200

Project

Somersham
St Ives Road
Working Drawings

Drawing Title

The Draftsman-Life

934 ft² | 3b Semi/Mid | All Variants

Floor Boards Layout

DML-3B-2S-0

1

First Floor Floorboards

1 : 50

Plots 32, 34, 36, 46 (AS) & 33, 35, 47 (OPP)

Drawing Created By	First Issue Date	Scale(s)
Group	April '25	1 : 50
Project No	Drg Status	Revision
BI01	Construction	C1
Drawing No.		BI01/934DML/40/0/04

Do not scale - if in doubt, ask