


Staircraft Drawing Ref:


House Type Name: DRAFTSMAN
Handing*: RHWS
Finished Floor Level (FFL) 2662
Revision: -

*Handing of staircase to be confirmed at point of call off.


Revision Schedule			
Rev	Date	Description	Drn By
C1	28.11.25	Construction Issue	-

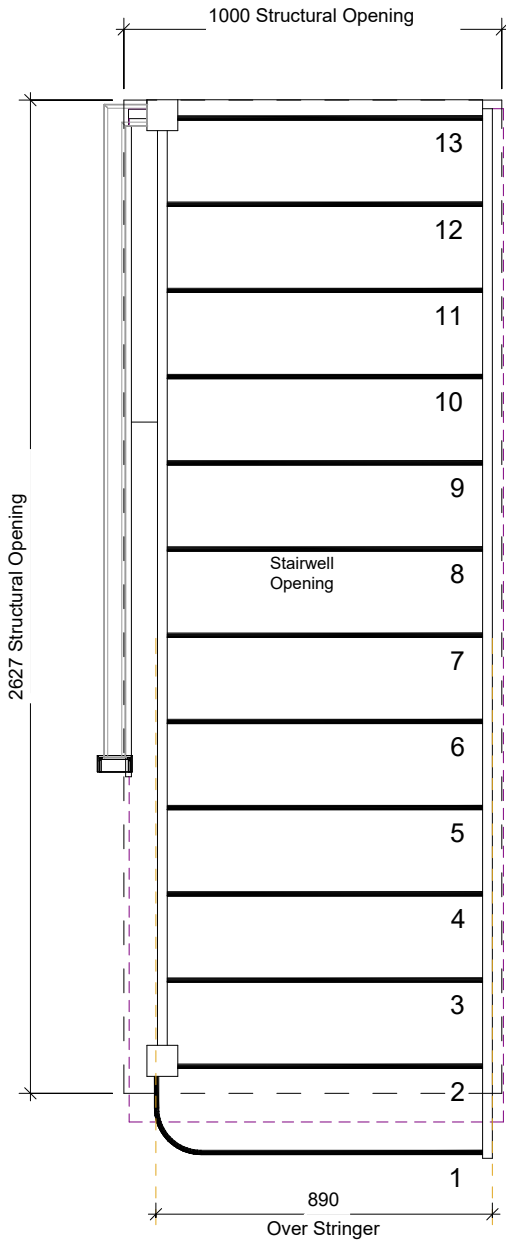

1 Staircase - Plan
1 : 20

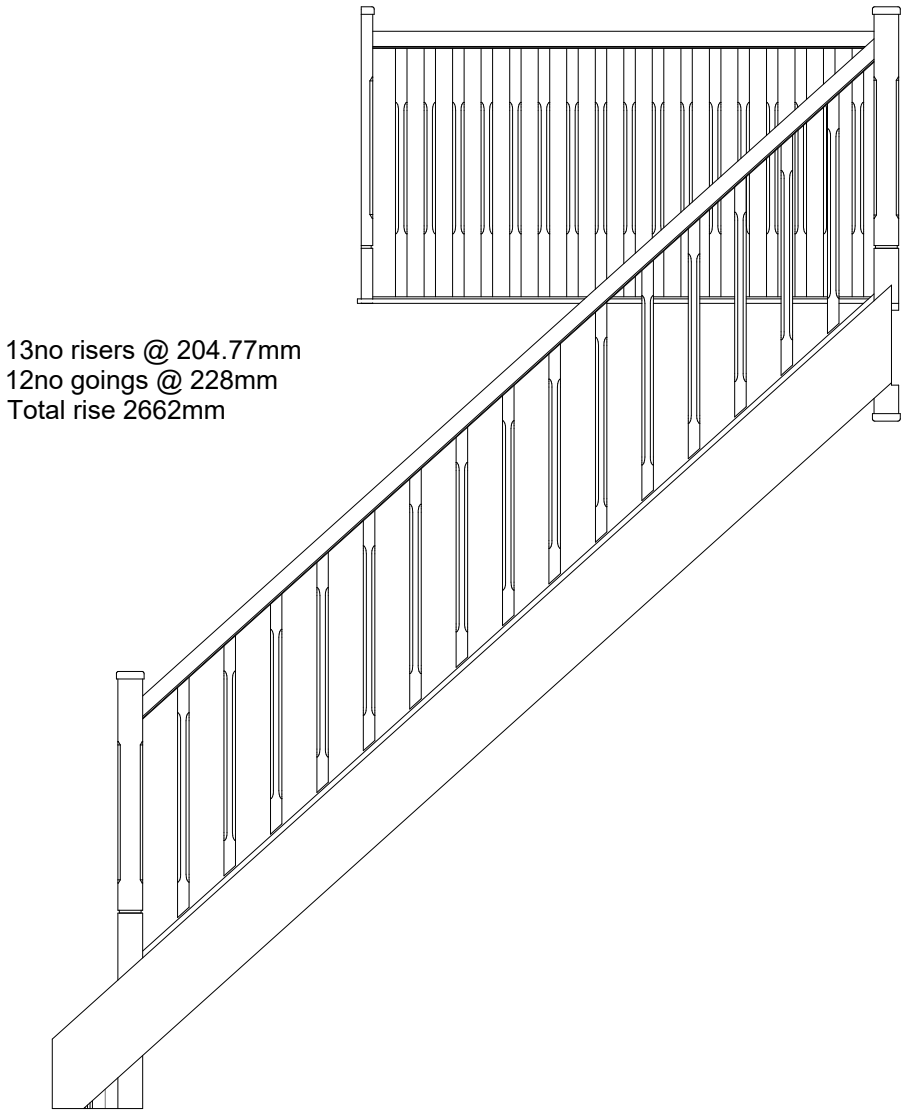

2 Stair - Elevation
1 : 25

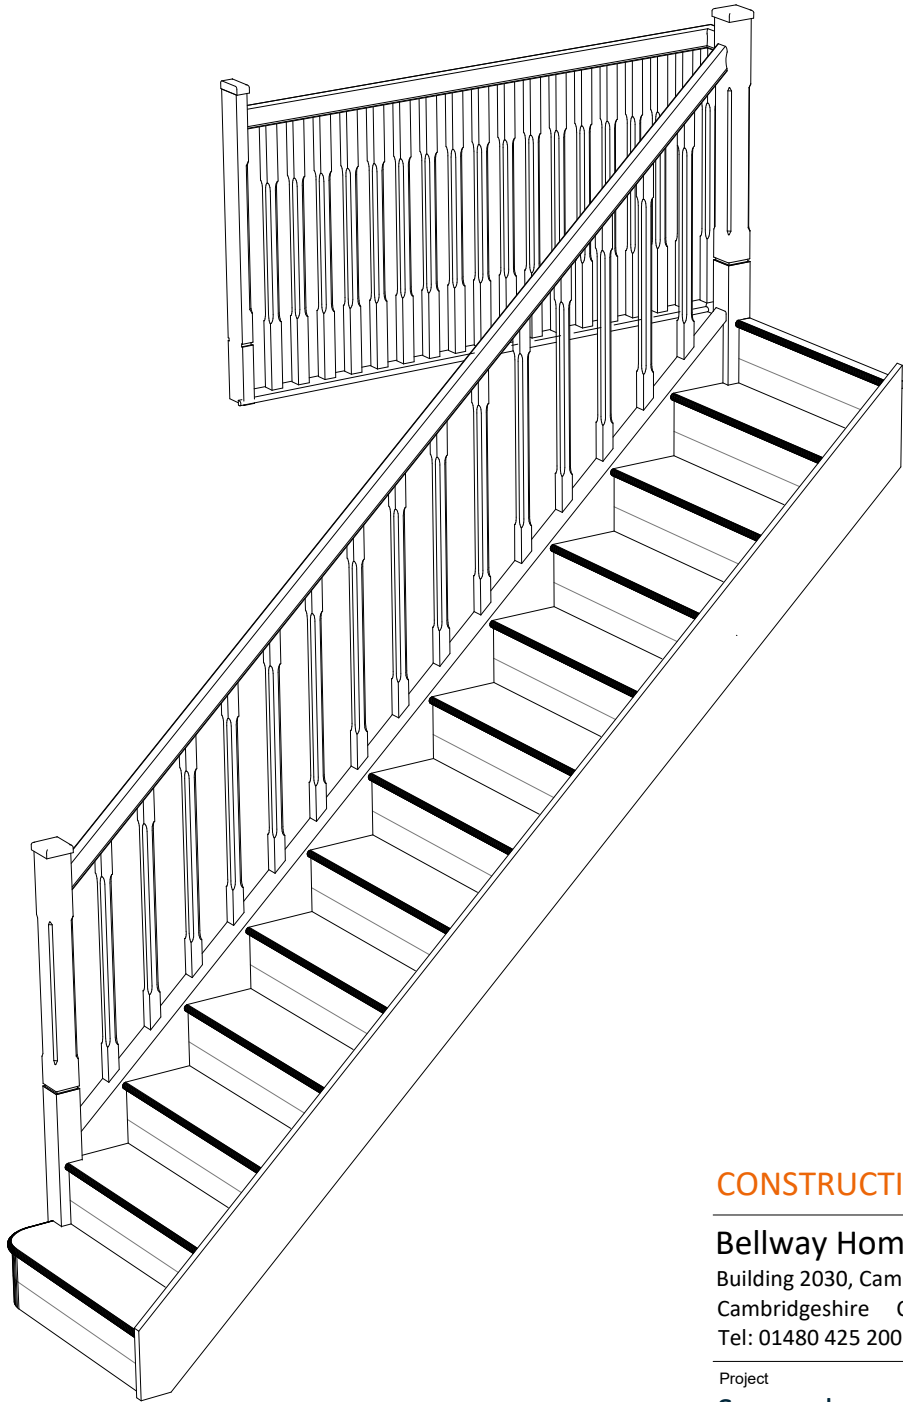

3 Staircase - 3D View



Bellway Homes (Eastern Counties)
Building 2030, Cambourne Business Park,
Cambridgeshire CB23 6DW
Tel: 01480 425 200

Project
Somersham
St Ives Road
Working Drawings

Drawing Title
The Draftsman-Life **DML-3B-2S-0**
934 ft² | 3b Semi/Mid | All Variants
Staircase Details

Drawing Created By Group	First Issue Date April '25	Scale(s) As indicated
Project No BI01	Drg Status Construction	Revision C1
Drawing No. BI01/934DML/50/0/01		

Plots 32, 34, 36, 46 (AS) & 33, 35, 47 (OPP)

Do not scale - if in doubt, ask