


| Revision Schedule |          |                    |        |
|-------------------|----------|--------------------|--------|
| Rev               | Date     | Description        | Drn By |
| C1                | 28.11.25 | Construction Issue | -      |

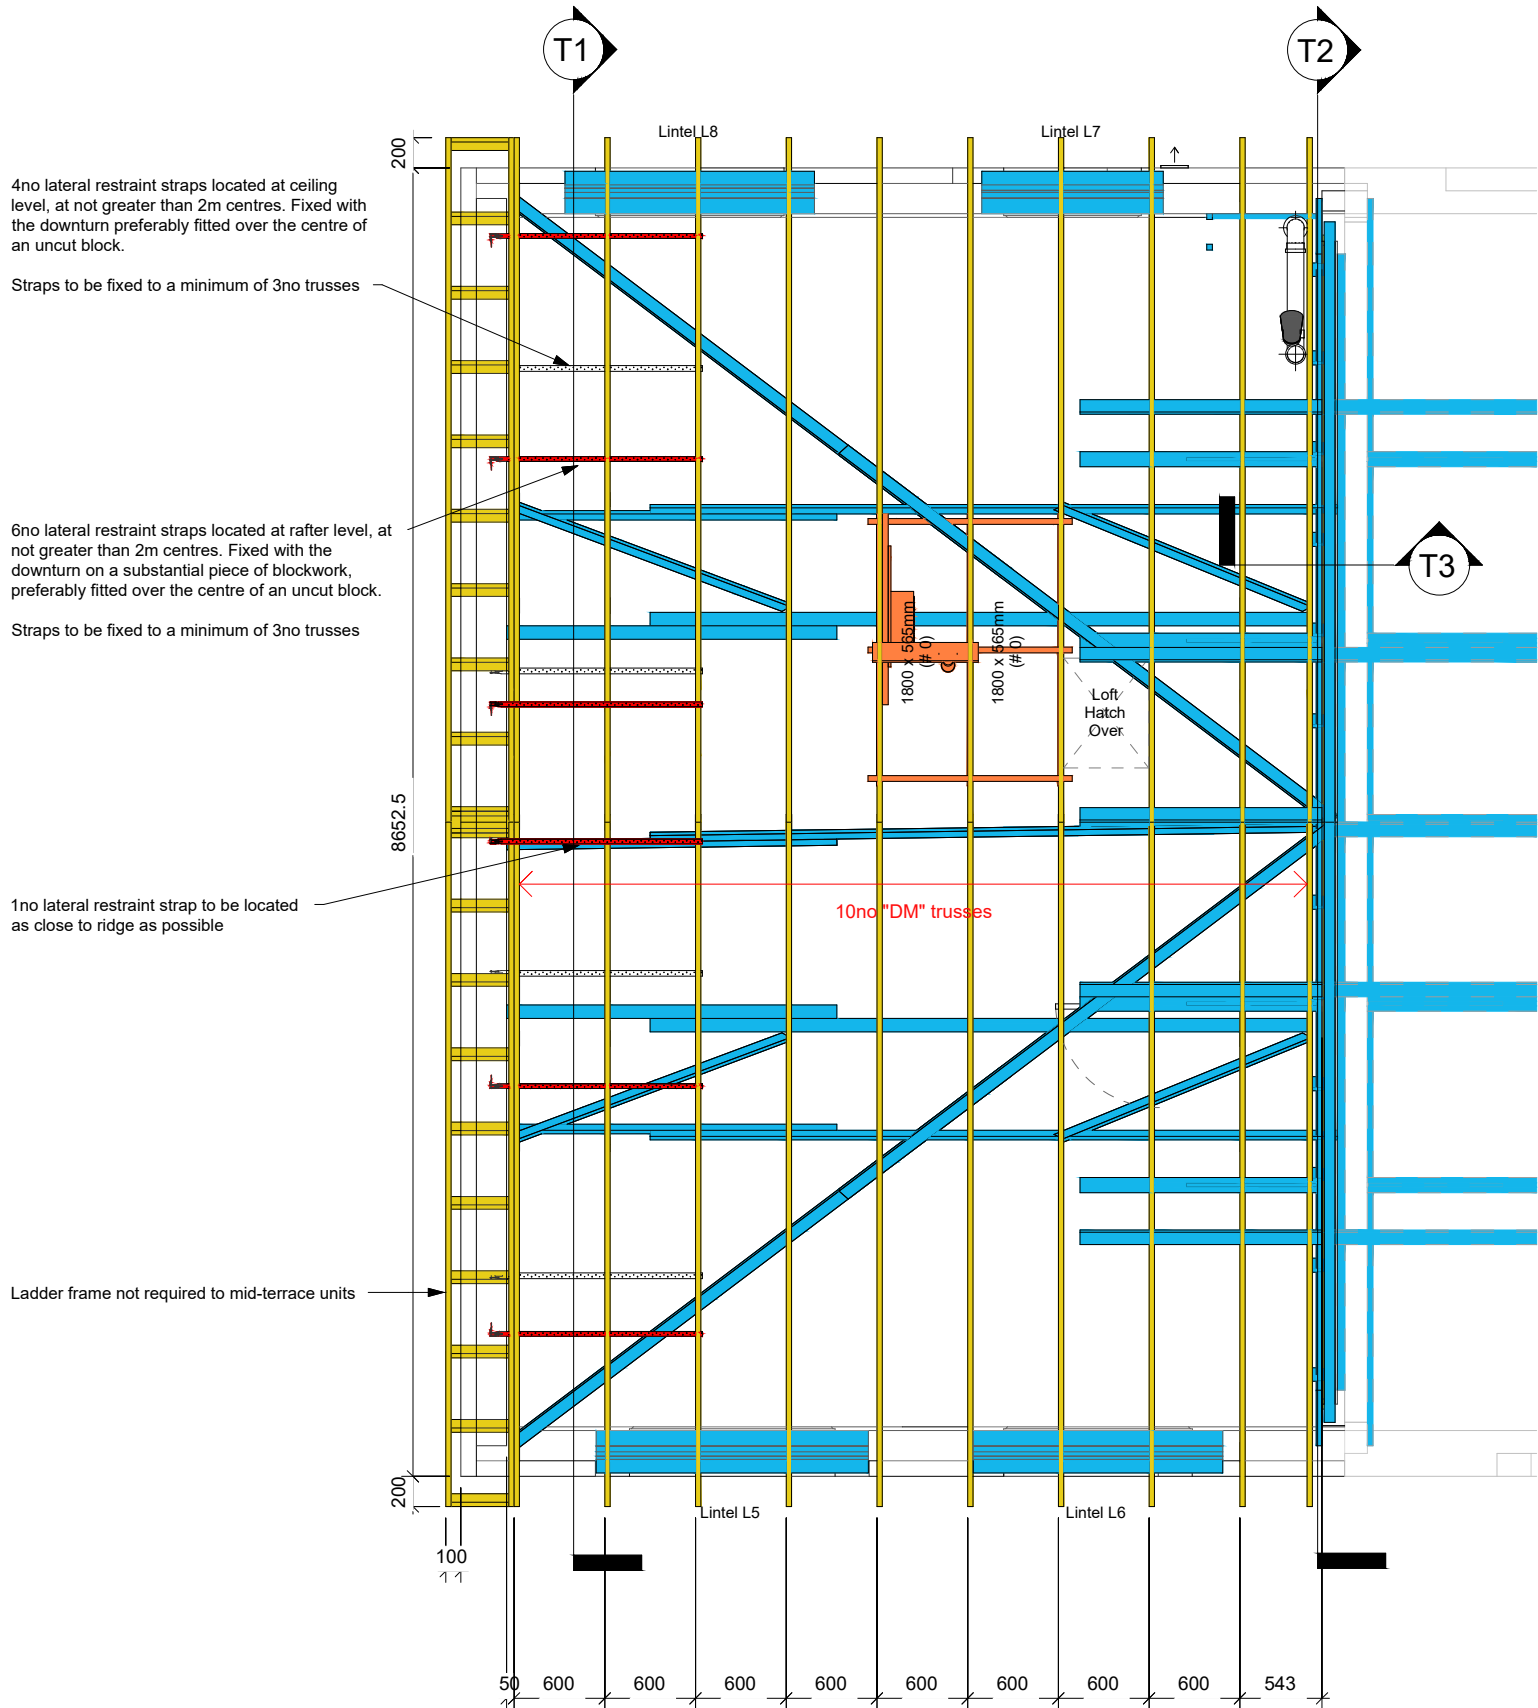

1 Roof Trusses (Boxed Eaves) 1-50  
1 : 50

|                             |                               |                     |
|-----------------------------|-------------------------------|---------------------|
| Drawing Created By<br>Group | First Issue Date<br>April '25 | Scale(s)<br>1 : 50  |
| Project No<br>BI01          | Drg Status<br>Construction    | Revision<br>C1      |
| Drawing No.                 |                               | BI01/934DML/60/0/01 |