



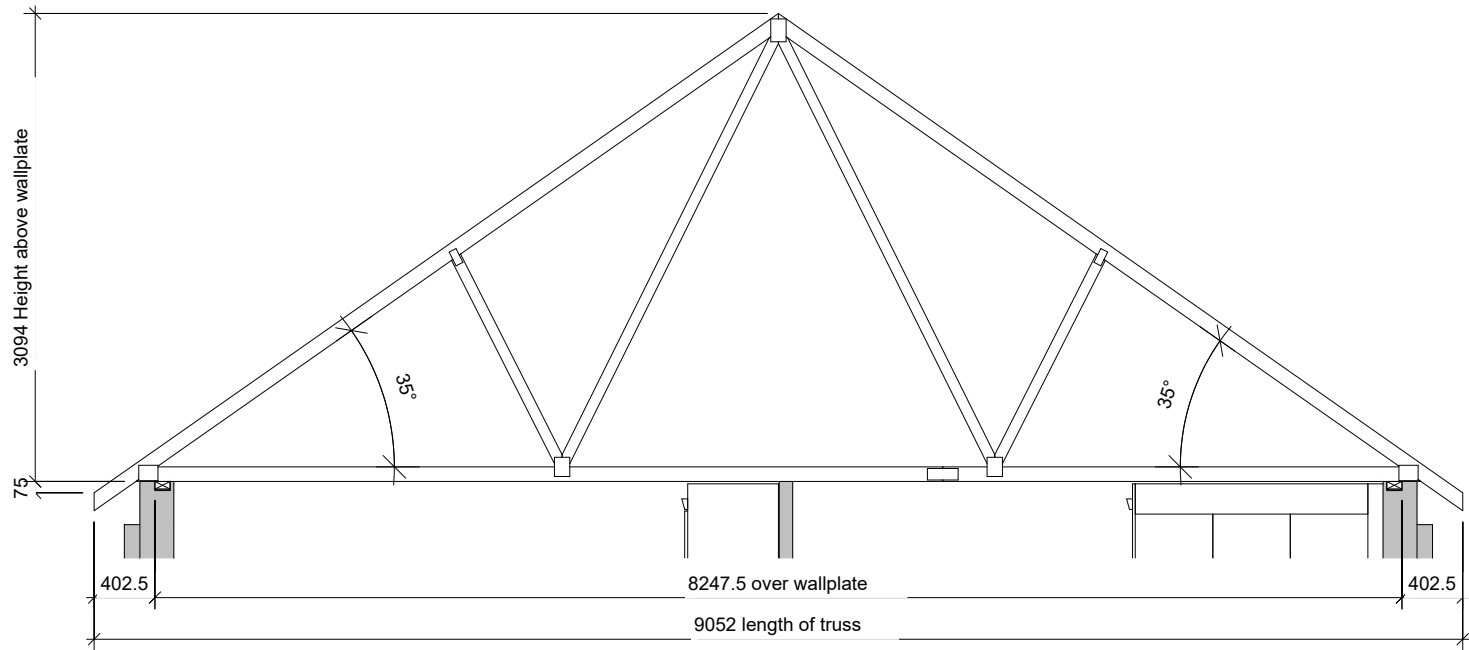


C1 Truss "DM" - 10no reqd (1ply, 54kg)
1 : 50

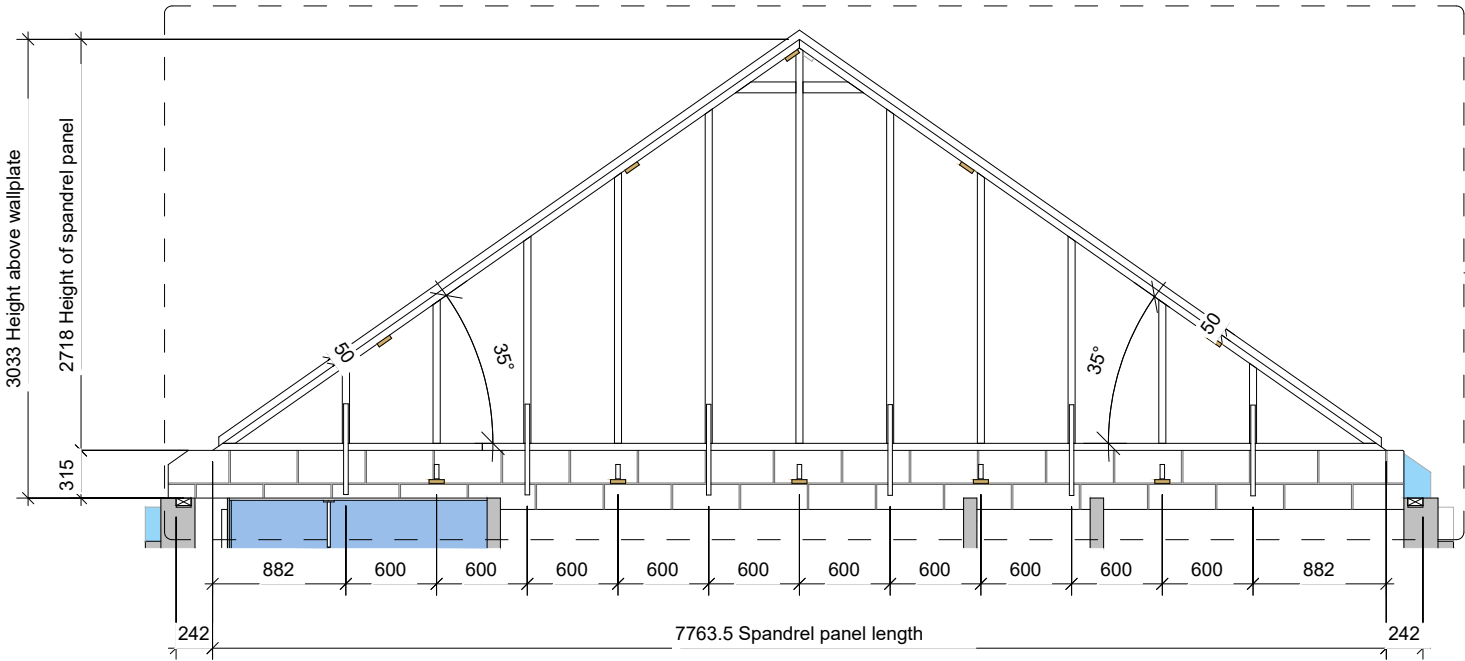

T2 Spandrel Panel - 1no reqd (1ply, 470kg)
1 : 50

Standard Detail
Party Wall
Spandrel Panel
A/SD/S80/A/12-15

Revision Schedule			
Rev	Date	Description	Drn By
C1	28.11.25	Construction Issue	-

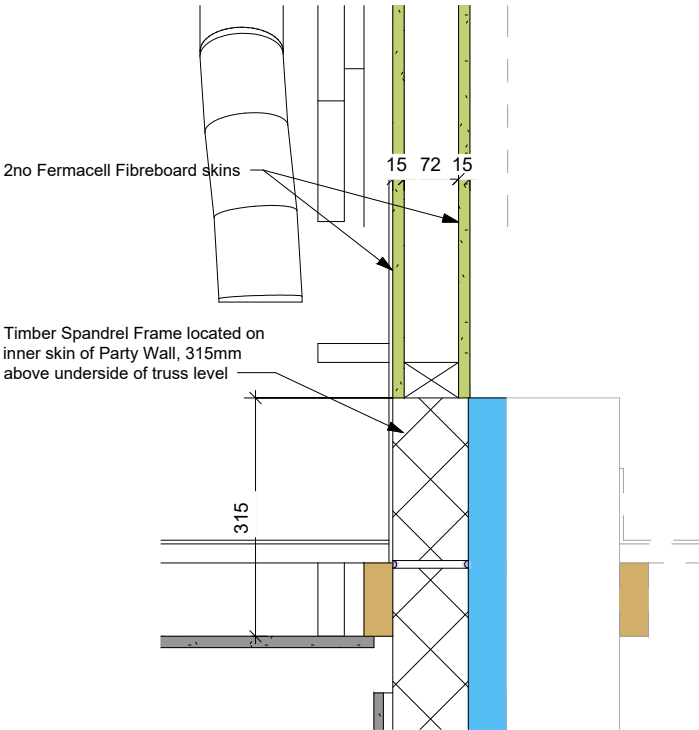

T3 Spandrel Panel - Section Through Base
1 : 10

CONSTRUCTION **Bellway**
www.bellway.co.uk

Bellway Homes (Eastern Counties)
Building 2030, Cambourne Business Park,
Cambridgeshire CB23 6DW
Tel: 01480 425 200

Project
Somersham
St Ives Road
Working Drawings

Drawing Title
The Draftsman-Life **DML-3B-2S-0**
934 ft² | 3b Semi/Mid | All Variants
Roof Trusses

Drawing Created By Group	First Issue Date April '25	Scale(s) As indicated
Project No BI01	Drg Status Construction	Revision C1
Drawing No.		BI01/934DML/60/0/02

Plots 32, 34, 36, 46 (AS) & 33, 35, 47 (OPP)

Do not scale - if in doubt, ask