



Revision Schedule			
Rev	Date	Description	Drn By
C1	28.11.25	Construction Issue	-

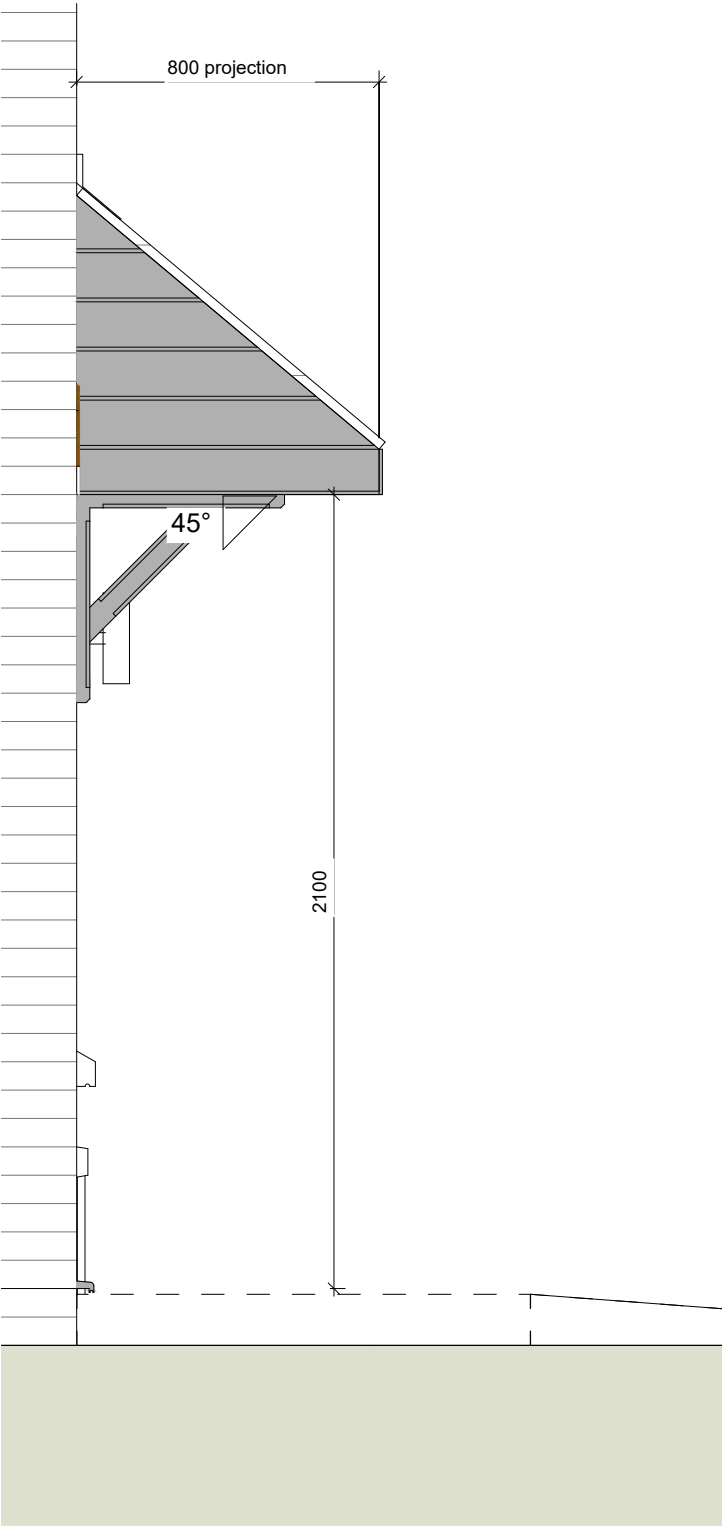

1 Gable Elevation
1 : 20

Elevations for dimensional purposes only.
Read with A/SD/S100/A/01 for canopy
fixing and construction details.

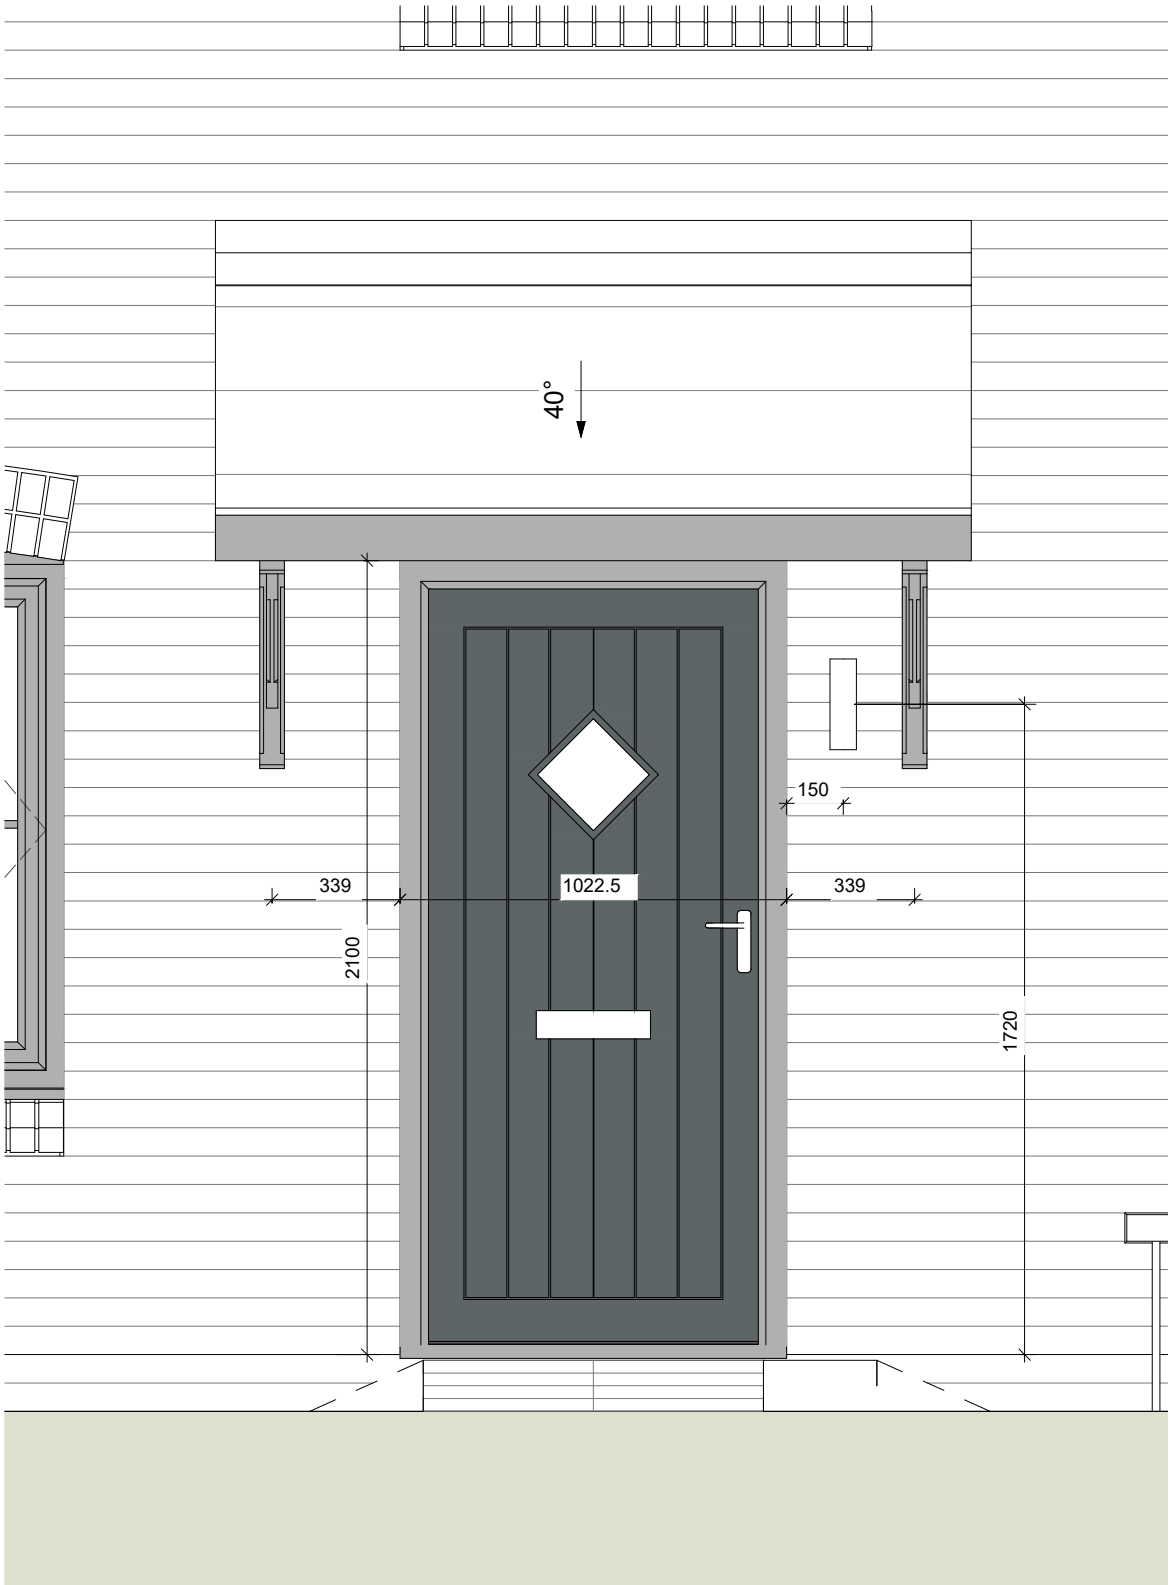

2 Front Elevation
1 : 20

Plots 32, 34, 36, 46 (AS) & 33, 35, 47 (OPP)

CONSTRUCTION

Bellway
www.bellway.co.uk

Bellway Homes (Eastern Counties)
Building 2030, Cambourne Business Park,
Cambridgeshire CB23 6DW
Tel: 01480 425 200

Project
Somersham
St Ives Road
Working Drawings

Drawing Title

The Draftsman-Life

DML-3B-2S-CB

934 ft² | 3b Semi/Mid | Country Brick
Entrance Canopy

Drawing Created By	First Issue Date	Scale(s)
Group	April '25	1 : 20
Project No	Drg Status	Revision
BI01	Construction	C1
Drawing No.	BI01/934DML/65/CB/01	

Do not scale - if in doubt, ask