




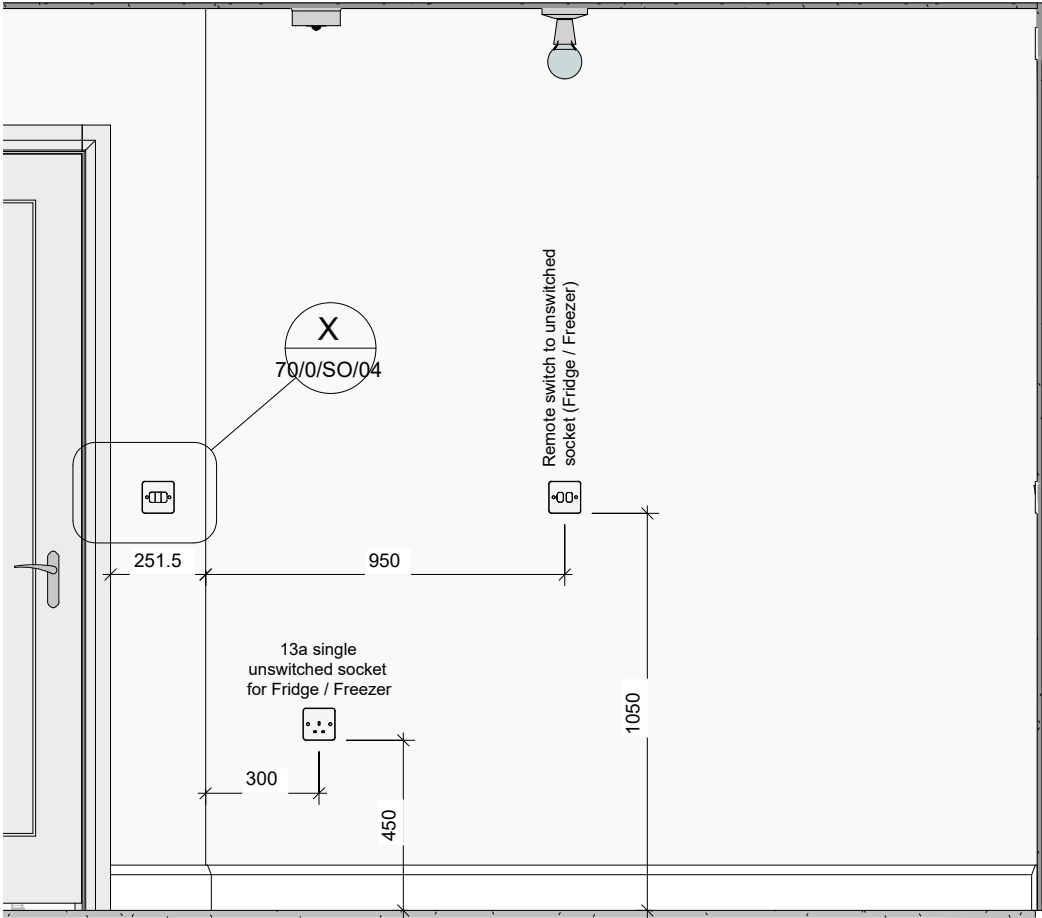


A Kitchen Electrics - View A (Rented Spec)
1 : 20

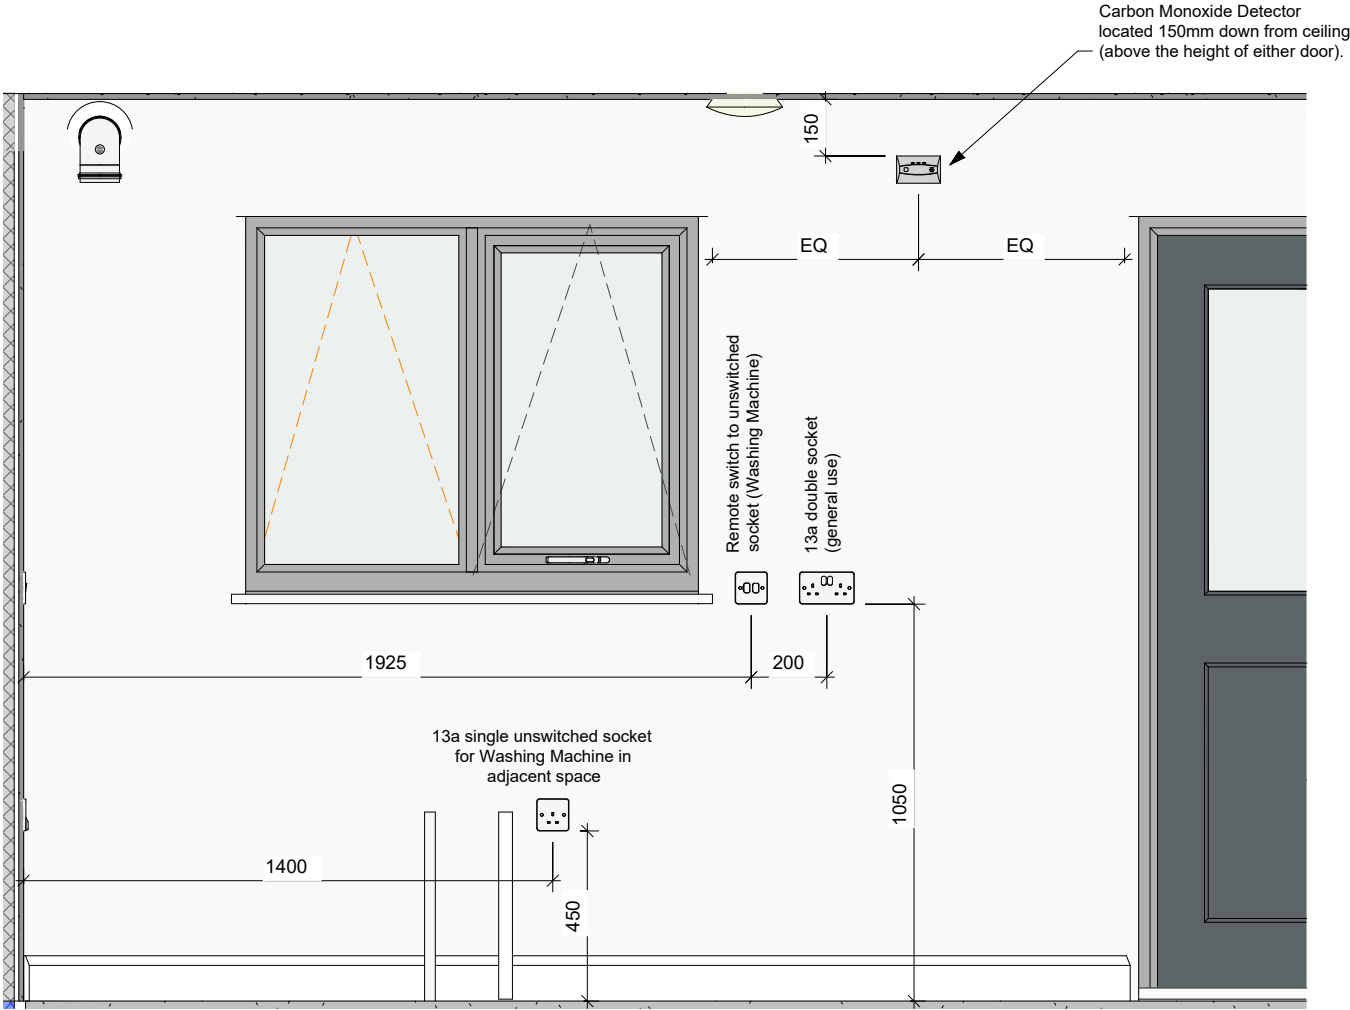

C Kitchen Electrics - View C (Rented Spec)
1 : 20

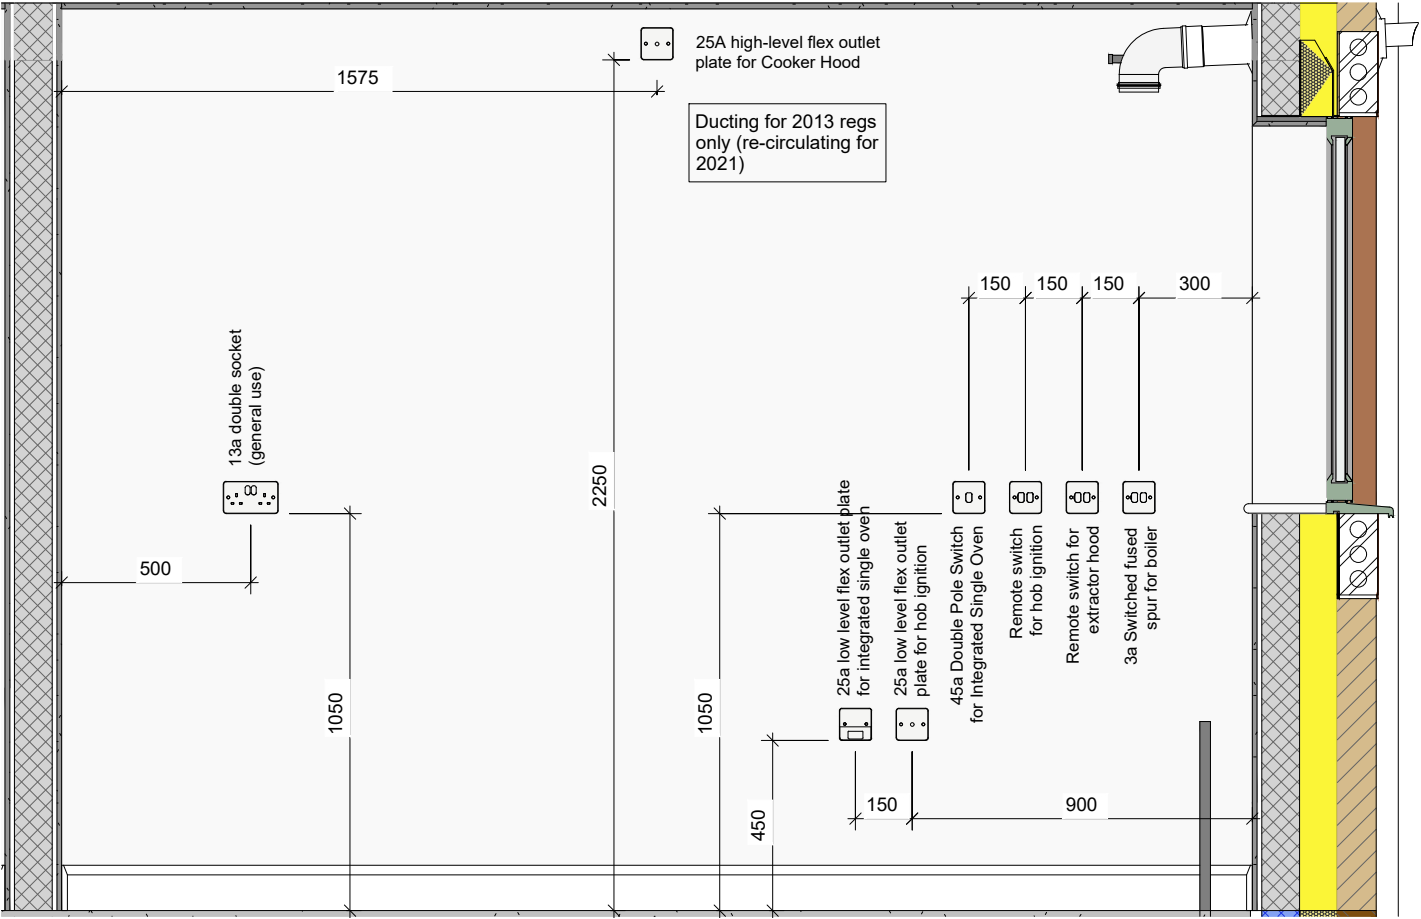

B Kitchen Electrics - View B (Rented Spec)
1 : 20

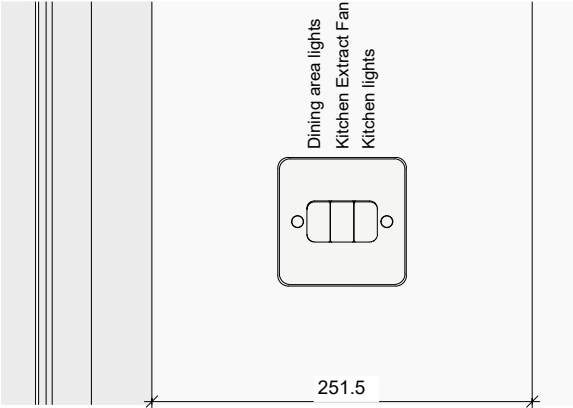

X Lightswitch
1 : 5

Revision Schedule			
Rev	Date	Description	Drn By
T1	18.08.25	Tender Issue	-

CONSTRUCTION **Bellway**
www.bellway.co.uk

Bellway Homes (Eastern Counties)
Building 2030, Cambourne Business Park,
Cambridgeshire CB23 6DW
Tel: 01480 425 200

Project
Somersham
St Ives Road
Working Drawings

Drawing Title
The Draftsman-Life **DML-3B-2S-0**
934 ft² | 3b Semi/Mid | All Variants
Kitchen Electrics GA

Drawing Created By Group	First Issue Date April '25	Scale(s) As indicated
Project No BI01	Drng Status Construction	Revision T1
Drawing No. BI01/934DML/70/0/SO/04		

Plots 32, 34, 36, 46 (AS) & 33, 35, 47 (OPP)

Do not scale - if in doubt, ask