


Revision Schedule			
Rev	Date	Description	Drn By
C1	28.11.25	Construction Issue	-

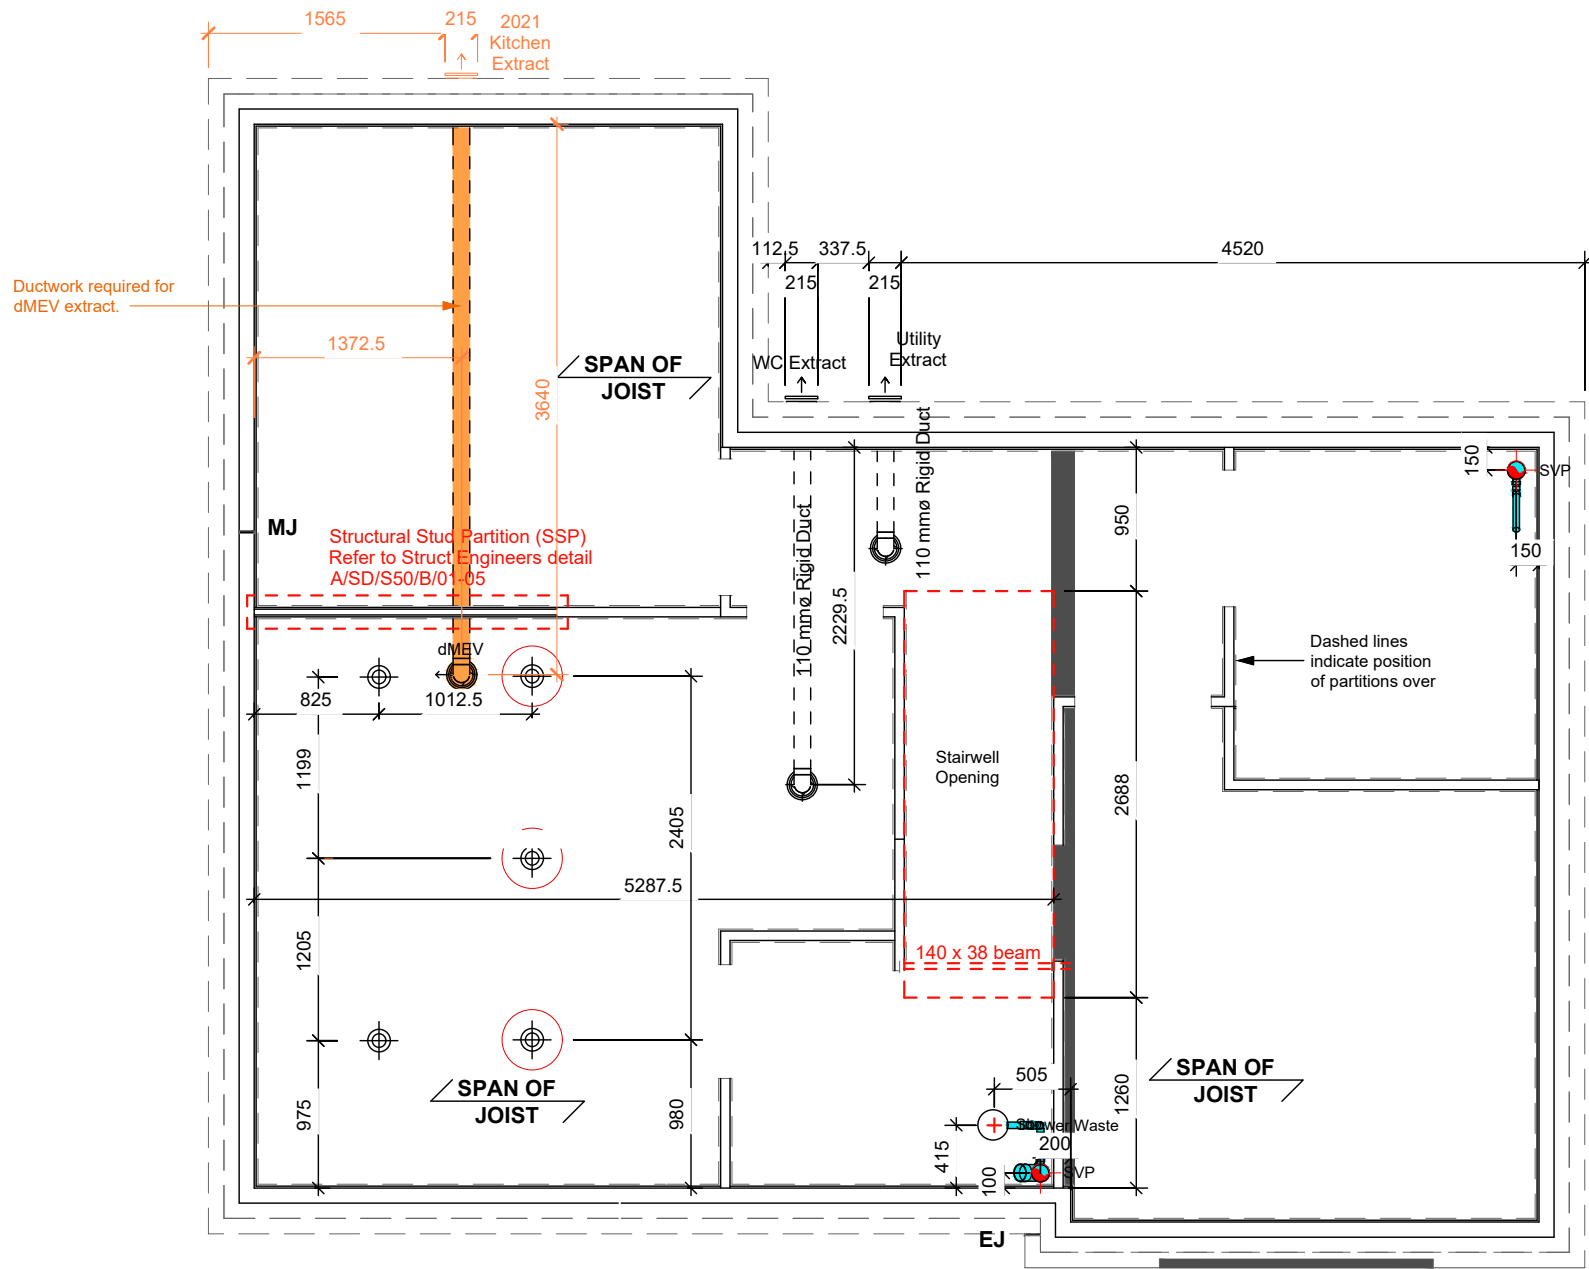

1 First Floor Joist Setting Out
1 : 50

CONSTRUCTION

Bellway
www.bellway.co.uk

Bellway Homes (Eastern Counties)
Building 2030, Cambourne Business Park,
Cambridgeshire CB23 6DW
Tel: 01480 425 200

Project
Somersham
St Ives Road
Working Drawings

Drawing Title
The Fuller Life **FRL-3B-2S-0**

1053 ft² | 3b Det (Corner Turner) | All Variants
First Floor Joist Setting Out

Drawing Created By Group	First Issue Date April '25	Scale(s) 1 : 50
Project No BI01	Drg Status Construction	Revision C1
Drawing No. BI01/1053FRL/40/0/01		