


Staircraft Drawing Ref:



House Type Name: FRAMER option 2
Handing*: RHWS
Finished Floor Level (FFL) 2662
Revision: C

Revision Schedule			
Rev	Date	Description	Drn By
C1	28.11.25	Construction Issue	-

*Handing of staircase to be confirmed at point of call off.

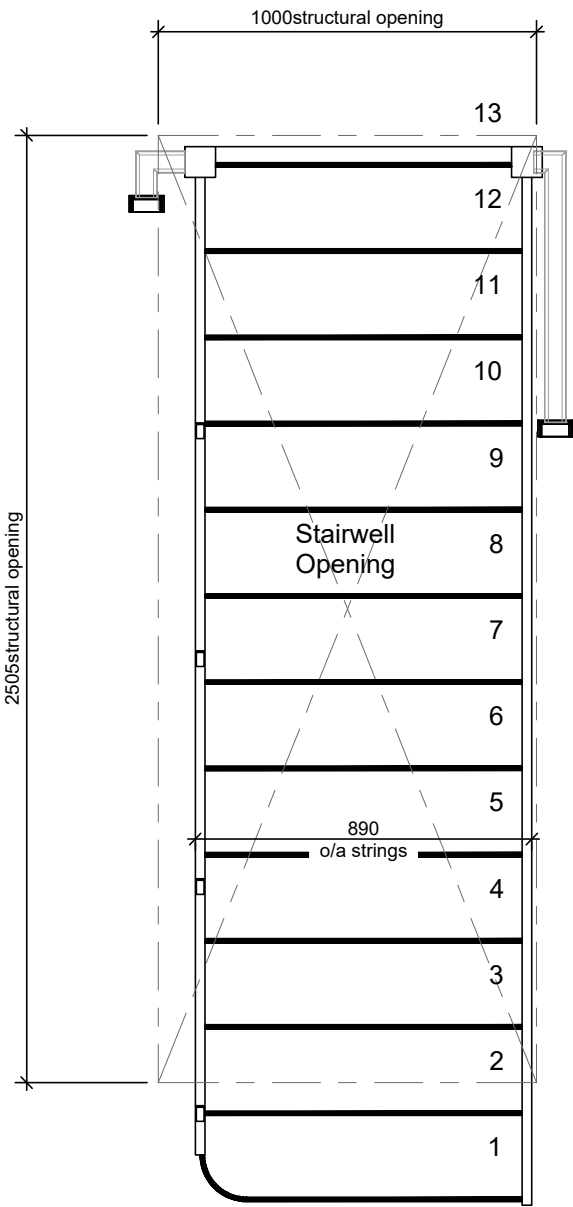

13no risers @ 204.77mm
12no goings @ 228mm
Total rise 2662mm

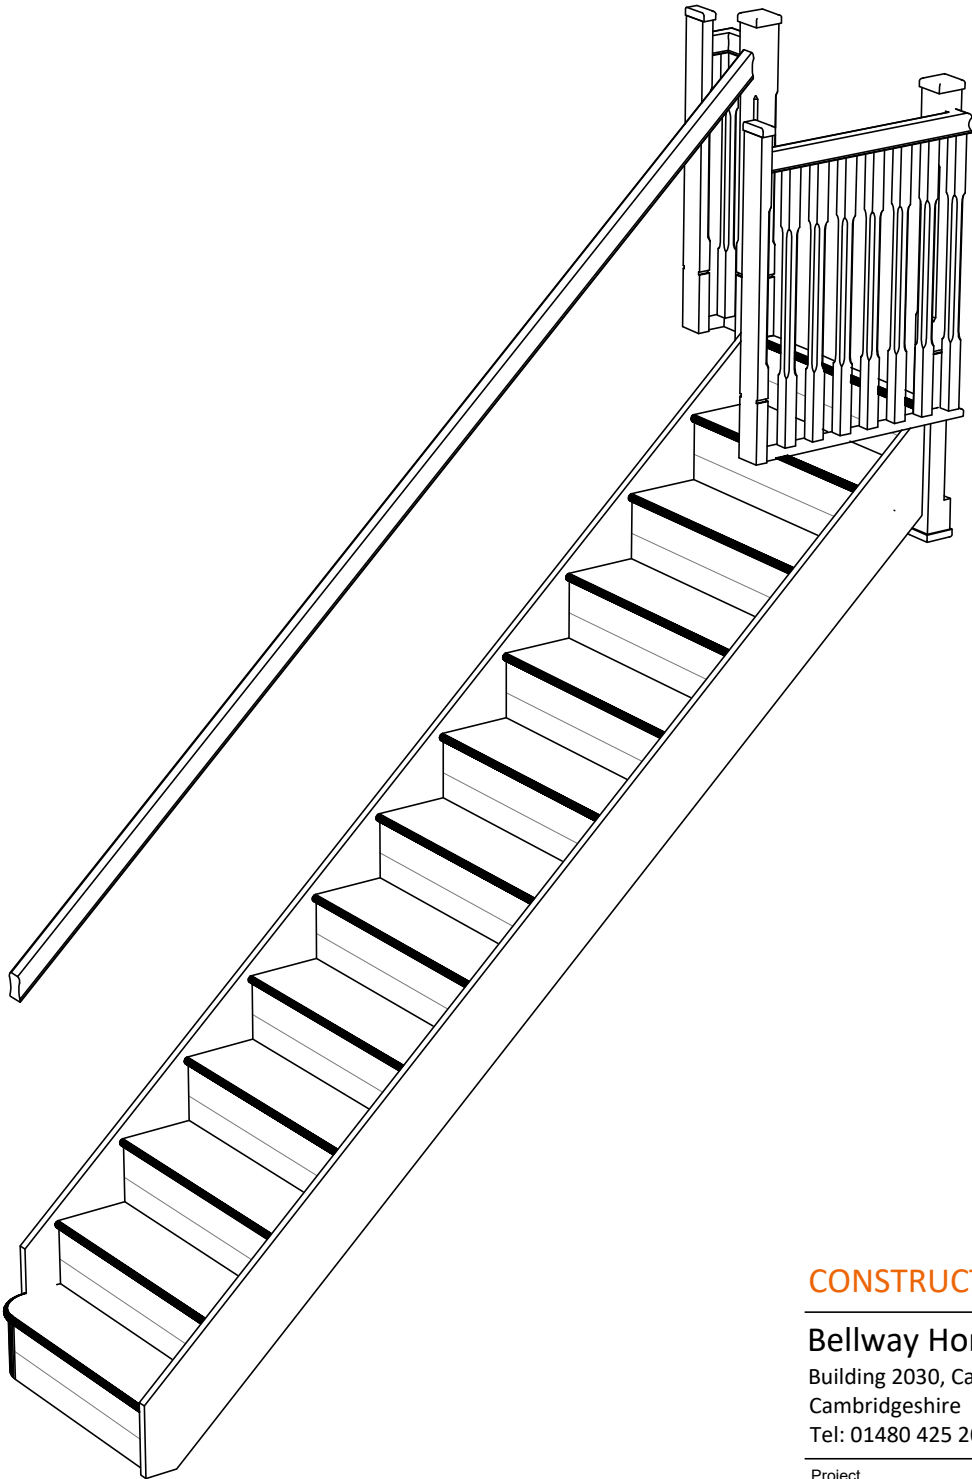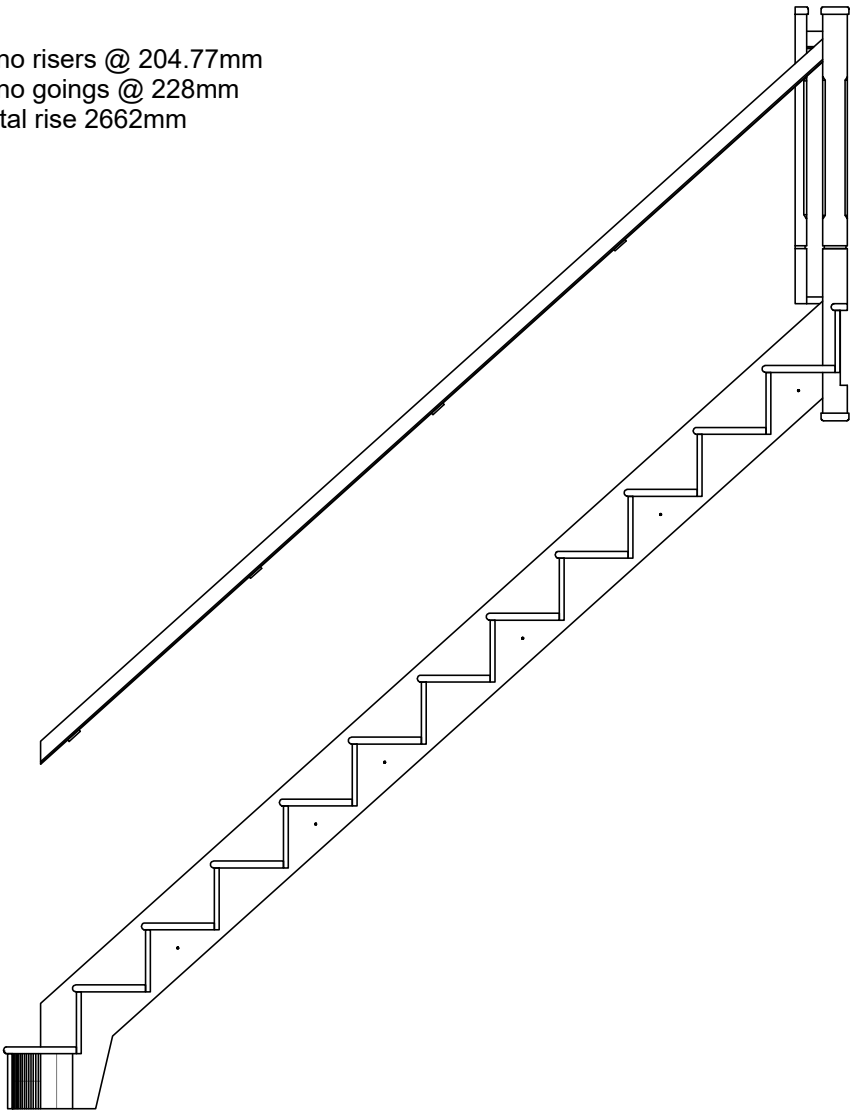

1 Staircase - Plan
1 : 20

2 Stair - Elevation
1 : 25

3 Staircase - 3D View



Bellway Homes (Eastern Counties)

Building 2030, Cambourne Business Park,
Cambridgeshire CB23 6DW
Tel: 01480 425 200

Project

Somersham

St Ives Road

Working Drawings

Drawing Title

The Fuller Life

FRL-3B-2S-0

1053 ft² | 3b Det (Corner Turner) | All Variants

Staircase Details

Drawing Created By Group	First Issue Date April '25	Scale(s) As indicated
Project No BI01	Drg Status Construction	Revision C1
Drawing No. BI01/1053FRL/50/0/01		

Plots 20, 23 (OPP)

Do not scale - if in doubt, ask