


Revision Schedule			
Rev	Date	Description	Drm By
C1	28.11.25	Construction Issue	-

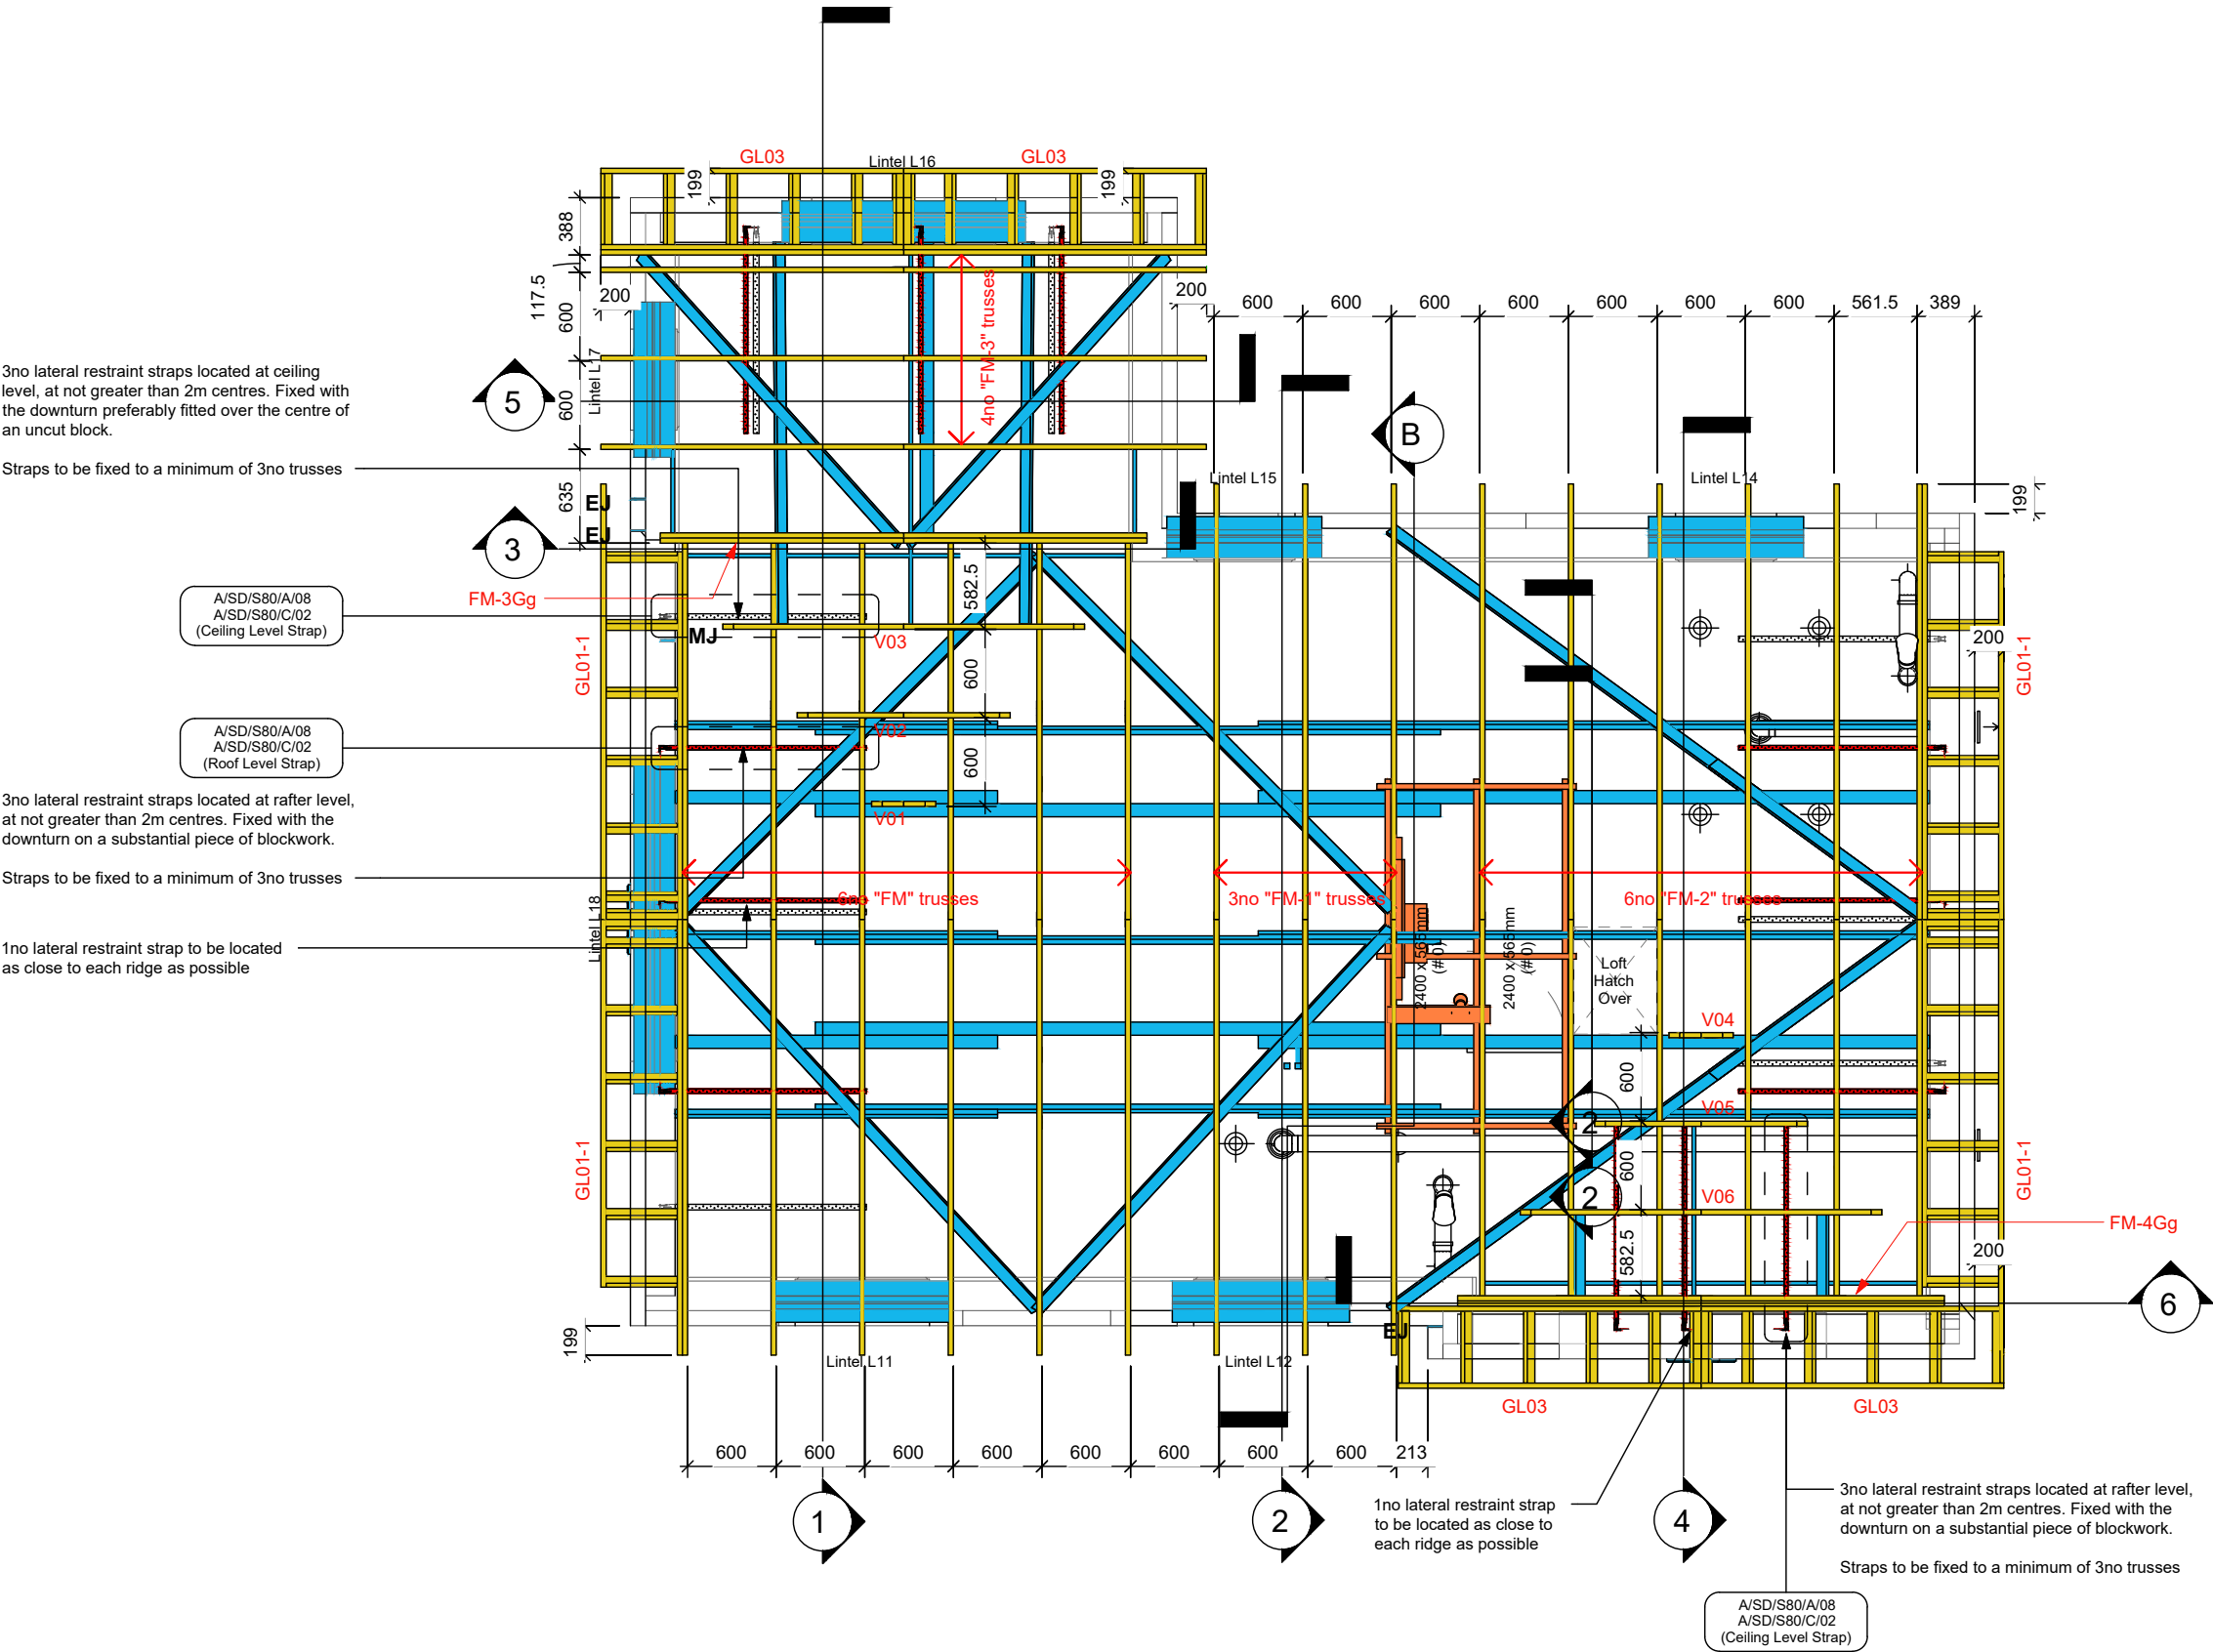

1 Roof Trusses (Boxed Eaves) 1-50
1 : 50

Plots 20, 23 (OPP)

CONSTRUCTION


www.bellway.co.uk

Bellway Homes (Eastern Counties)
Building 2030, Cambourne Business Park,
Cambridgeshire CB23 6DW
Tel: 01480 425 200

Project
Somersham
St Ives Road
Working Drawings

Drawing Title
The Fuller Life
1053 ft² | 3b Det (Corner Turner) | All Variants
Roof Layout

FRL-3B-2S-0

Drawing Created By Group	First Issue Date April '25	Scale(s) 1 : 50
Project No BI01	Drg Status Construction	Revision C1
Drawing No. BI01/1053FRL/60/0/01		

Do not scale - if in doubt, ask