


Revision Schedule			
Rev	Date	Description	Drm By
C1	28.11.25	Construction Issue	-



1 Front Elevation
1 : 20

Elevations for dimensional purposes only.
Read with A/SD/S100/A/01 for canopy
fixing and construction details.

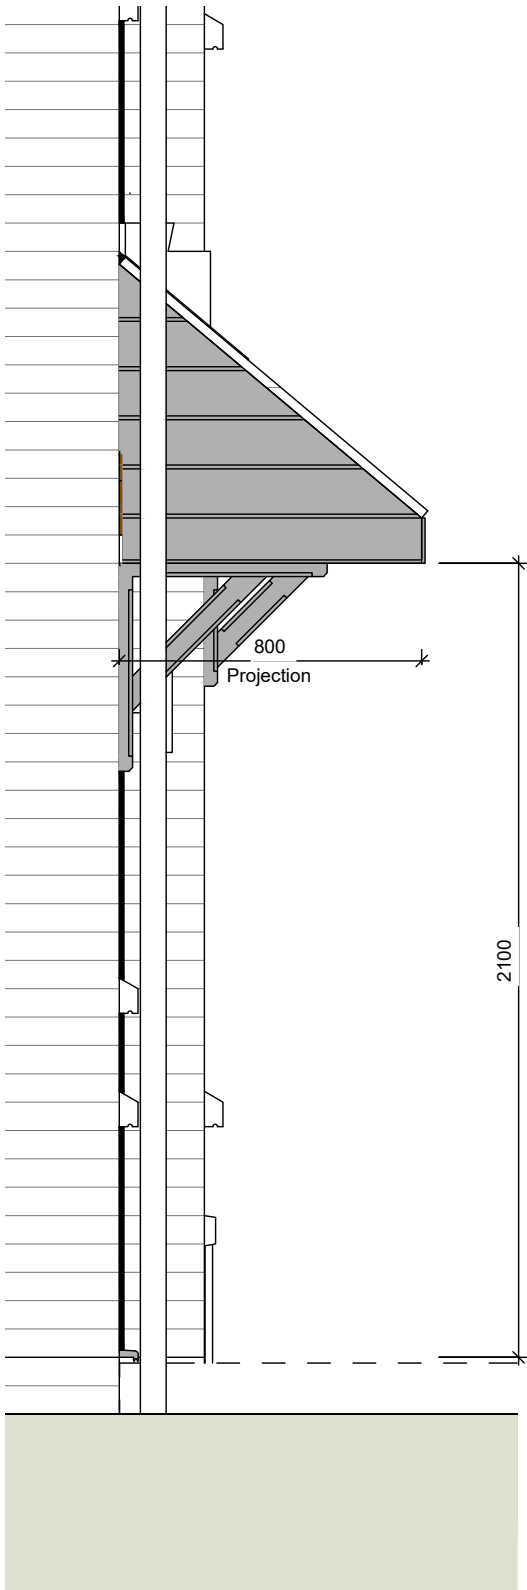

2 Gable Elevation
1 : 20

CONSTRUCTION

Bellway
www.bellway.co.uk

Bellway Homes (Eastern Counties)
Building 2030, Cambourne Business Park,
Cambridgeshire CB23 6DW
Tel: 01480 425 200

Project
Somersham
St Ives Road
Working Drawings

Drawing Title
The Fuller Life **FRL-3B-2S-CB**
1053 ft² | 3b Det (Corner Turner) | Country Brick
Entrance Canopy

Drawing Created By Group	First Issue Date April '25	Scale(s) 1 : 20
Project No BI01	Drg Status Construction	Revision C1
Drawing No. BI01/1053FRL/65/CB/01		

Plots 20, 23 (OPP)

Do not scale - if in doubt, ask