

Revision Schedule			
Rev	Date	Description	Drn By
C1	28.11.25	Construction Issue	-

Kitchen Electrical Legend

	Pendant light fitting		Light switch - Intermediate ⁽¹⁾
	Batten holder fitting		AC isolator switch for solar panels
	IP65 recessed spotlight		Fan isolator switch (installed to centreline of door, 2150mm above FFL to underside of switch)
	IP65 recessed spotlight to be supplied with Fire Hood / Shroud		13A Single Un-switched fused spur connection
	External Wall mounted light fitting		Double pole switched fused spur connection (13A 3A)
	Multi (8g)		Remote switches to unswitched sockets ⁽²⁾ Single Multi (8no max)
	CM		Wall mounted CO detector (installed @ 2000mm above FFL)
	Light switch 1 way ⁽¹⁾ 1 2 3 gang		25A Flex outlet plate high level ⁽²⁾ low level ⁽³⁾
	Light switch 2 way ⁽¹⁾ 1 2 3 gang		Cooker outlet plate ⁽³⁾ with 6mm Ø cable to 45A double pole switch
	Single unswitched socket (13A) high level ⁽²⁾ low level ⁽³⁾		45A double pole switch ⁽²⁾ with 6mm Ø cable to distribution board
	Single switched socket (13A) high level ⁽²⁾ low level ⁽³⁾		Consumer unit (underside of unit installed 1350mm above FFL)
	Double switched socket (13A) high level ⁽²⁾ low level ⁽³⁾		Room thermostat ⁽¹⁾ Zone 1 Zone 2
	Ceiling mounted detector Smoke Heat		

General Note - sockets located 400mm from internal corners of rooms to centrelines of sockets, unless otherwise stated

2021 Regulations
All radiators sizes illustrated here are to satisfy 2021 regulations.

All Radiators and Extract Fan locations shown in orange are to be provided for 2021 Regulation properties only.

Refer to 80 series drawings for Radiator schedules and sizes, and refer to 90/0/02 drawing for Extract Fan schedules for both 2013 and 2021 regulations.

CONSTRUCTION

Bellway
www.bellway.co.uk

Bellway Homes (Eastern Counties)

Building 2030, Cambourne Business Park,
Cambridgeshire CB23 6DW
Tel: 01480 425 200


Project
Somersham
St Ives Road
Working Drawings

Drawing Title
The Fuller Life
FRL-3B-2S-0

1053 ft² | 3b Det (Corner Turner) | All Variants
Kitchen Layout - Upgrade
Plots 20, 23 (OPP)

Drawing Created By	First Issue Date	Scale(s)
Group	April '25	As indicated
Project No	Drg Status	Revision
BI01	Construction	C1

Drawing No. **BI01/1053FRL/70/0/U/01**

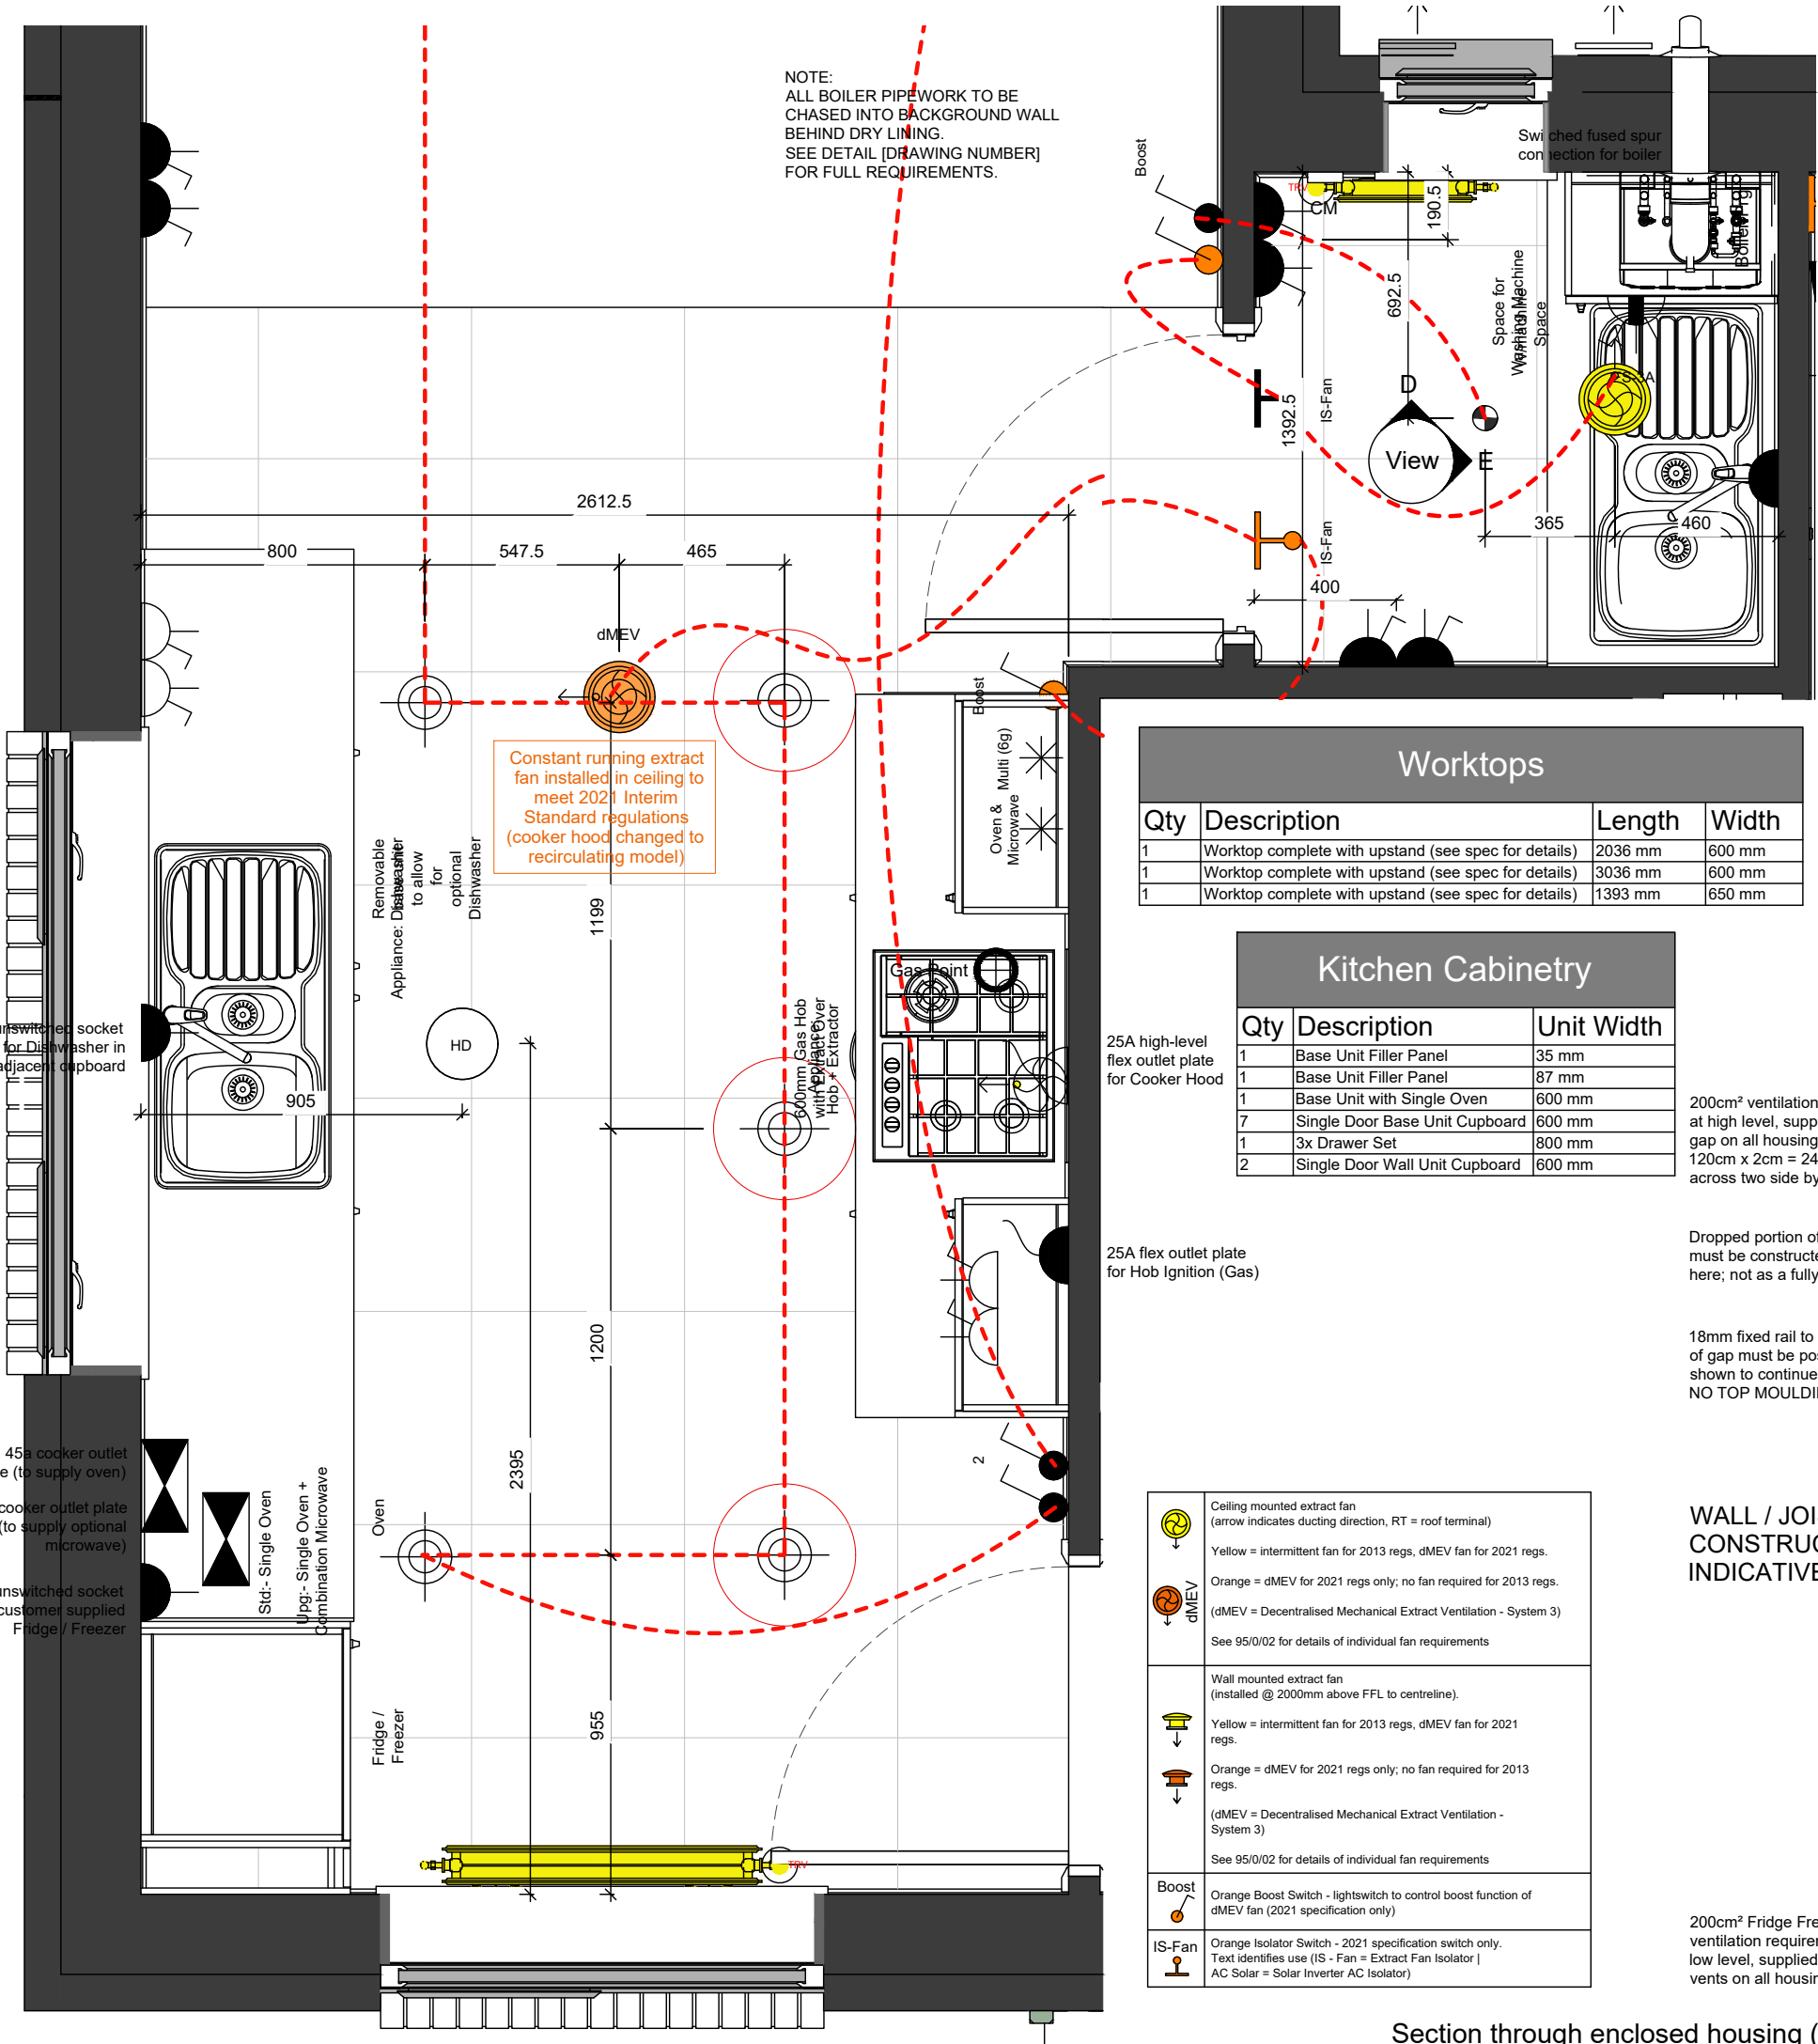

Worktops			
Qty	Description	Length	Width
1	Worktop complete with upstand (see spec for details)	2036 mm	600 mm
1	Worktop complete with upstand (see spec for details)	3036 mm	600 mm
1	Worktop complete with upstand (see spec for details)	1393 mm	650 mm

Kitchen Cabinetry		
Qty	Description	Unit Width
1	Base Unit Filler Panel	35 mm
1	Base Unit Filler Panel	87 mm
1	Base Unit with Single Oven	600 mm
7	Single Door Base Unit Cupboard	600 mm
1	3x Drawer Set	800 mm
2	Single Door Wall Unit Cupboard	600 mm

	Ceiling mounted extract fan (arrow indicates ducting direction, RT = roof terminal) Yellow = intermittent fan for 2013 regs, dMEV fan for 2021 regs. Orange = dMEV for 2021 regs only; no fan required for 2013 regs. (dMEV = Decentralised Mechanical Extract Ventilation - System 3) See 95/0/02 for details of individual fan requirements
	Wall mounted extract fan (installed @ 2000mm above FFL to centreline). Yellow = intermittent fan for 2013 regs, dMEV fan for 2021 regs. Orange = dMEV for 2021 regs only; no fan required for 2013 regs. (dMEV = Decentralised Mechanical Extract Ventilation - System 3) See 95/0/02 for details of individual fan requirements
	Orange Boost Switch - lightswitch to control boost function of dMEV fan (2021 specification only)
	Orange Isolator Switch - 2021 specification switch only. Text identifies use (IS - Fan = Extract Fan Isolator AC Solar = Solar Inverter AC Isolator)


WALL / JOIST CONSTRUCTION IS INDICATIVE ONLY

200cm² Fridge Freezer ventilation requirement at low level, supplied via plinth vents on all housing types

200cm² ventilation requirement at high level, supplied via air gap on all housing types; e.g., 120cm x 2cm = 240cm² across two side by side units

Dropped portion of alcove must be constructed as shown here; not as a fully closed roof

18mm fixed rail to close sight of gap must be positioned as shown to continue air flow. NO TOP MOULDING REQD

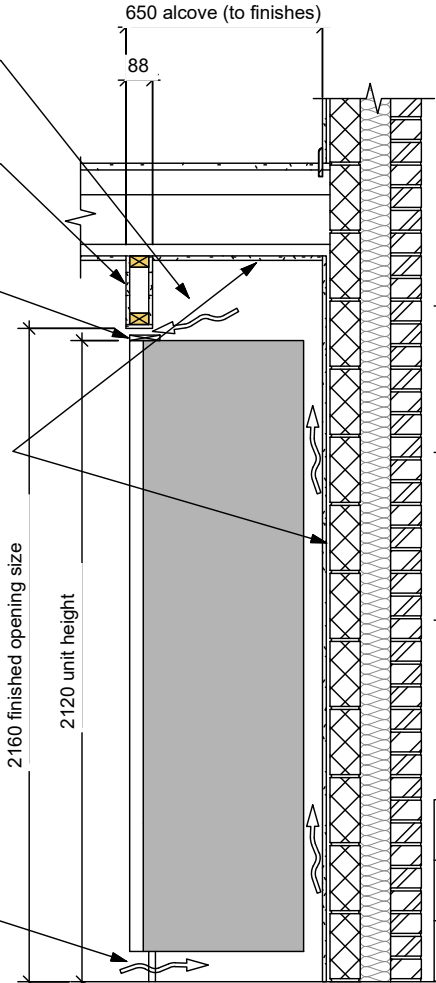

Section through enclosed housing (1 : 25)