


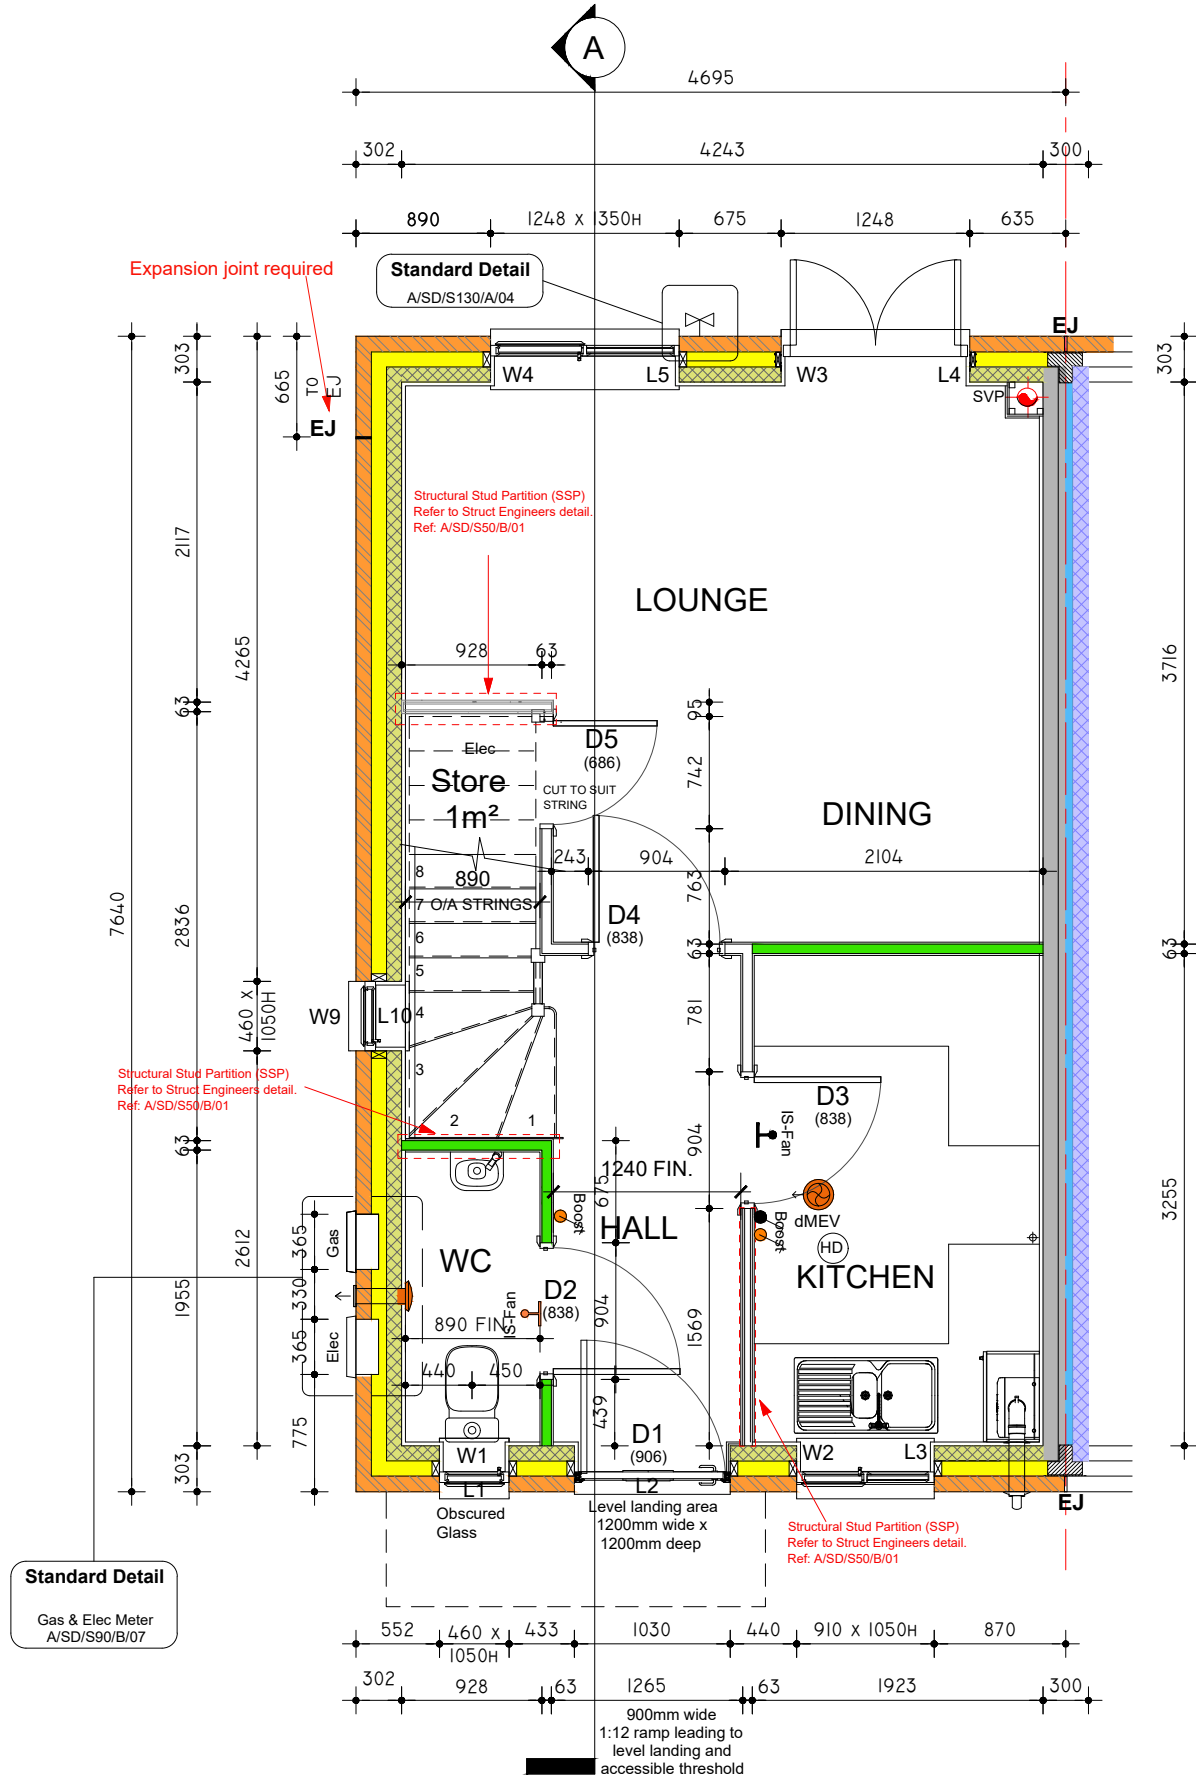

NB. FOR RWP LOCATIONS REFER TO CIVIL ENGINEER'S DRAWINGS.

- HA SPEC NOTES (Refer to site specification)
Affordable Rent -
1. Carpets to be supplied to Hall, Stairs, Lounge Dining, Bedroom, and Landing.
 2. Vinyl to WC, Kitchen & Bathroom.
 3. Full Height tiling around Bath.
 4. Thermostatic Shower Over Bath.
 5. Fixed Rail & Curtain over Bath.
 6. Turf to Rear Gardens.
 7. Fencing to Boundaries.
 8. CO Detector
 9. Door Numerals.
 10. 1.5 Stainless Steel Bowl.

Plots 26, 37, 39 (AS) & 27, 38, 40 (OPP)

Revision Schedule			
Rev	Date	Description	Drn By
C1	02.12.25	Construction Issue	C1
C1	-	C1	C1

Wall Legend (100mm Cavity)

	Standard External Insulated Cavity Wall 102.5mm brickwork 100mm cavity filled with blown mineral fibre insulation 100mm aerated concrete block (2.9N/mm²) 12.5mm gypsum board on adhesive dabs
	Mid Strength External Insulated Cavity Wall 102.5mm brickwork 100mm cavity filled with blown mineral fibre insulation 100mm mid strength aerated concrete block (3.6N/mm²) 12.5mm gypsum board on adhesive dabs
	High Strength External Insulated Cavity Wall 102.5mm brickwork 100mm cavity filled with blown mineral fibre insulation 100mm high strength aerated concrete block (7.3N/mm²) 12.5mm gypsum board on adhesive dabs
	External Uninsulated Cavity Wall (to garage, cold roof space etc.) 102.5mm brickwork 100mm air cavity 100mm aerated concrete block (2.9N/mm²)
	Party Wall 100mm mid strength aerated concrete block (3.6N/mm²) 100mm Party Wall blown glass mineral wool insulation 100mm mid strength aerated concrete block (3.6N/mm²) 12.5mm gypsum board on adhesive dabs
	Internal Blockwork Partition Between Dwelling and Garage 100mm aerated concrete block (2.9N/mm²) 70mm British Gypsum Thermaline Super Thermal Laminate Plasterboard on adhesive dabs
	Internal Blockwork Partition 12.5mm gypsum board on adhesive dabs 100mm aerated concrete block (2.9N/mm²) 12.5mm gypsum board on adhesive dabs
	Structural Stud Partition 12.5mm gypsum board 12.5mm OSB2 sheathing 63 x 38mm timber studs (studs and noggings rotated through 90°) 12.5mm gypsum board 12.5mm OSB2 sheathing
	Non-Load Bearing Stud Partition 12.5mm gypsum board 63 x 38mm timber studs 12.5mm gypsum board
	Stud Partition with Acoustic Insulation 12.5mm gypsum board 63 x 38mm timber studs, with 65mm thick Isover APR 1200 acoustic insulation packed between 12.5mm gypsum board

Note:- all blockwork drawn magenta to be 3.6N/mm²
Note:- all blockwork drawn blue to be 7.3N/mm²
Refer to current Construction Specification for further details
For Country Tile (CT), Country Weatherboard (CW) and Town Tile (TT), external skin to be replaced with 3.6N/mm² lightweight aggregate blocks to areas which are to receive alternative external treatment only.
This drawing must be read in conjunction with 25 series drawings.

TENDER

Bellway
www.bellway.co.uk

Bellway Homes Limited (Eastern Counties)
Building 2030, Cambourne Business Park
Cambourne, Cambridgeshire, CB23 6DW
Tel: 01480 425200

Project

Somersham
St Ives Road
Working Drawings

Drawing Title The Halstead		
630 ft² 1b Semi-Det Country Brick Ground Floor Plan		
Drawing Created By FDL	First Issue Date April '25	Scale(s) 1 : 50
Project No BIO1	Drg Status	Revision C1
Drawing No. BIO1 / 630HA / 10 / 01		

Do not scale - if in doubt, ask