
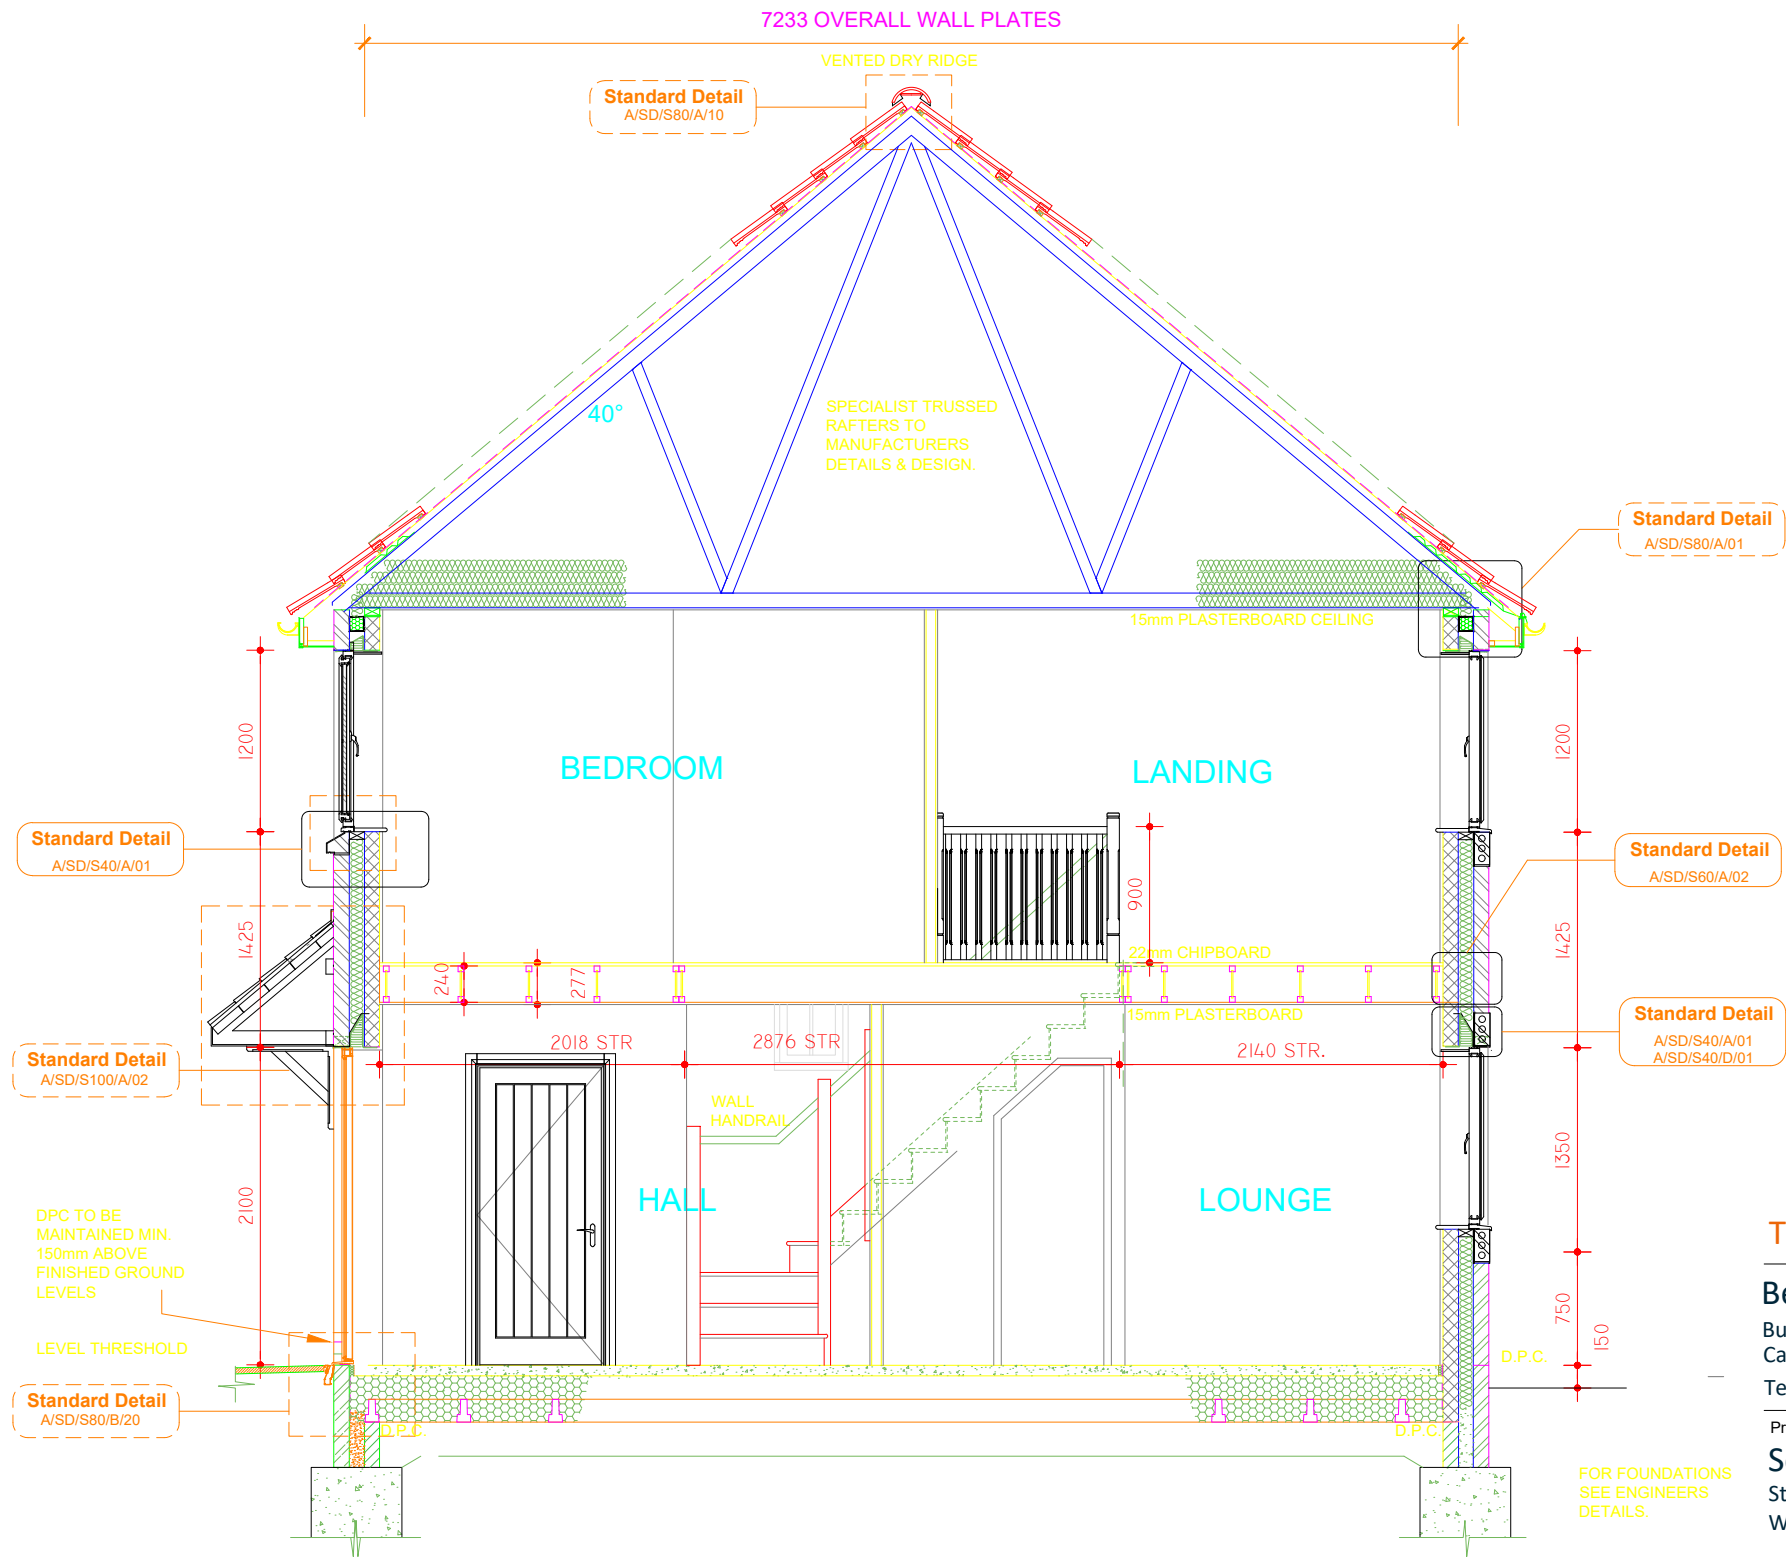


Revision Schedule			
Rev	Date	Description	Drn By
C1	02.12.25	Construction Issue	C1

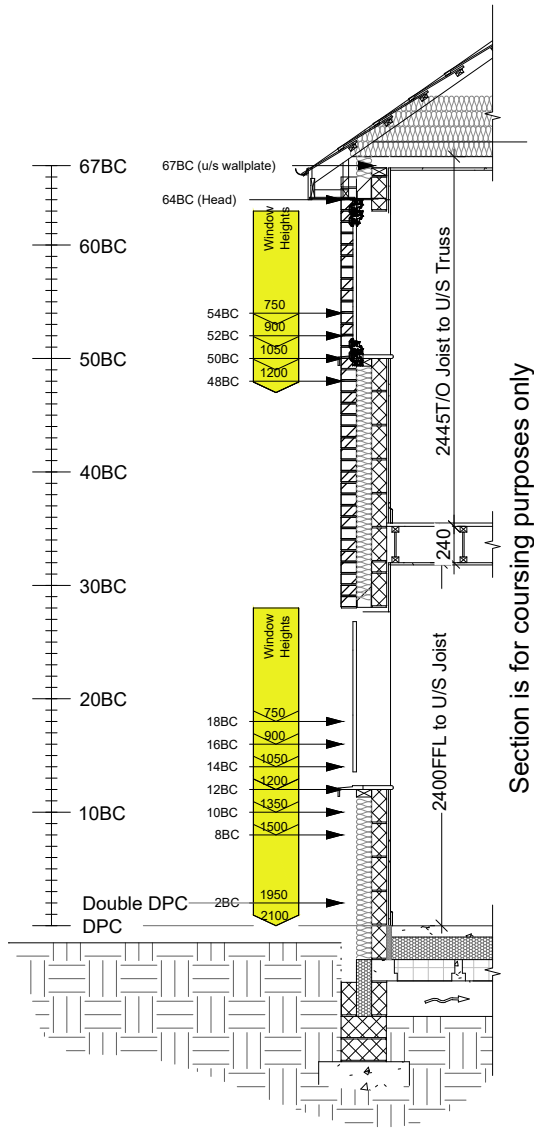

Bellway
www.bellway.co.uk

TENDER

Bellway Homes Limited (Eastern Counties)
Building 2030, Cambourne Business Park
Cambourne, Cambridgeshire, CB23 6DW
Tel: 01480 425200

Project
Somersham
St Ives Road
Working Drawings

Drawing Title The Halstead		
630 ft² 1b Semi-Det Country Brick Section A - A		
Drawing Created By FDL	First Issue Date April '25	Scale(s) 1 : 50
Project No BI01	Drg Status	Revision C1
Drawing No.		BI01 / 630HA / 20 / 01

1 Section A - A
1 : 50

Plots 26, 37, 39 (AS) & 27, 38, 40 (OPP)