


Revision Schedule			
Rev	Date	Description	Drn By
C1	02.12.25	Construction Issue	C1

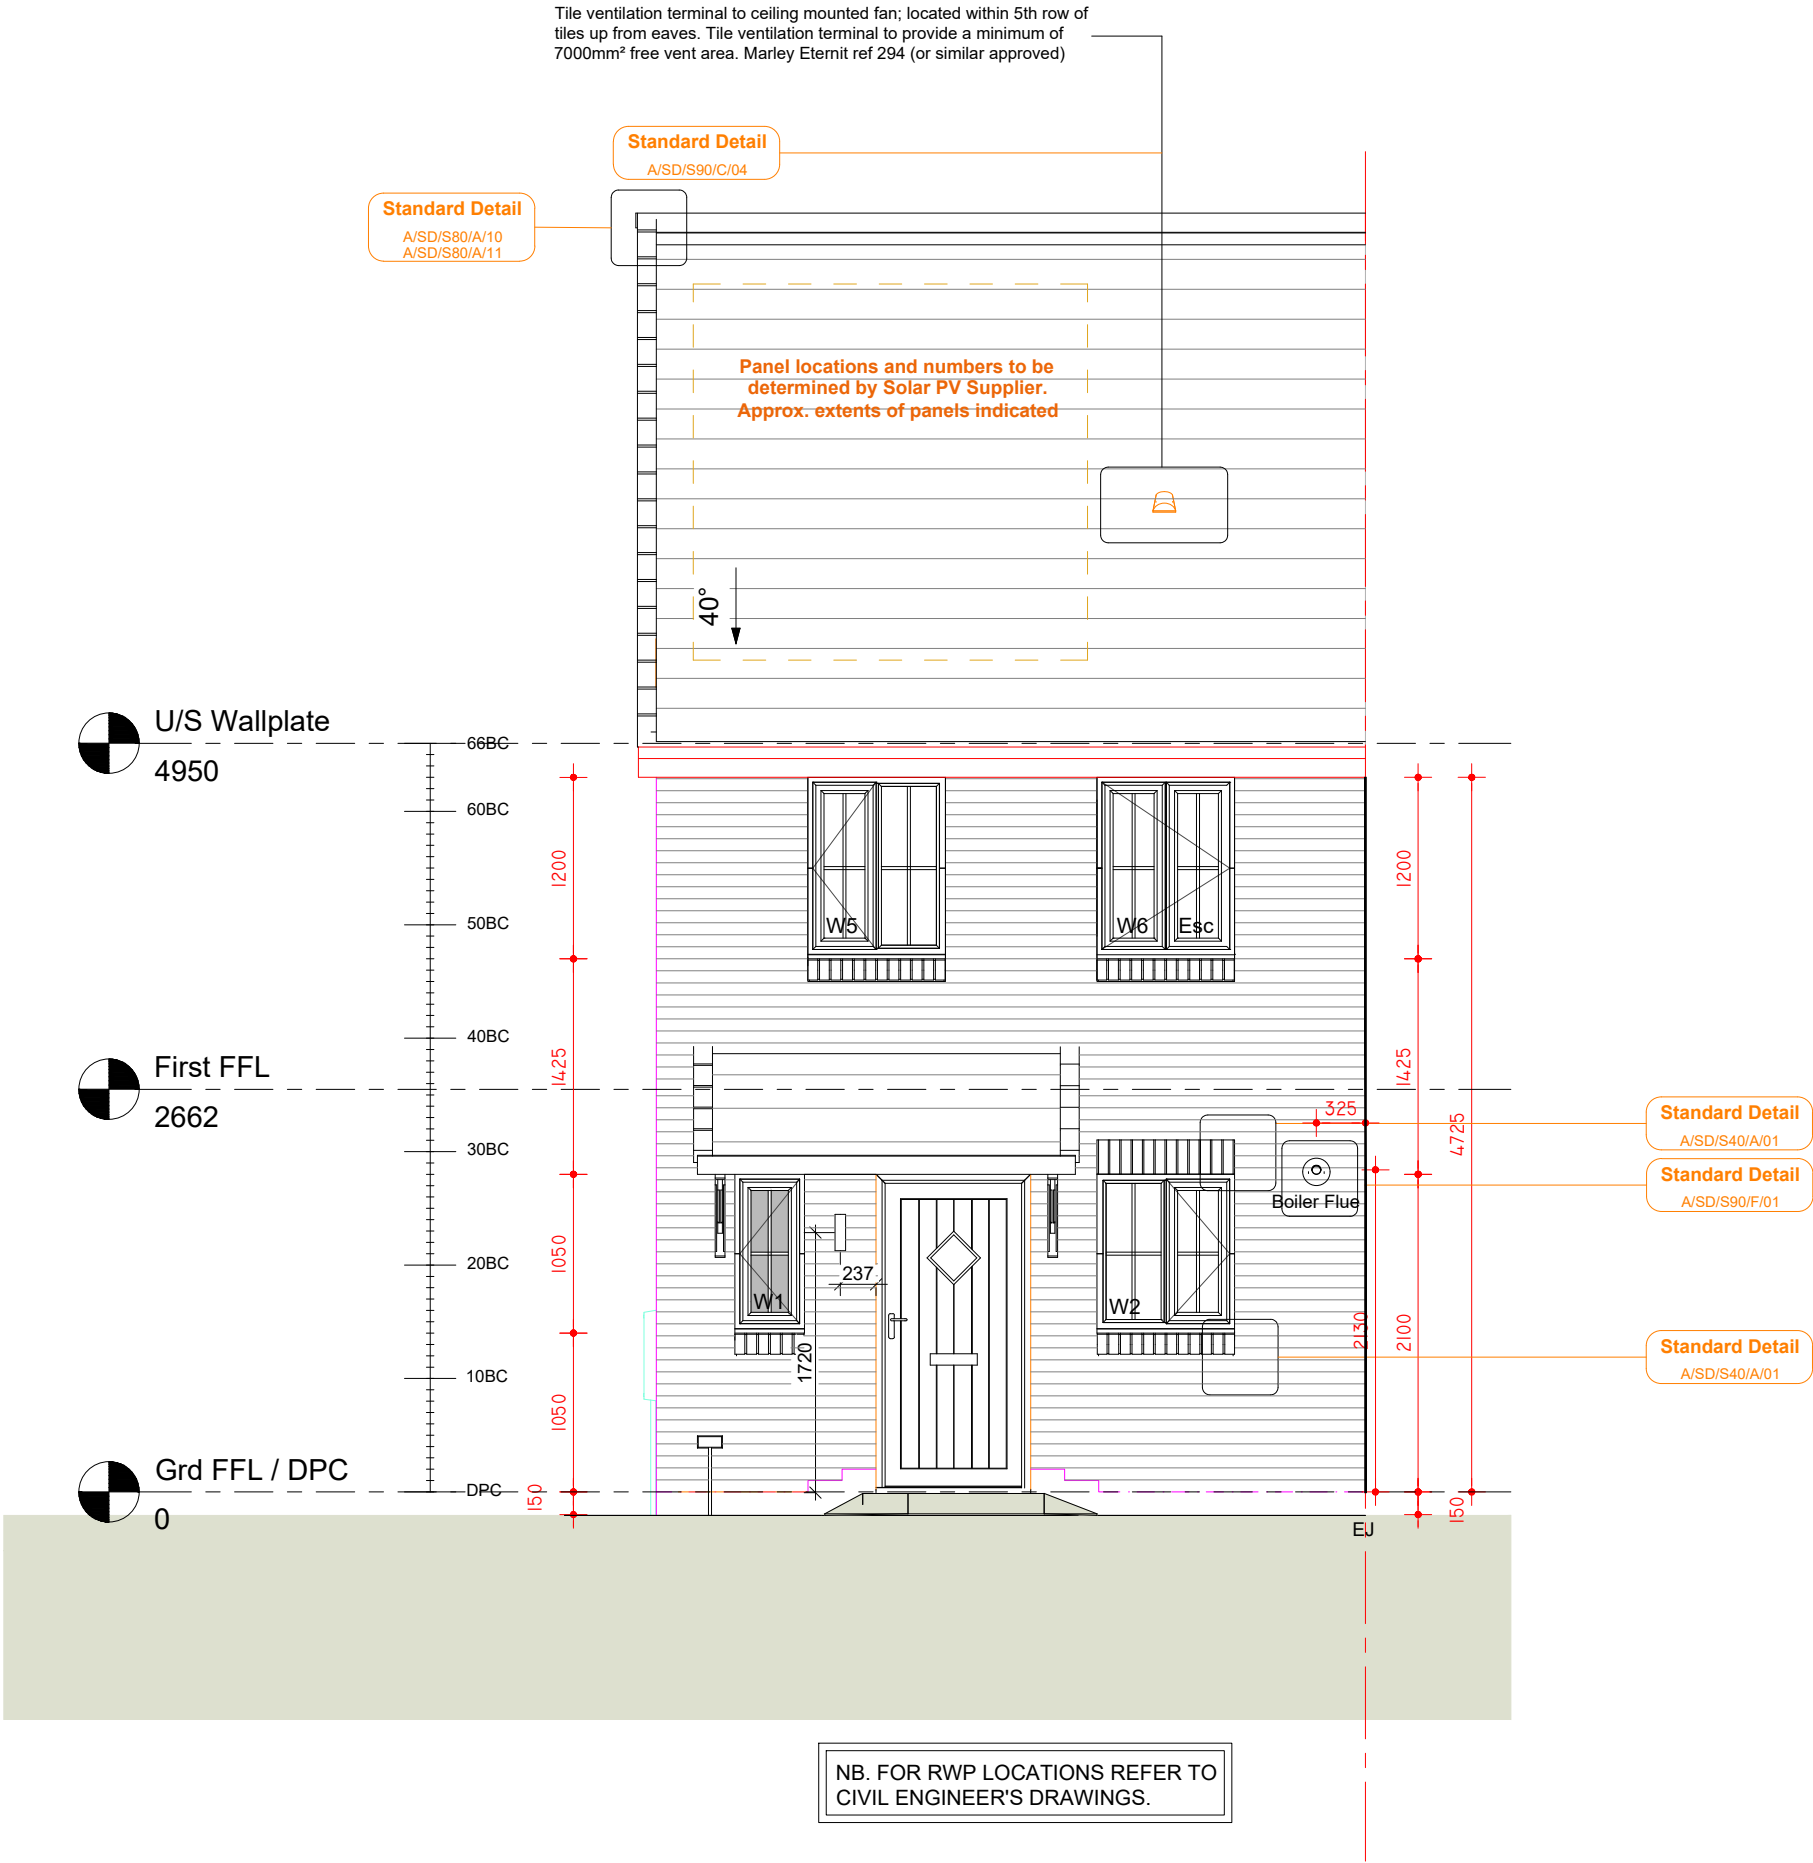

1 Front Elevation
1 : 50

TENDER


www.bellway.co.uk

Bellway Homes Limited (Eastern Counties)

Building 2030, Cambourne Business Park
Cambourne, Cambridgeshire, CB23 6DW
Tel: 01480 425200

Project

Somersham
St Ives Road
Working Drawings

Drawing Title

The Halstead

630 ft² | 1b Semi-Det | Country Brick

Front Elevation

Drawing Created By FDL	First Issue Date April '25	Scale(s) 1 : 50
Project No BI01	Drg Status	Revision C1
Drawing No.		BI01 / 630HA / 25 / 01

Plots 26, 37, 39 (AS) & 27, 38, 40 (OPP)