


Revision Schedule			
Rev	Date	Description	Drn By
C1	02.12.25	Construction Issue	C1

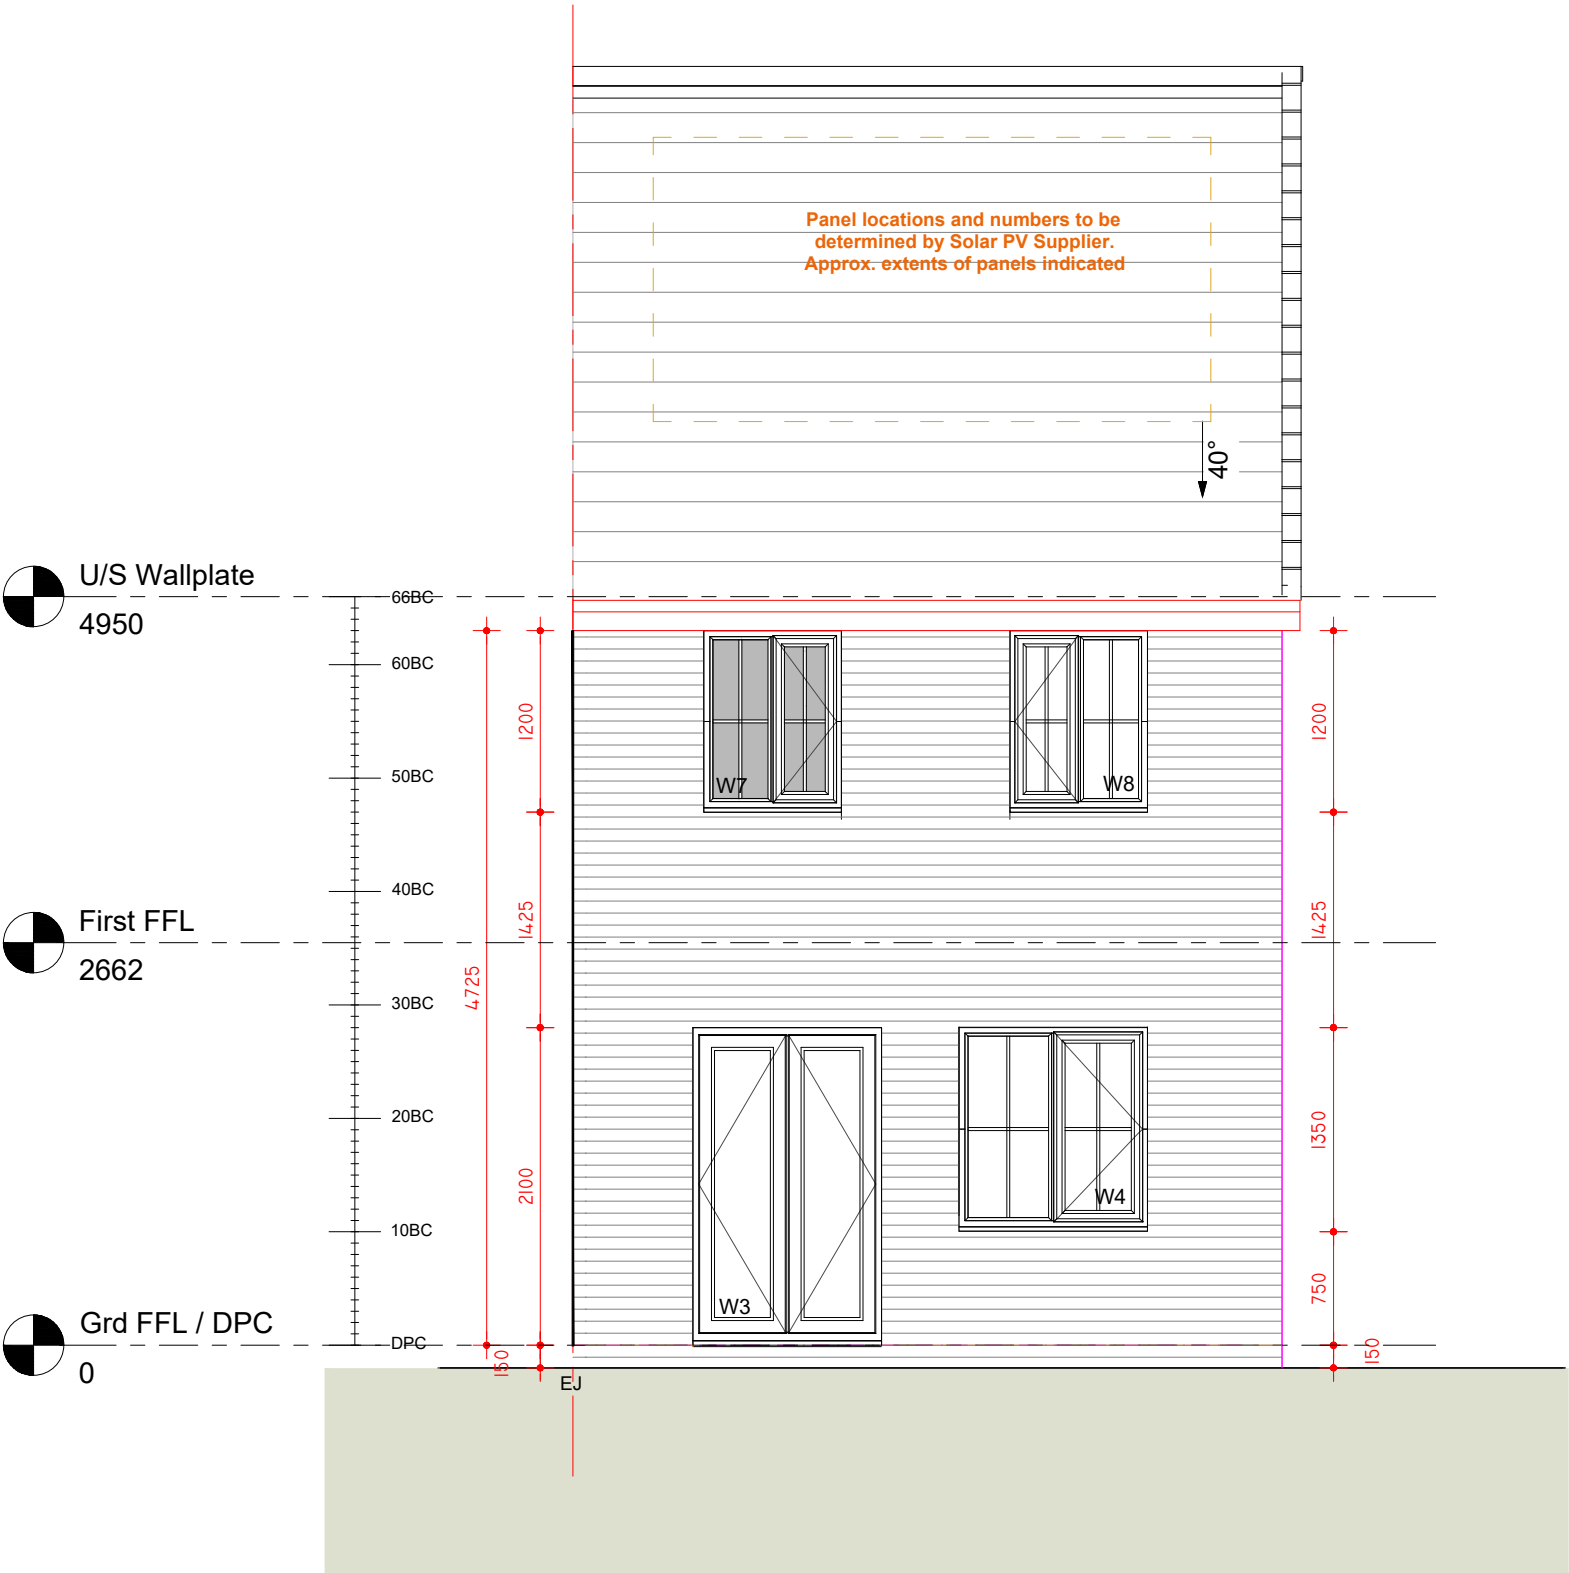

NB. FOR RWP LOCATIONS REFER TO
CIVIL ENGINEER'S DRAWINGS.

1 Rear Elevation
1 : 50

TENDER


www.bellway.co.uk

Bellway Homes Limited (Eastern Counties)

Building 2030, Cambourne Business Park
Cambourne, Cambridgeshire, CB23 6DW
Tel: 01480 425200

Project

Somersham
St Ives Road
Working Drawings

Drawing Title

The Halstead
630 ft² | 1b Semi-Det | Country Brick
Rear Elevation

Drawing Created By FDL	First Issue Date April '25	Scale(s) 1 : 50
Project No BI01	Drg Status	Revision C1
Drawing No.		BA01 / HA / 25 / 02