


Revision Schedule			
Rev	Date	Description	Drm By
C1	02.12.25	Construction Issue	C1

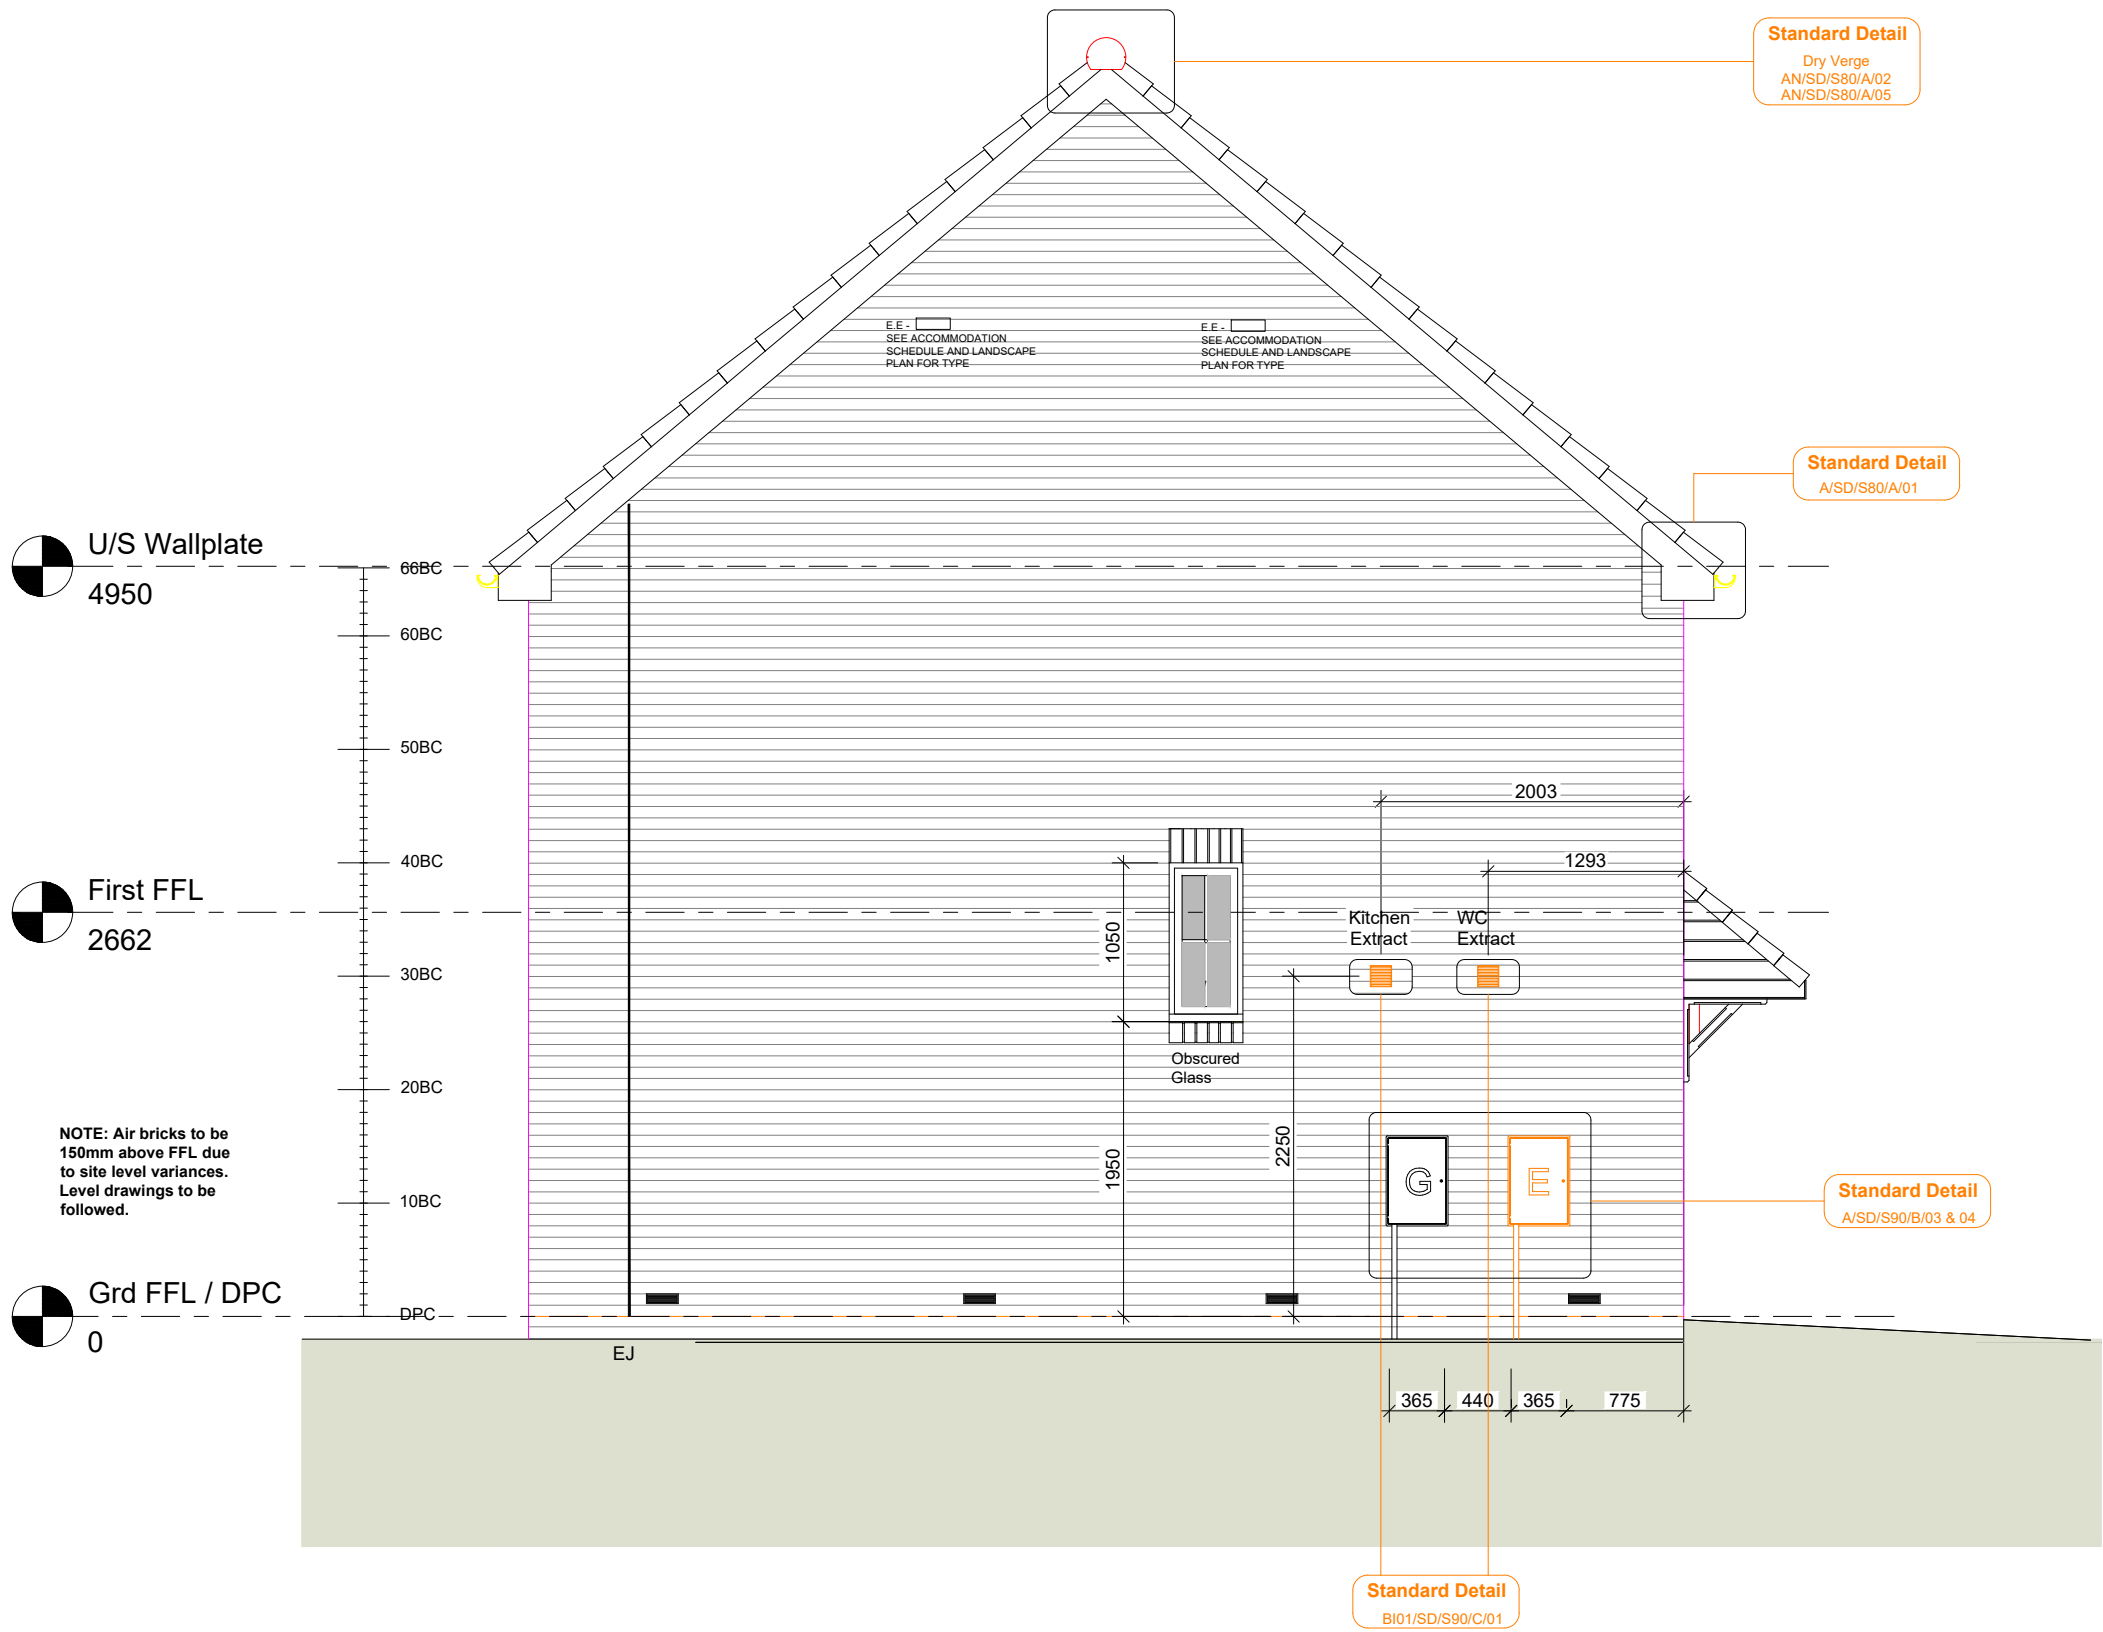

1 Gable Elevation
1 : 50

TENDER

Bellway
www.bellway.co.uk

Bellway Homes Limited (Eastern Counties)
Building 2030, Cambourne Business Park
Cambourne, Cambridgeshire, CB23 6DW
Tel: 01480 425200

Project
Somersham
St Ives Road
Working Drawings

Drawing Title
The Halstead
630 ft² | 1b Semi-Det | Country Brick
Gable Elevation

Drawing Created By FDL	First Issue Date April '25	Scale(s) 1 : 50
Project No BI01	Drg Status	Revision C1
Drawing No.		BI01 /630 HA / 25 / 03

Plots 26, 37, 39 (AS) & 27, 38, 40 (OPP)