

Revision Schedule			
Rev	Date	Description	Drn By
C1	02.12.25	Construction Issue	C1

Substructure Wall Legend (100mm Cavity)

	Standard External Insulated Cavity Wall (Below Ground) 100mm blocks (3.6N/mm²) upto 150mm below external ground level, then class B engineering brickwork (102.5mm) to DPC level 100mm cavity with expanded polystyrene board (thermal conductivity 0.038 W/m²/K) 100mm aerated concrete block / coursing bricks (3.6N/mm²)
	External Uninsulated Cavity Wall (To Garage etc - Below Ground) 100mm blocks (3.6N/mm²) upto 150mm below external ground level, then class B engineering brickwork (102.5mm) to DPC level 100mm cavity 100mm aerated concrete block / coursing bricks (3.6N/mm²)
	Party Wall (Below Ground) 100mm aircrete block (3.6N/mm²) 100mm cavity with expanded polystyrene board (thermal conductivity 0.038 W/m²/K) 100mm aircrete block (3.6N/mm²)
	Internal Blockwork Partition (Below Ground) 100mm aerated concrete block (3.6N/mm²) (Suspended ground floor beam manufacturer's coursing blocks / bricks as required)
	Sleeper Wall 100mm aerated concrete block (3.6N/mm²) to underside of suspended ground floor beams

Refer to current Construction Specification for further details

NB. FOR RWP LOCATIONS REFER TO
CIVIL ENGINEER'S DRAWINGS.

TENDER

www.bellway.co.uk

Bellway Homes Limited (Eastern Counties)


Building 2030, Cambourne Business Park
Cambourne, Cambridgeshire, CB23 6DW
Tel: 01480 425200

Project

Somersham
St Ives Road
Working Drawings

Drawing Title The Halstead		
630 ft² 1b Semi-Det Country Brick		
Substructure Blockplan - Semi		
Drawing Created By FDL	First Issue Date 28.03.25	Scale(s) 1 : 50
Project No BI01	Drg Status	Revision C1
Drawing No.		BI01 / 630HA / 30 / 02

1 Substructure Plan
1 : 50

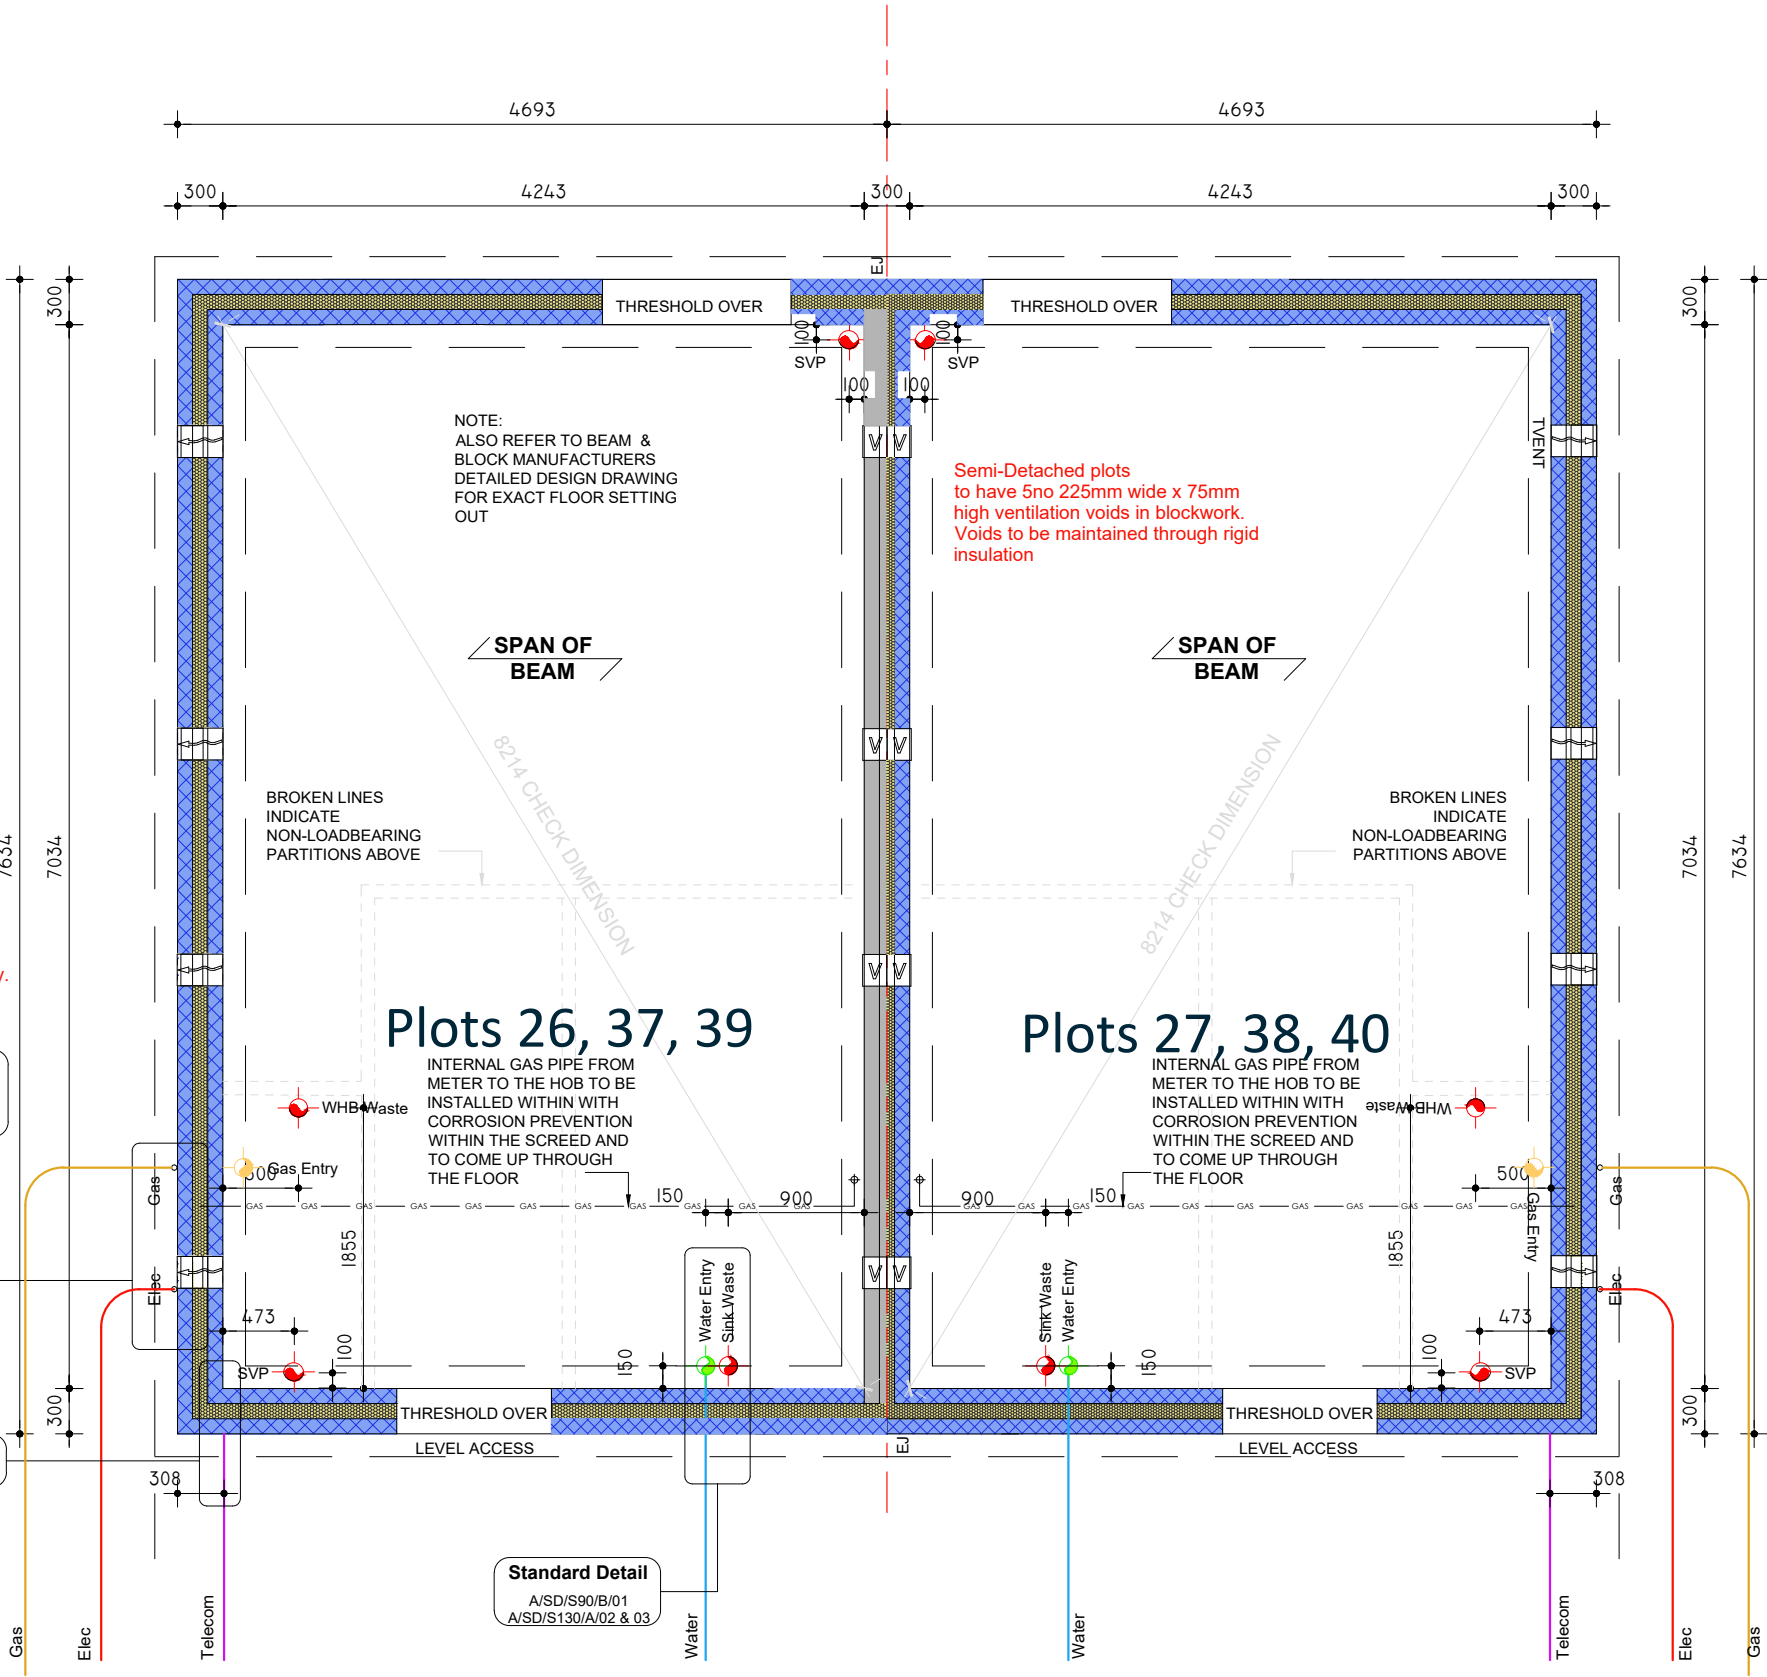

Plots 26, 27, 37, 38, 39 & 40