




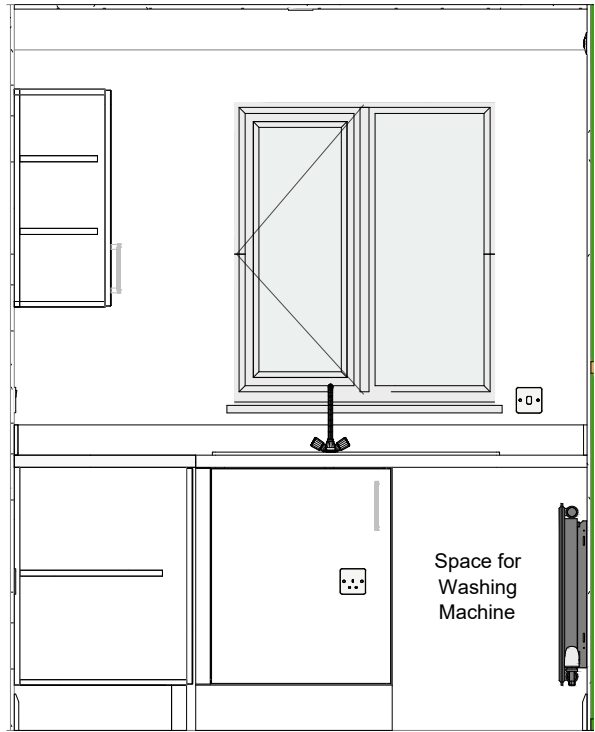

A Kitchen - View A
1 : 25

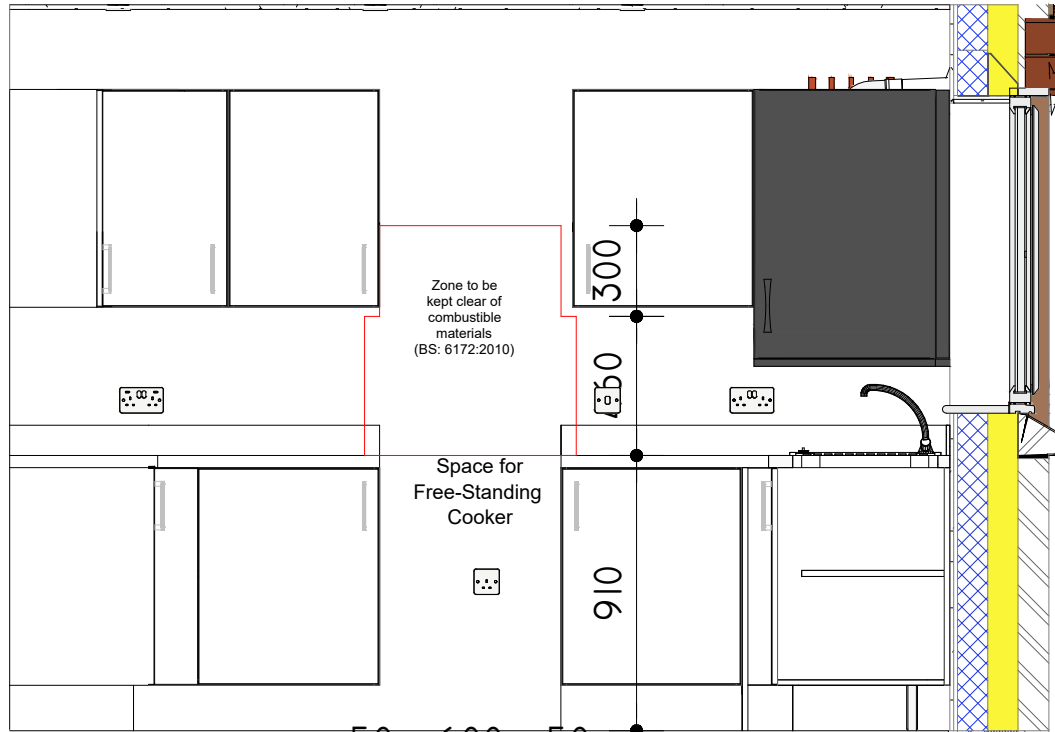


B Kitchen - View B
1 : 25

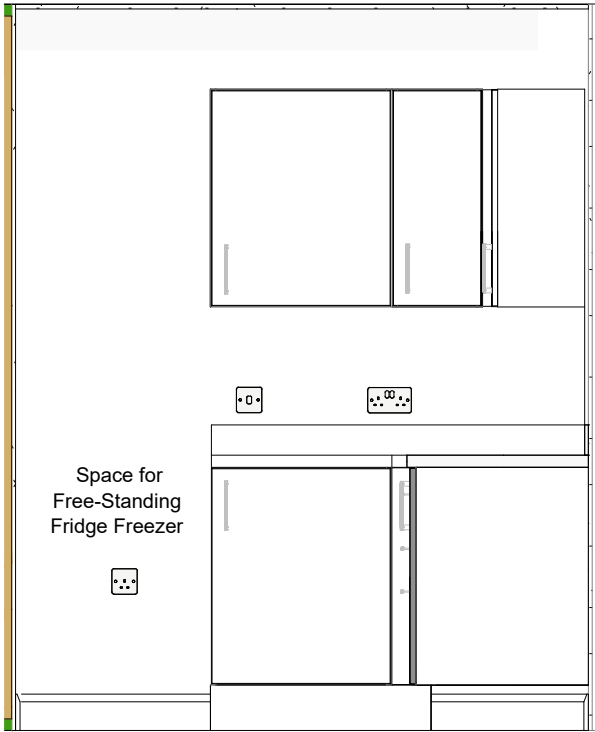

C Kitchen - View C
1 : 25



D Kitchen - View D
1 : 25

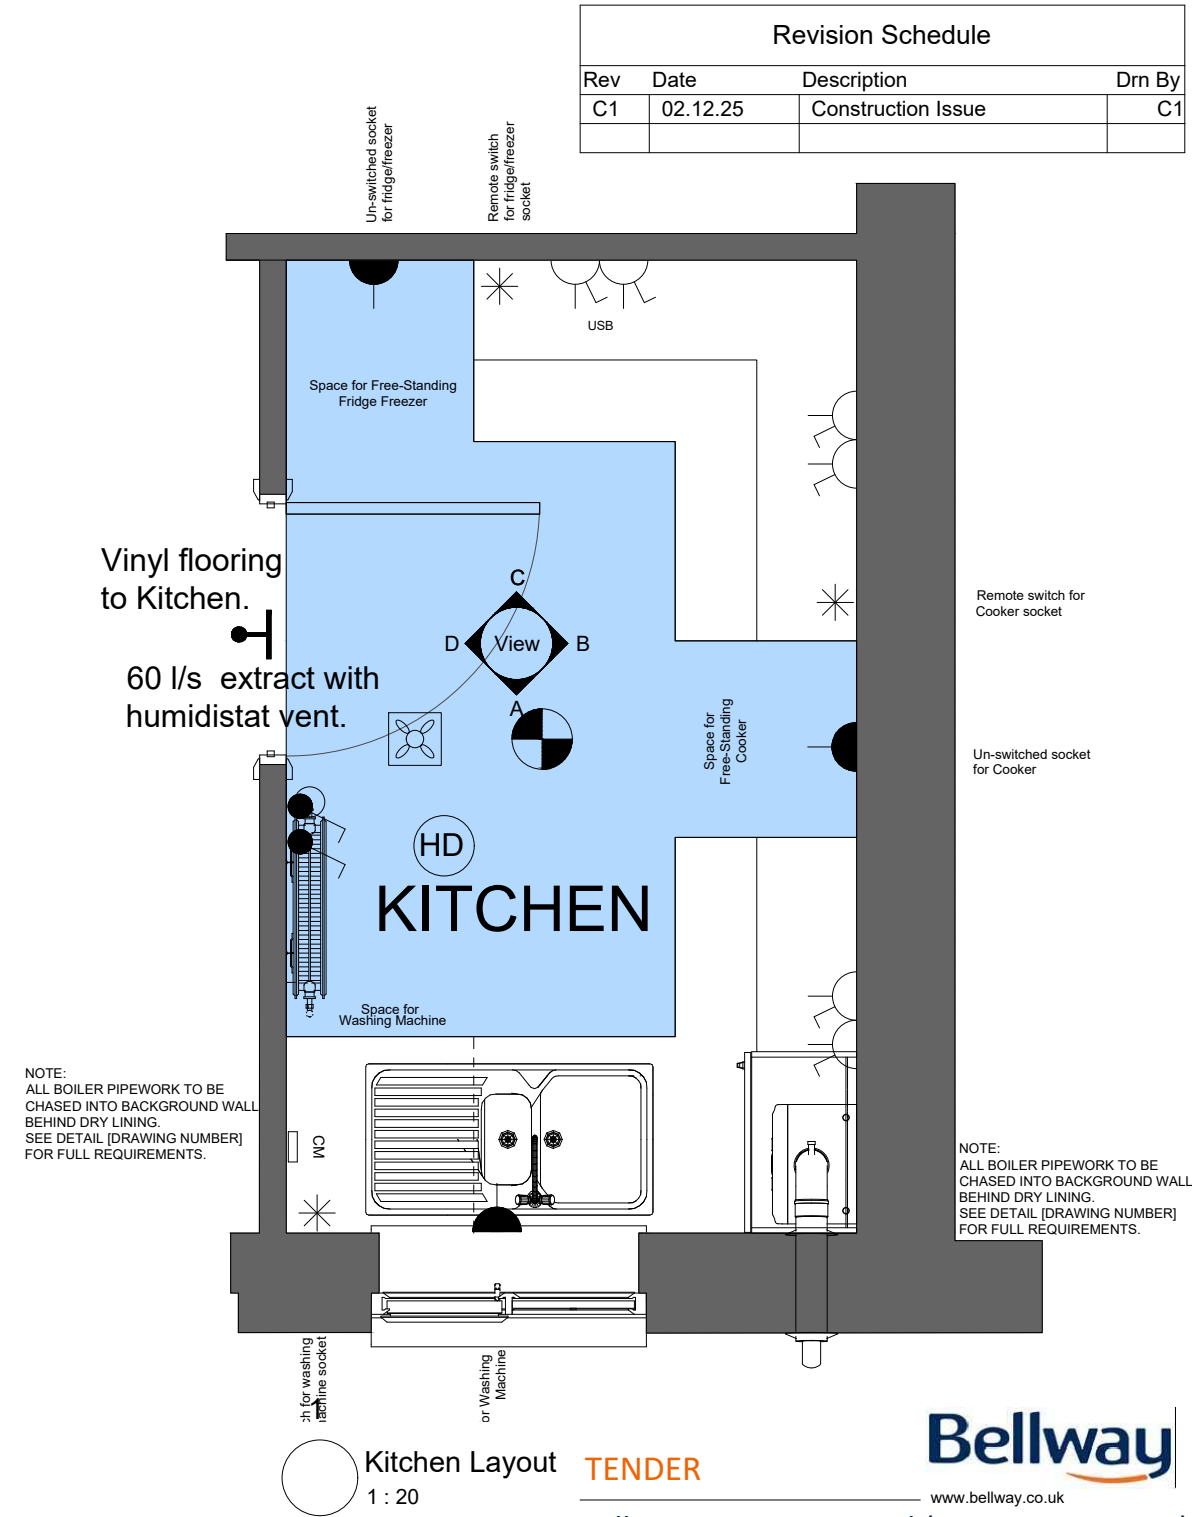

Bellway
www.bellway.co.uk

TENDER

Bellway Homes Limited (Eastern Counties)
Building 2030, Cambourne Business Park
Cambourne, Cambridgeshire, CB23 6DW
Tel: 01480 425200

Project
Somersham
St Ives Road
Working Drawings

Drawing Title
The Halstead
630 ft² | 1b Semi-Det | Country Brick
Kitchen Layout

Drawing Created By FDL	First Issue Date April '25	Scale(s) 1 : 25
Project No BI01	Drg Status	Revision C1
Drawing No.	BI01/ 630HA / 70 / 01	

Plots 26, 37, 39 (AS) & 27, 38, 40 (OPP)