


Revision Schedule			
Rev	Date	Description	Drn By
C1	01.12.25	Construction Issue	FDL

Part O requirements:-
Safety Rail to be installed at 1100mm, which may be omitted if
Build Tolerance to window opening is within a range of maximum
1100mm and minimum 1000mm

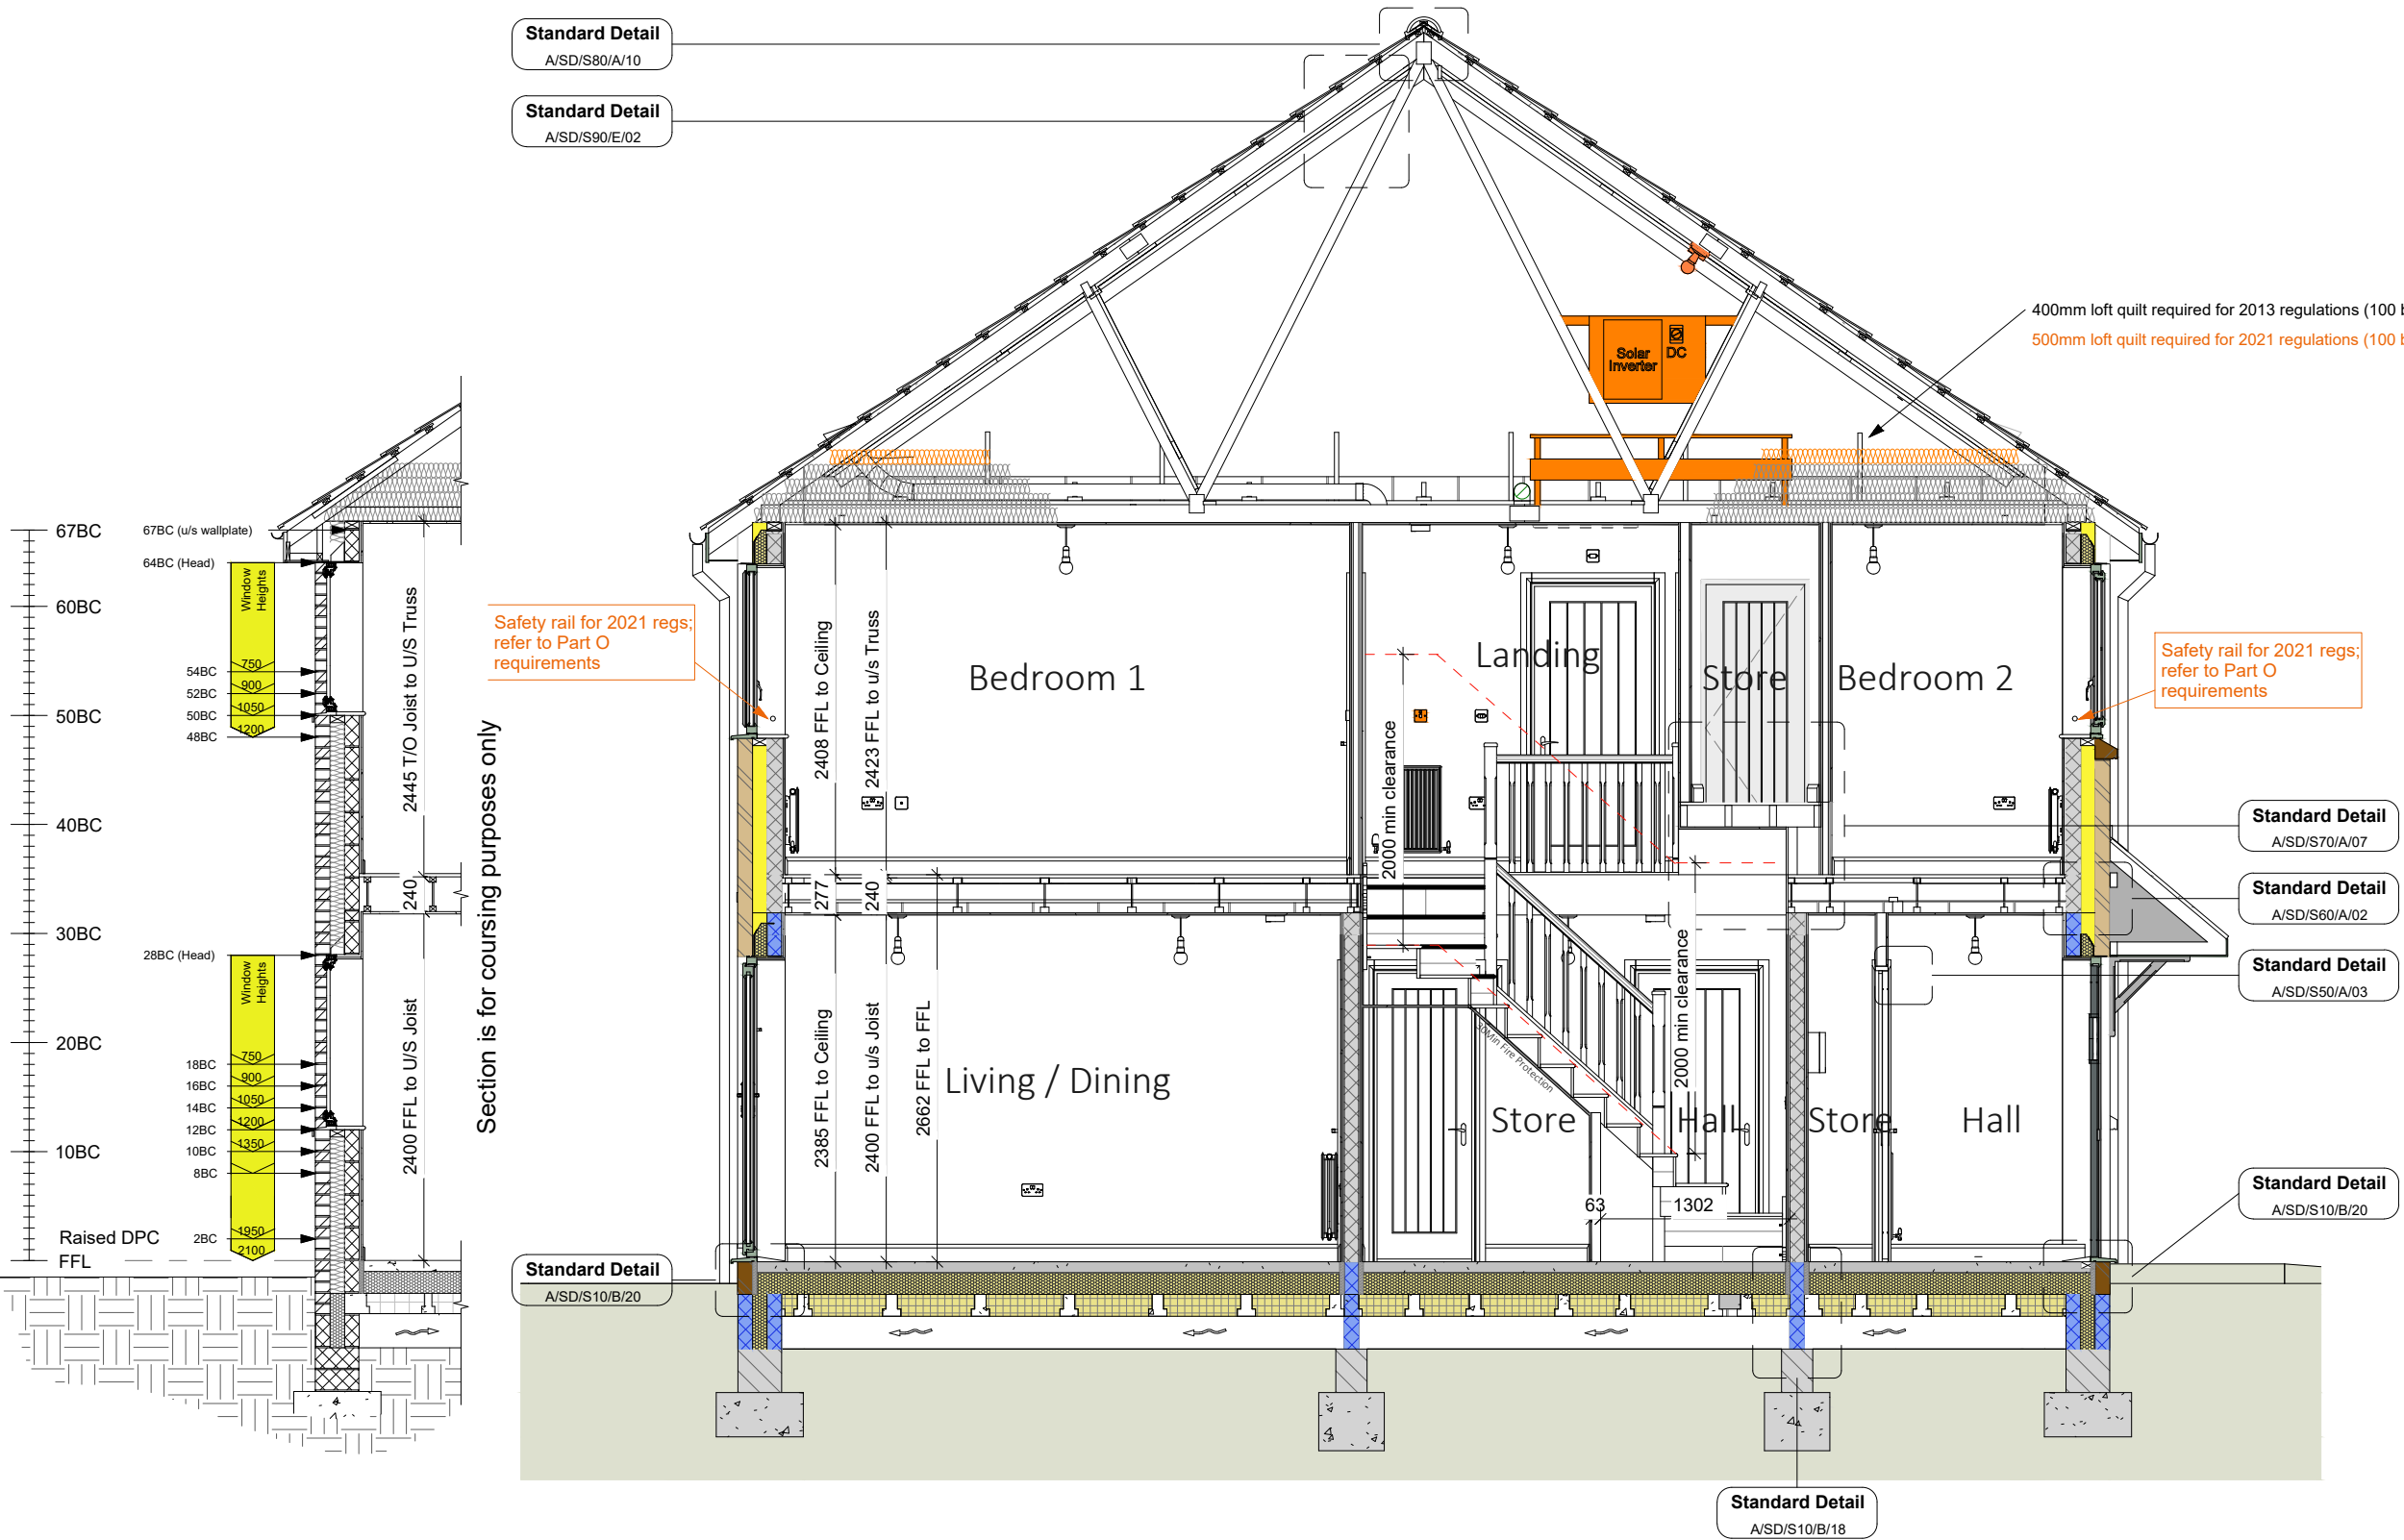

A Section A - A
1 : 50

CONSTRUCTION

Bellway
www.bellway.co.uk

Bellway Homes (Eastern Counties)
Building 2030, Cambourne Business Park,
Cambridgeshire CB23 6DW
Tel: 01480 425 200

Project
Somersham
St Ives Road
Working Drawings

Building Regulations
2013 & 2021
Compliant

Drawing Title
The Hooper-Life
790 ft² | 2b Semi/Terr | All Traditional Variants
Section A-A

HPL-2B-2S-AT

Drawing Created By Group	First Issue Date April '25	Scale(s) 1 : 50
Project No BI01	Drg Status Construction	Revision C1
Drawing No. BI01/790HP/20/AT/01		

Plots 10, 16, 41, 42 (AS) & 11, 17, 43 (OPP)

Do not scale - if in doubt, ask