


Revision Schedule			
Rev	Date	Description	Drn By
C1	01.12.25	Construction Issue	FDL

2021 Regulations
All fixed panes* in habitable rooms to become openable to satisfy Approved Document O requirements, as indicated by orange dashed lines (*excludes fixed panes to French Door sidelights, and entrance door sidelights).

PV Requirement
Solar PV will be required on this housetype. Panel locations and numbers to be determined on a site by site basis to take into account roof configuration and plot orientation.

Part O requirements:-
Safety Rail to be installed at 1100mm, which may be omitted if Build Tolerance to window opening is within a range of maximum 1100mm and minimum 1000mm

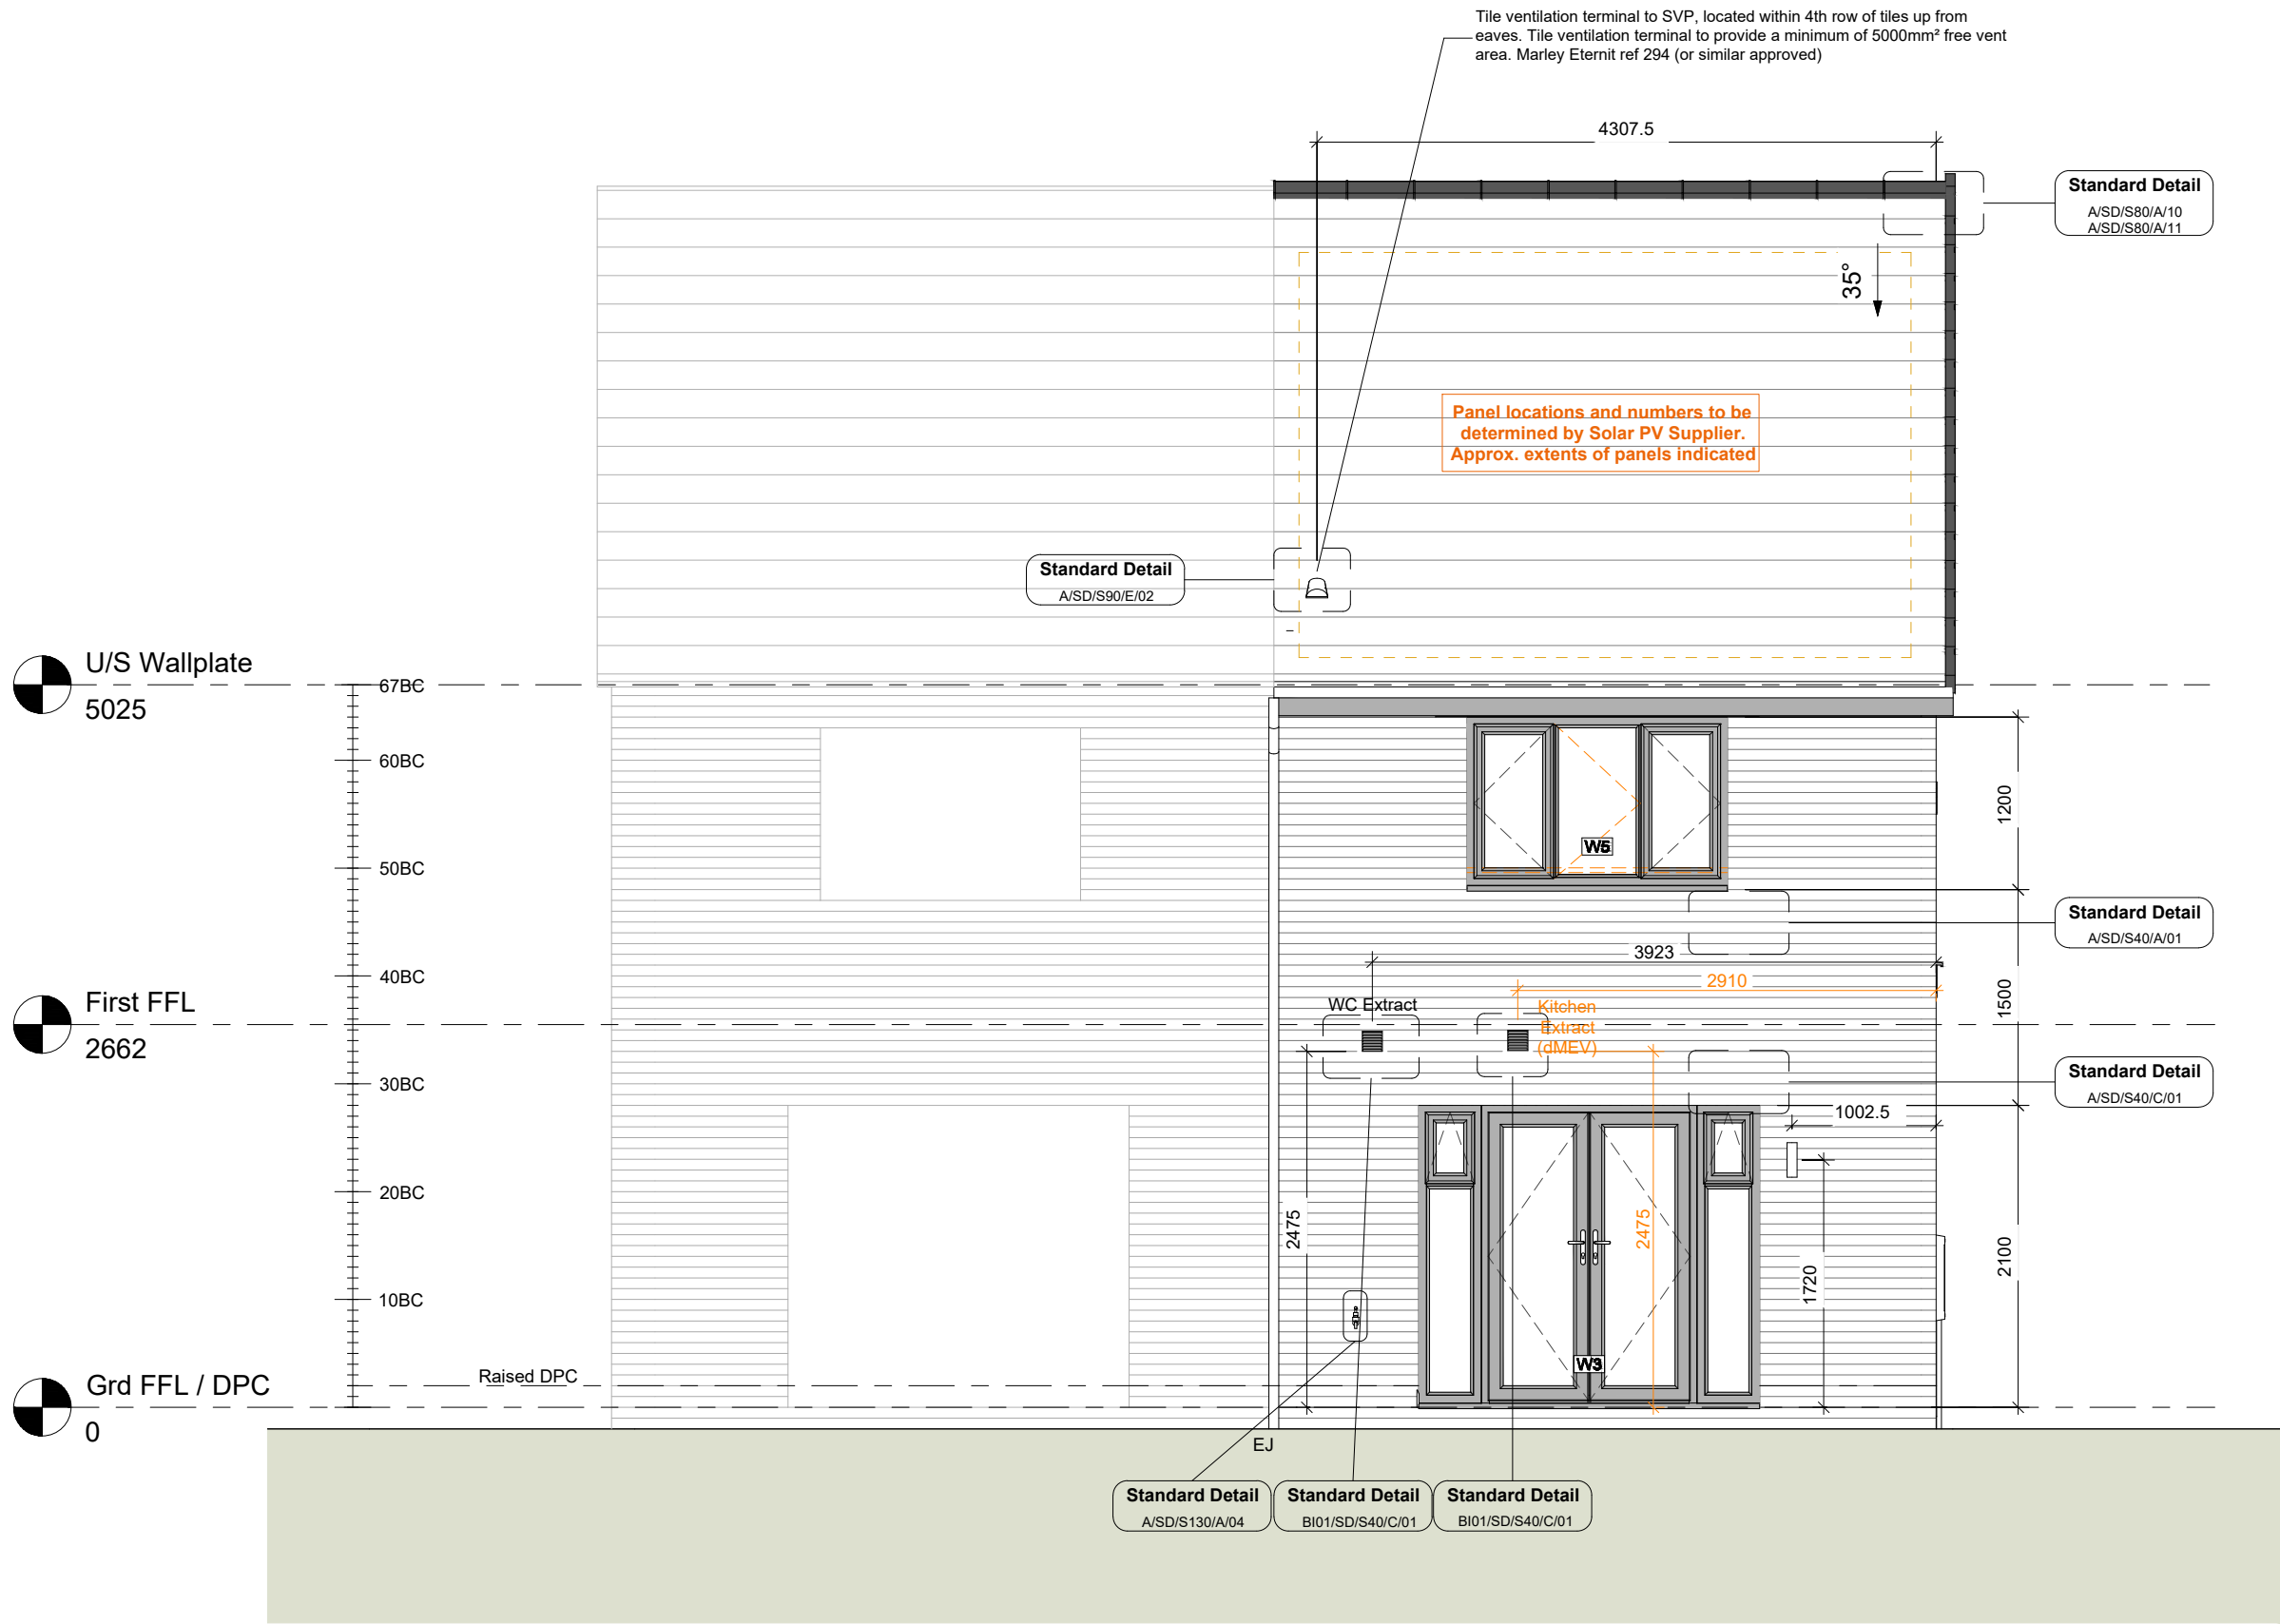

CONSTRUCTION

Bellway
www.bellway.co.uk

Bellway Homes (Eastern Counties)
Building 2030, Cambourne Business Park,
Cambridgeshire CB23 6DW
Tel: 01480 425 200

Building Regulations
2013 & 2021
Compliant

Project
Somersham
St Ives Road
Working Drawings

Drawing Title
The Hooper-Life
790 ft² | 2b Semi/Terr | Country Brick
Rear Elevation

HPL-2B-2S-CB

Drawing Created By Group	First Issue Date April '25	Scale(s) 1 : 50
Project No BI01	Drg Status Construction	Revision C1
Drawing No. BI01/790HP/25/CB/02		

Plots 10, 16, 41, 42 (AS) & 11, 17, 43 (OPP)

Do not scale - if in doubt, ask