



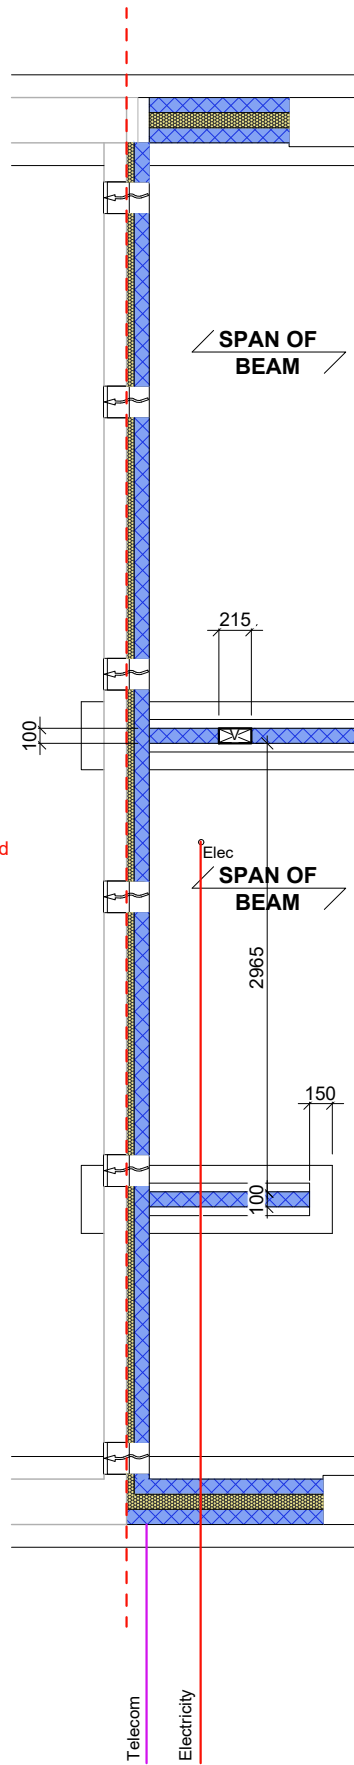

Semi-Detached and Mid-Terrace plots to have 6no 225mm wide x 75mm high ventilation voids in blockwork. Voids to be maintained through rigid insulation

2 Foundation - Terrace Services Variation
1 : 50

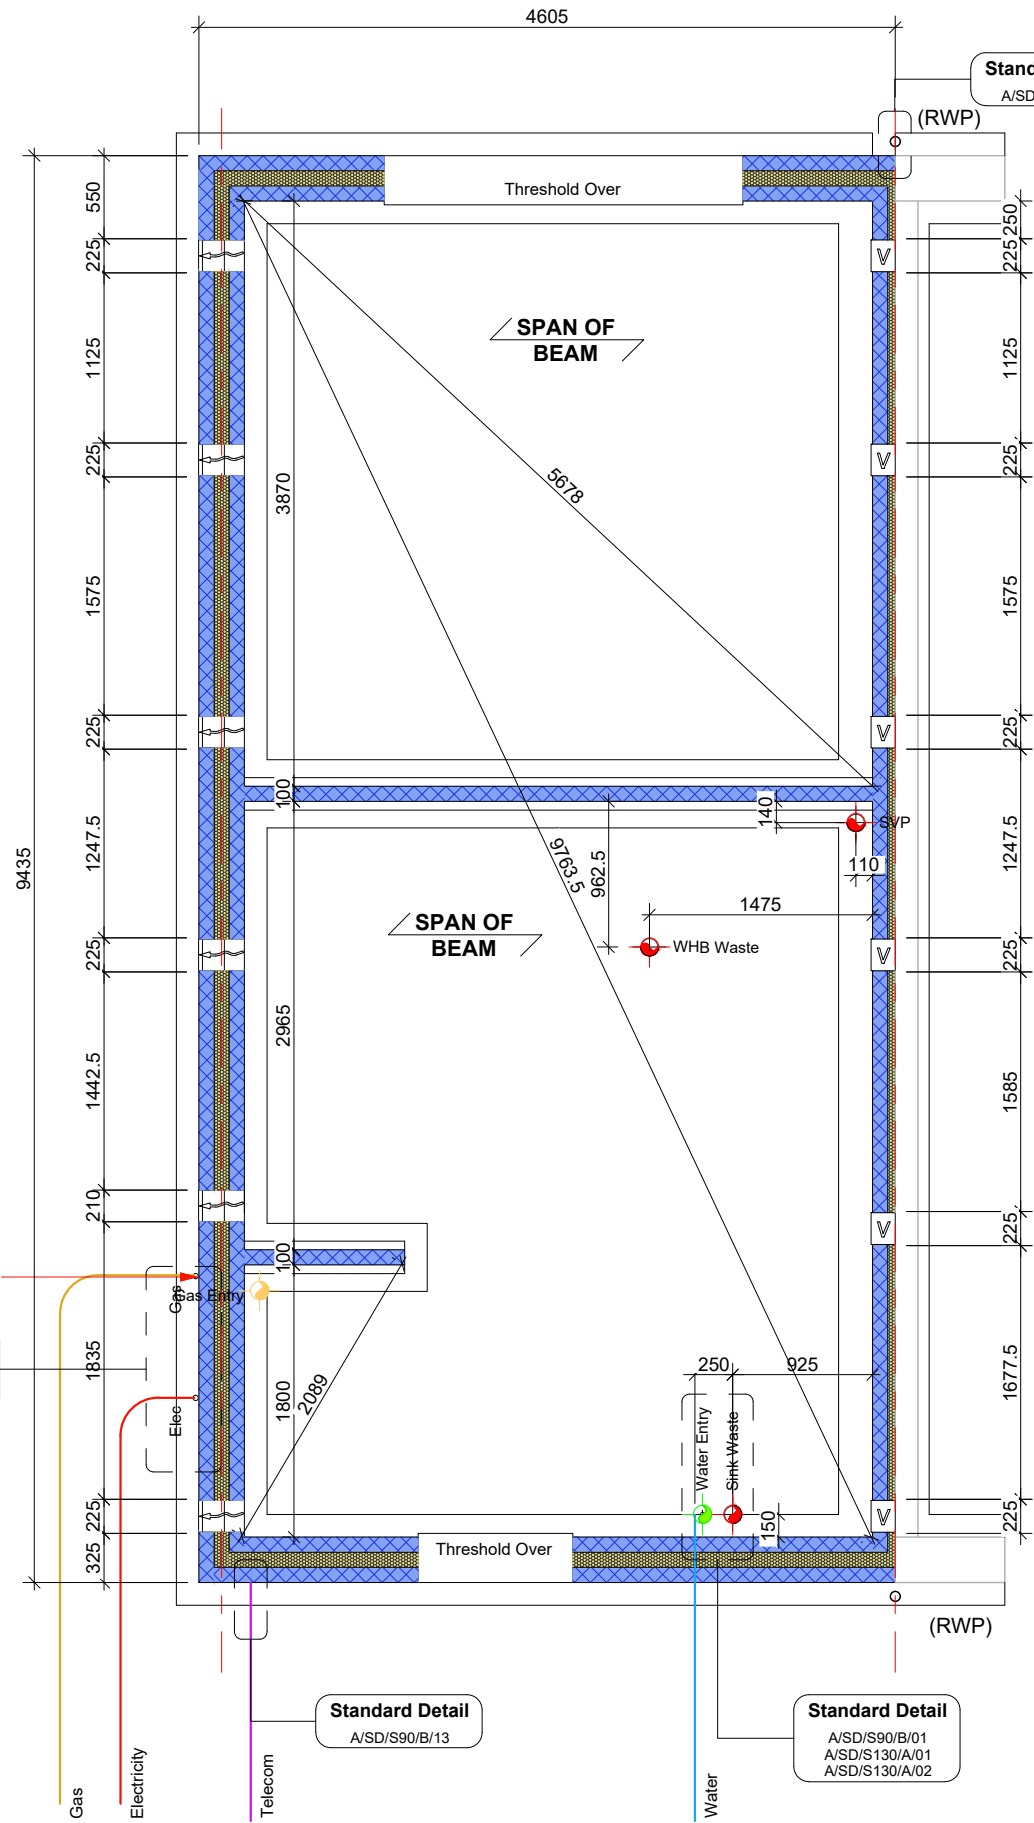

Ensure min 180mm between gas pipe and air brick

Semi-Detached and Mid-Terrace plots to have 6no 225mm wide x 75mm high ventilation voids in blockwork. Voids to be maintained through rigid insulation

1 Foundation - Semi Detached
1 : 50

Revision Schedule			
Rev	Date	Description	Drn By
C1	01.12.25	Construction Issue	FDL
C2	05.03.26	Mid terrace elec shown extending to understairs cupboard.	FDL

Substructure Wall Legend (100mm Cavity)

	Standard External Insulated Cavity Wall (Below Ground) 100mm blocks (3.6N/mm²) upto 150mm below external ground level, then class B engineering brickwork (102.5mm) to DPC level 100mm cavity with expanded polystyrene board (thermal conductivity 0.038 W/m²/K) 100mm aerated concrete block / coursing bricks (3.6N/mm²)
	External Uninsulated Cavity Wall (To Garage etc - Below Ground) 100mm blocks (3.6N/mm²) upto 150mm below external ground level, then class B engineering brickwork (102.5mm) to DPC level 100mm cavity 100mm aerated concrete block / coursing bricks (3.6N/mm²)
	Party Wall (Below Ground) 100mm aircrete block (3.6N/mm²) 100mm cavity with expanded polystyrene board (thermal conductivity 0.038 W/m²/K) 100mm aircrete block (3.6N/mm²)
	Internal Blockwork Partition (Below Ground) 100mm aerated concrete block (3.6N/mm²) (Suspended ground floor beam manufacturer's coursing blocks / bricks as required)
	Sleeper Wall 100mm aerated concrete block (3.6N/mm²) to underside of suspended ground floor beams

Refer to current Construction Specification for further details

CONSTRUCTION

www.bellway.co.uk

Bellway Homes (Eastern Counties)
Building 2030, Cambourne Business Park,
Cambridgeshire CB23 6DW
Tel: 01480 425 200

Building Regulations
2013 & 2021
Compliant

Project

Somersham
St Ives Road
Working Drawings

Drawing Title The Hooper-Life 790 ft² 2b Semi/Terr All Variants Foundation Layout			HPL-2B-2S-0	
Drawing Created By Group		First Issue Date 28.03.25		Scale(s) 1 : 50
Project No BI01		Drg Status Construction		Revision C2
Drawing No.			BI01/790HP/30/0/01	