


Revision Schedule			
Rev	Date	Description	Drn By
C1	01.12.25	Construction Issue	FDL

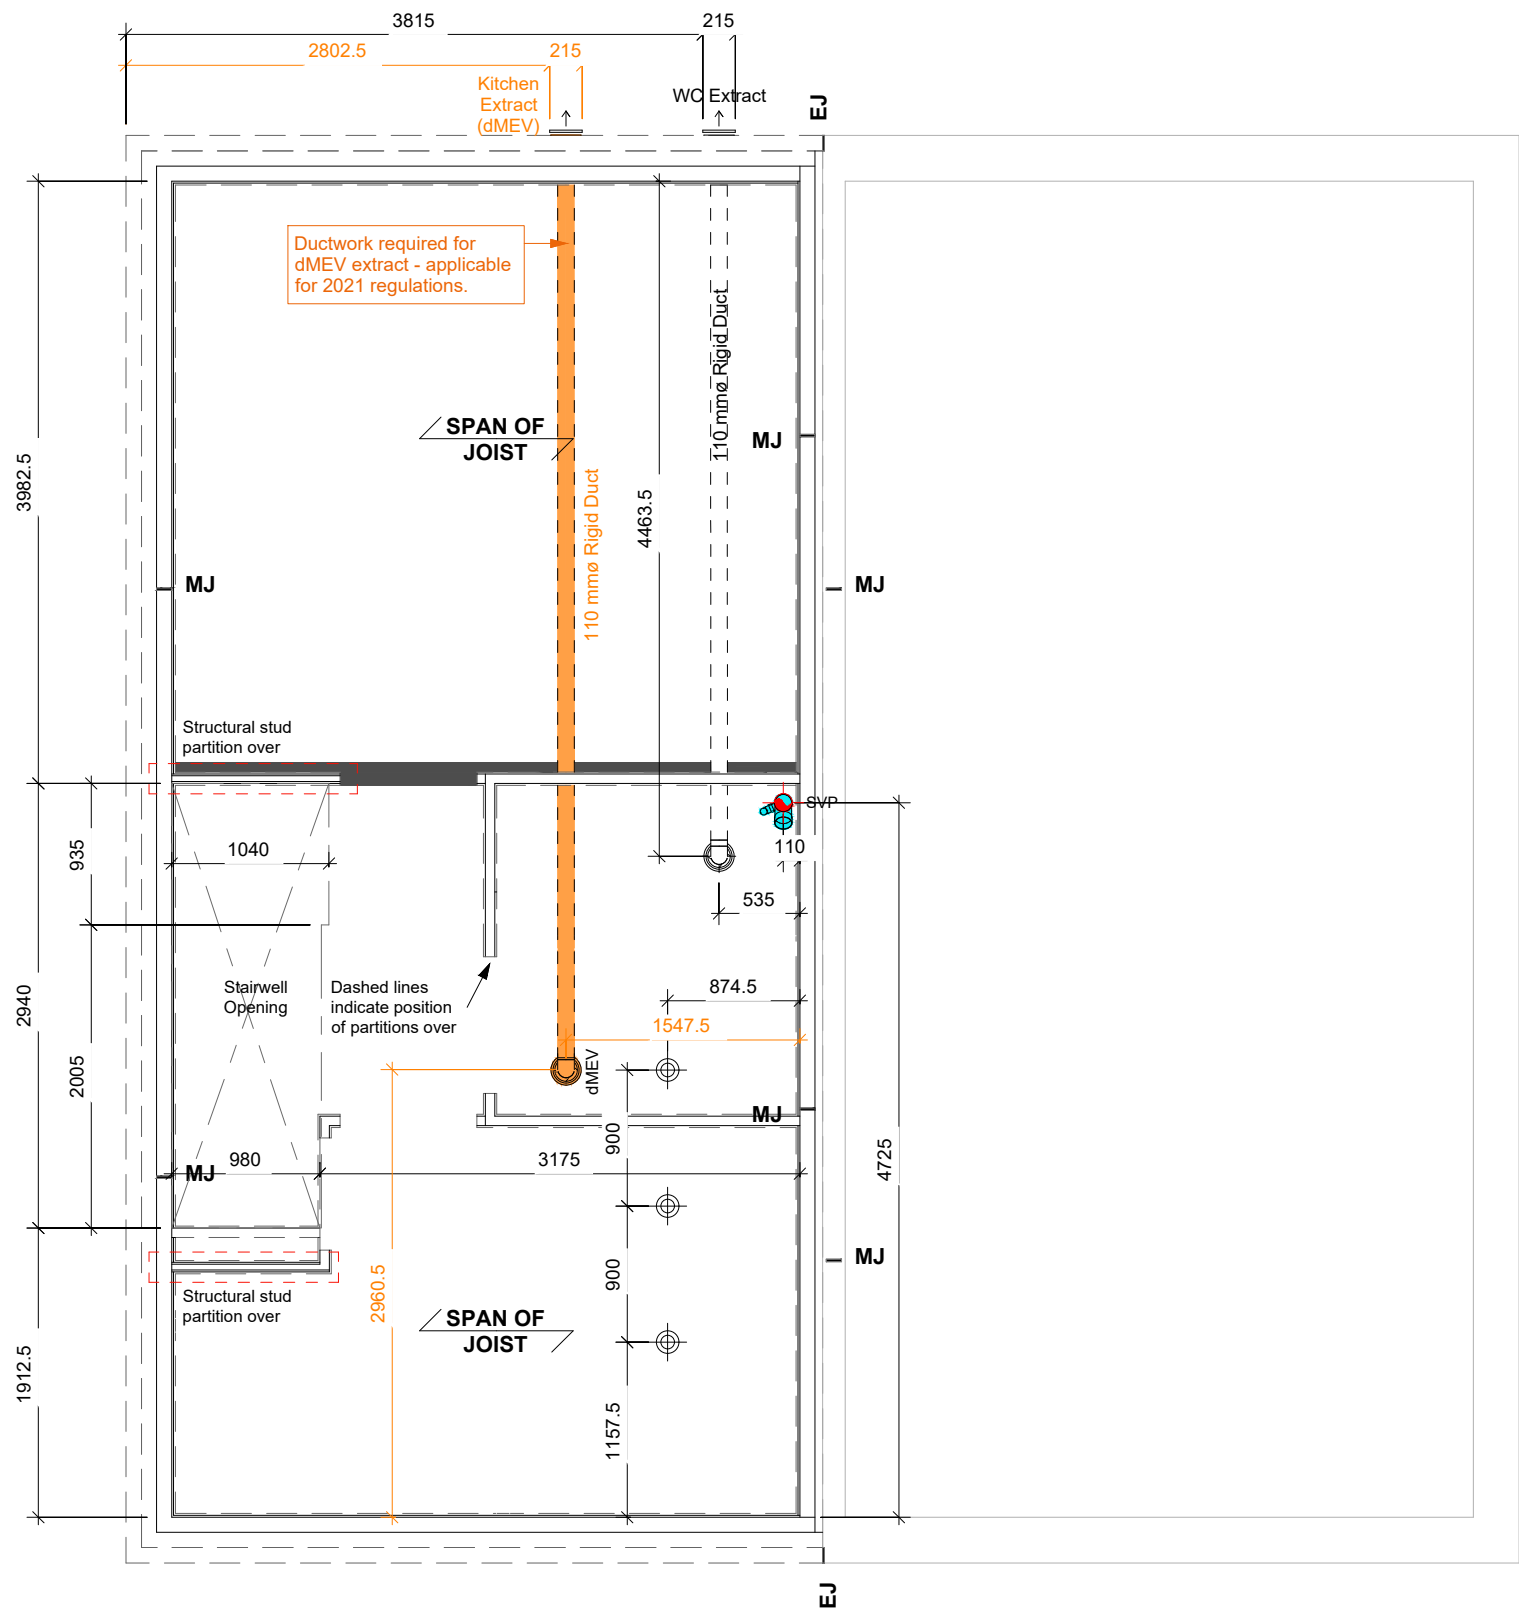

1 First Floor Joist Setting Out
1 : 50

Plots 10, 16, 41, 42 (AS) & 11, 17, 43 (OPP)

CONSTRUCTION

Bellway
www.bellway.co.uk

Bellway Homes (Eastern Counties)
Building 2030, Cambourne Business Park,
Cambridgeshire CB23 6DW
Tel: 01480 425 200

Project
Somersham
St Ives Road
Working Drawings

Building Regulations
2013 & 2021
Compliant

Drawing Title		
The Hooper-Life		HPL-2B-2S-0
790 ft² 2b Semi/Terr All Variants		
First Floor Joist Setting Out		
Drawing Created By	First Issue Date	Scale(s)
Group	April '25	1 : 50
Project No	Drg Status	Revision
BI01	Construction	C1
Drawing No.		BI01/790HP/40/0/01

Do not scale - if in doubt, ask