


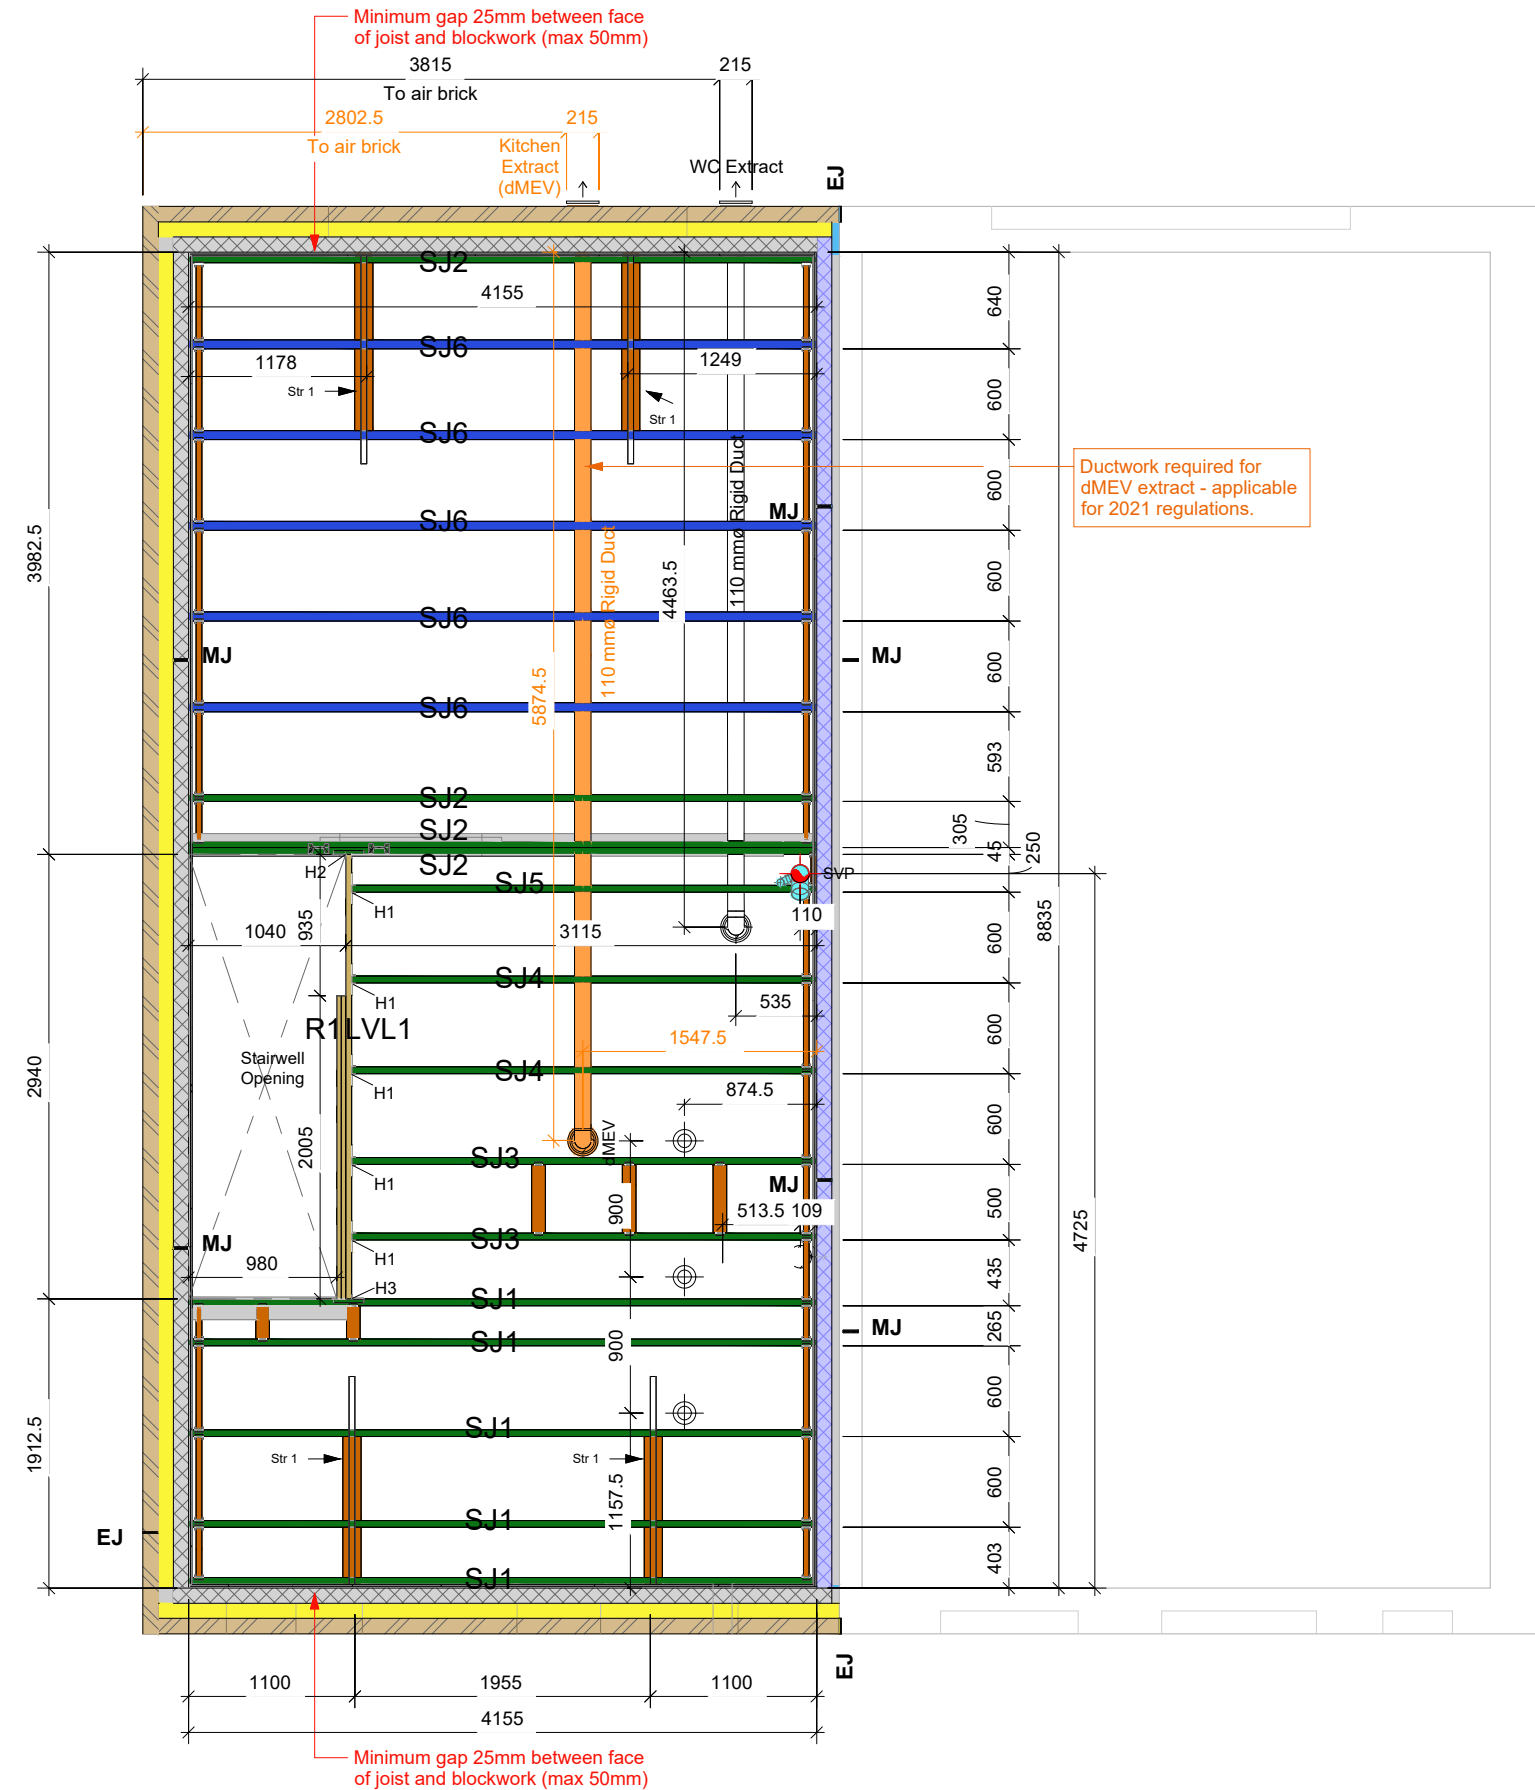

1 First Floor Joists
1 : 50

Steico First Floor Joists & Blocking

Qty	Ref	Length	Description
Beam/Joist			
1	LVL1	2940mm	ST4022 STEICO LVL R - 39x240mm
5	SJ1	4355mm	ST4119 SJL 45 - 240mm
4	SJ2	4355mm	ST4119 SJL 45 - 240mm
2	SJ3	3176mm	ST4119 SJL 45 - 240mm
2	SJ4	3176mm	ST4119 SJL 45 - 240mm
1	SJ5	3176mm	ST4119 SJL 45 - 240mm
5	SJ6	4355mm	ST4125 SJL 60 - 240mm

Noggin			
28	CN1		G7002 38x38 Nogging
5	PN1		G7000 Partition Nogging (38x90)
12	SN1		G7055 38x120mm Nogging - Plank

Rimboard			
2	R1	2005mm	ST1157 STEICO LVL X - 30x240mm

Steico First Floor Accessories

Ref	Description	Qty
ZS38N Z Clip 38mm		
		66
Backer Block		
BB1	ST3202 Backer Block 300 x 157 x 18 mm	1
End Device		
SES158/45	End Device	23
SES158/58	End Device	10
Hanger		
H1	EWB(T)235/47	5
H2	EWB(T)235/40	1
H3	EWB(T)235/40	1
I-Clip		
MJC1	G8138 MJC	4
Strap		
Str1	G8304 Simpson HES15B10	4

Revision Schedule

Rev	Date	Description	Drn By
C1	01.12.25	Construction Issue	FDL

Project Information

File Name	STEICO HOOPER APR 2023- NHBC 2023 EC5 Analytics.skd
Design Date	31 May 2023
Software Version No.	1.0.214

Design Information

Region	UK
Design Code	EC5
Application	A - Residential Upper Floor
Service Class	Service Class 1

Load and Deflection Settings

Dead Load (kN/m²)	0.40 - Permanent
Partitions Load (kN/m²)	0.35 - Permanent
Floor Imposed UD Load (kN/m²)	1.50 - Medium Term
Floor Imposed Concentrated Load (kN)	2.00 - Medium Term
Instantaneous Deflection	333 - 12mm
Net Final Deflection	250 -

Additional Information

Decking Type	Particle Board - 22mm P5
Direct Applied Ceiling	Yes
Ceiling Material	15mm - Ceiling (Gypsum board)



CONSTRUCTION



Bellway Homes (Eastern Counties)

Building 2030, Cambourne Business Park,
Cambridgeshire CB23 6DW
Tel: 01480 425 200

Project

Somersham

St Ives Road
Working Drawings

Drawing Title

The Hooper-Life

HPL-2B-2S-0

790 ft² | 2b Semi/Terr | All Variants
Joist Plan and Take Off

Drawing Created By	First Issue Date	Scale(s)
Group	April '25	1 : 50
Project No	Drg Status	Revision
BI01	Construction	C1

Drawing No. BI01/790HP/40/0/02

Plots 10, 16, 41, 42 (AS) & 11, 17, 43 (OPP)

Do not scale - if in doubt, ask