

Revision Schedule			
Rev	Date	Description	Drn By
C1	01.12.25	Construction Issue	FDL

Floorboard Schedule	
Qty	Description
27	22mm thick tongue and grooved chipboard floor board (2400 x 600mm)

CONSTRUCTION

Bellway

www.bellway.co.uk

Bellway Homes (Eastern Counties)

Building 2030, Cambourne Business Park,
Cambridgeshire CB23 6DW
Tel: 01480 425 200

Building Regulations
2013 & 2021
Compliant

Project
Somersham
St Ives Road
Working Drawings


Drawing Title

The Hooper-Life

HPL-2B-2S-0

790 ft² | 2b Semi/Terr | All Variants
Floor Boards Layout

Drawing Created By	First Issue Date	Scale(s)
Group	April '25	1 : 50
Project No	Drg Status	Revision
BI01	Construction	C1
Drawing No.		BI01/790HP/40/0/04

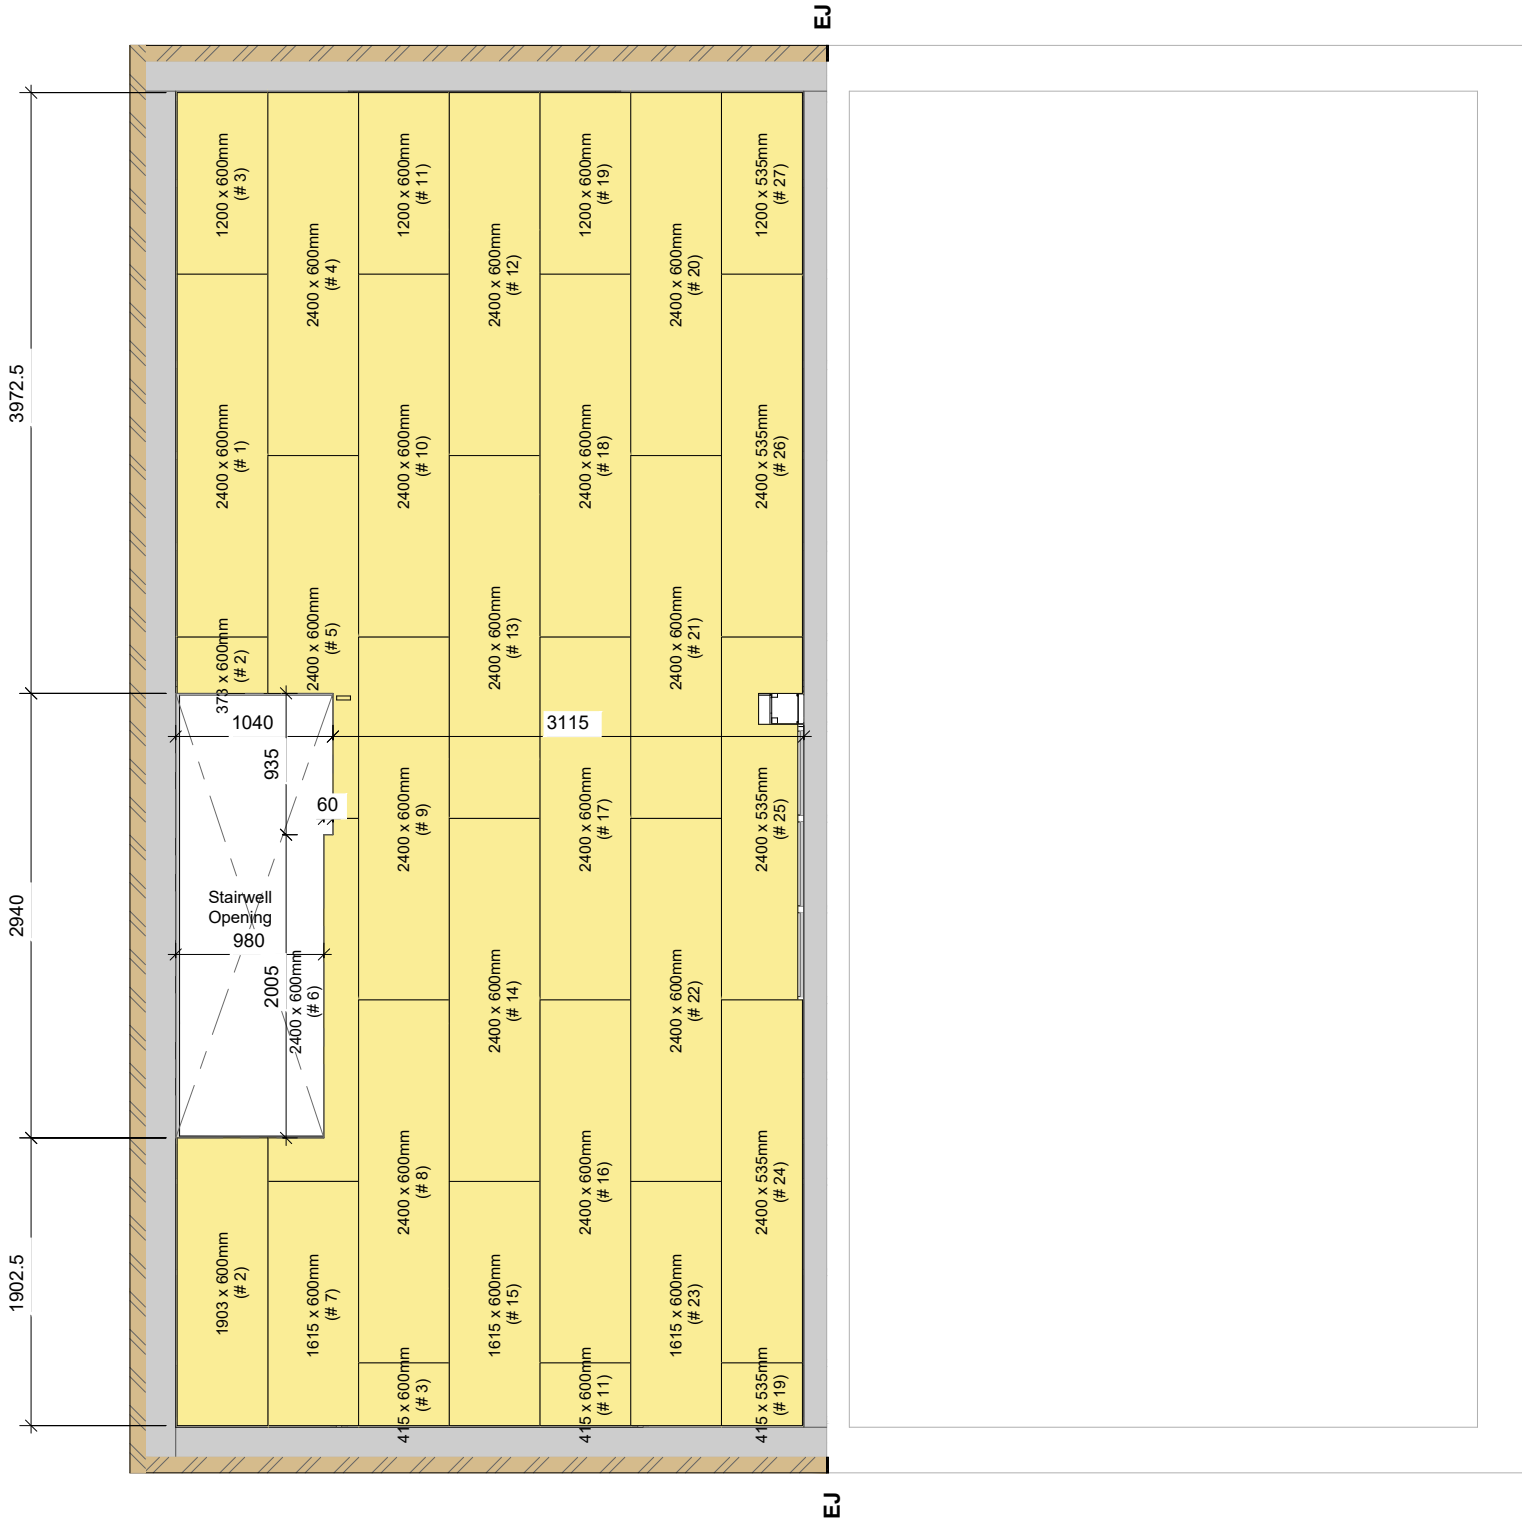

1 First Floor Floorboards
1 : 50