


Staircraft Drawing Ref:


House Type Name: HOOPER
Handing*: LHWS
Finished Floor Level (FFL) 2662
Revision: A

*Handing of staircase to be confirmed at point of call off.


Revision Schedule			
Rev	Date	Description	Drn By
C1	02/12/2025	Construction Issue.	FDL

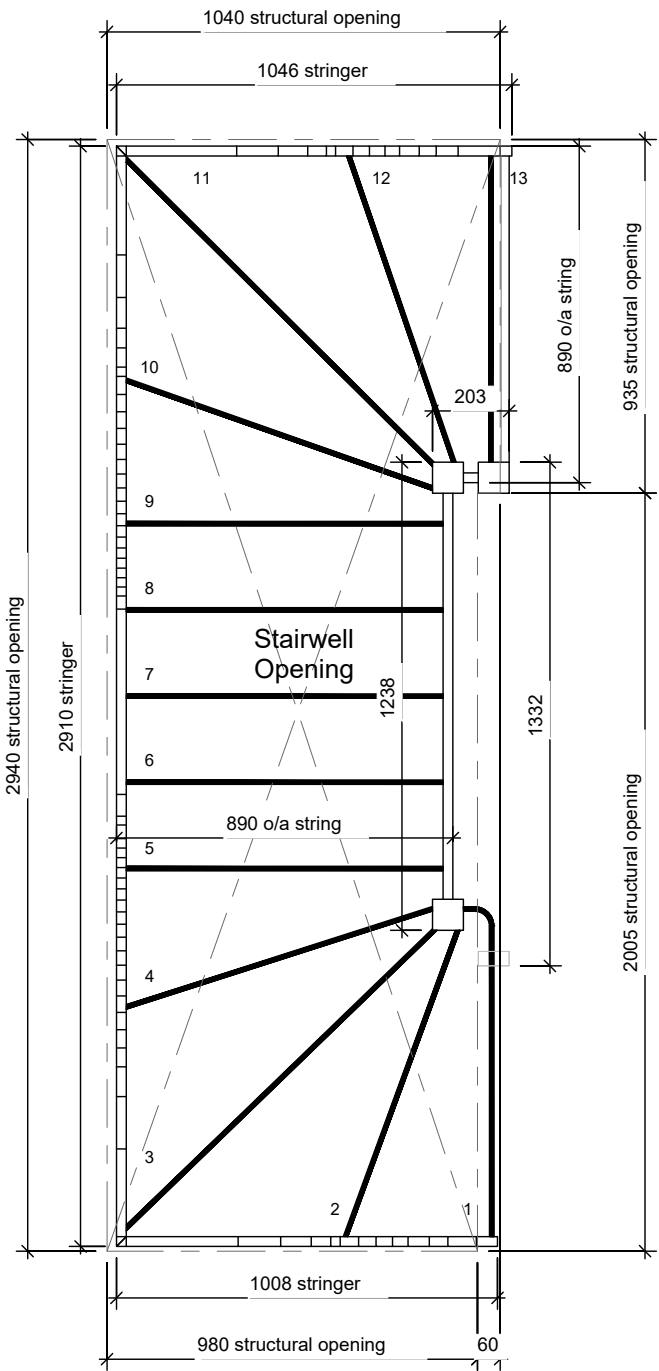

1 Staircase - Plan
1 : 20

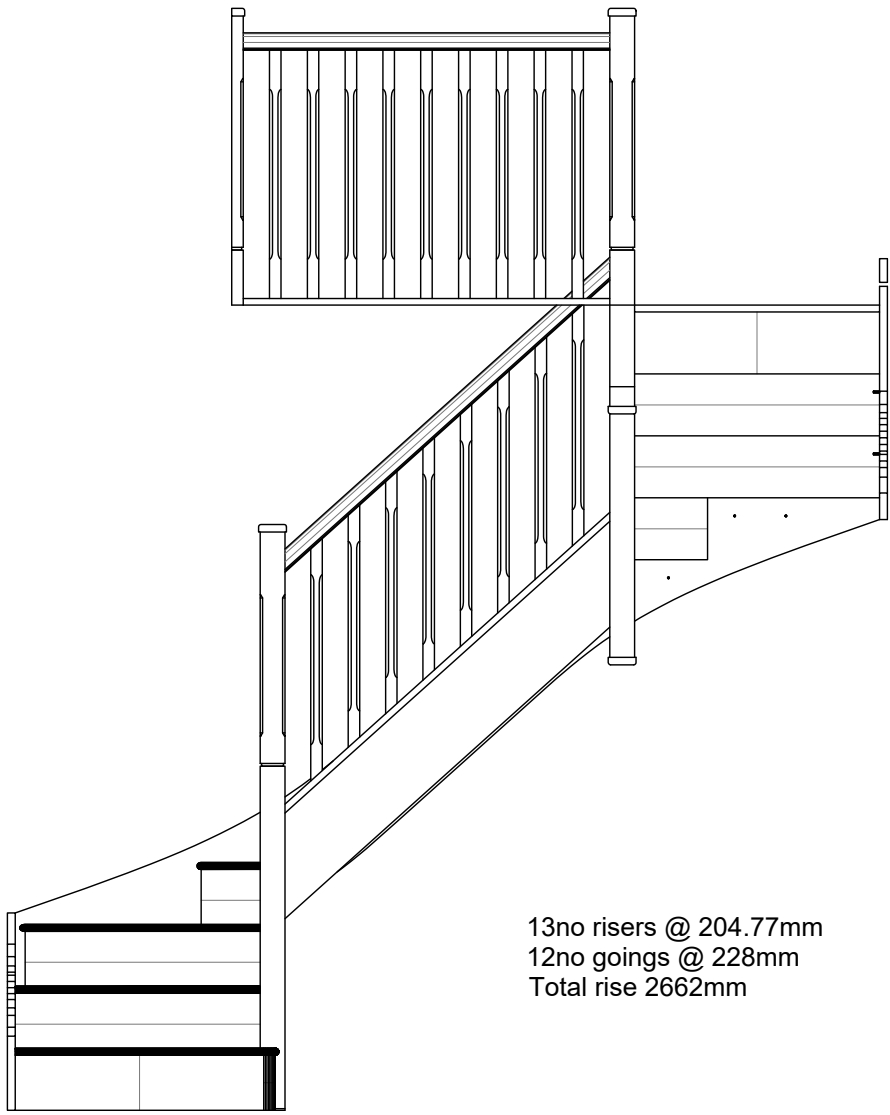

2 Stair - Elevation
1 : 25

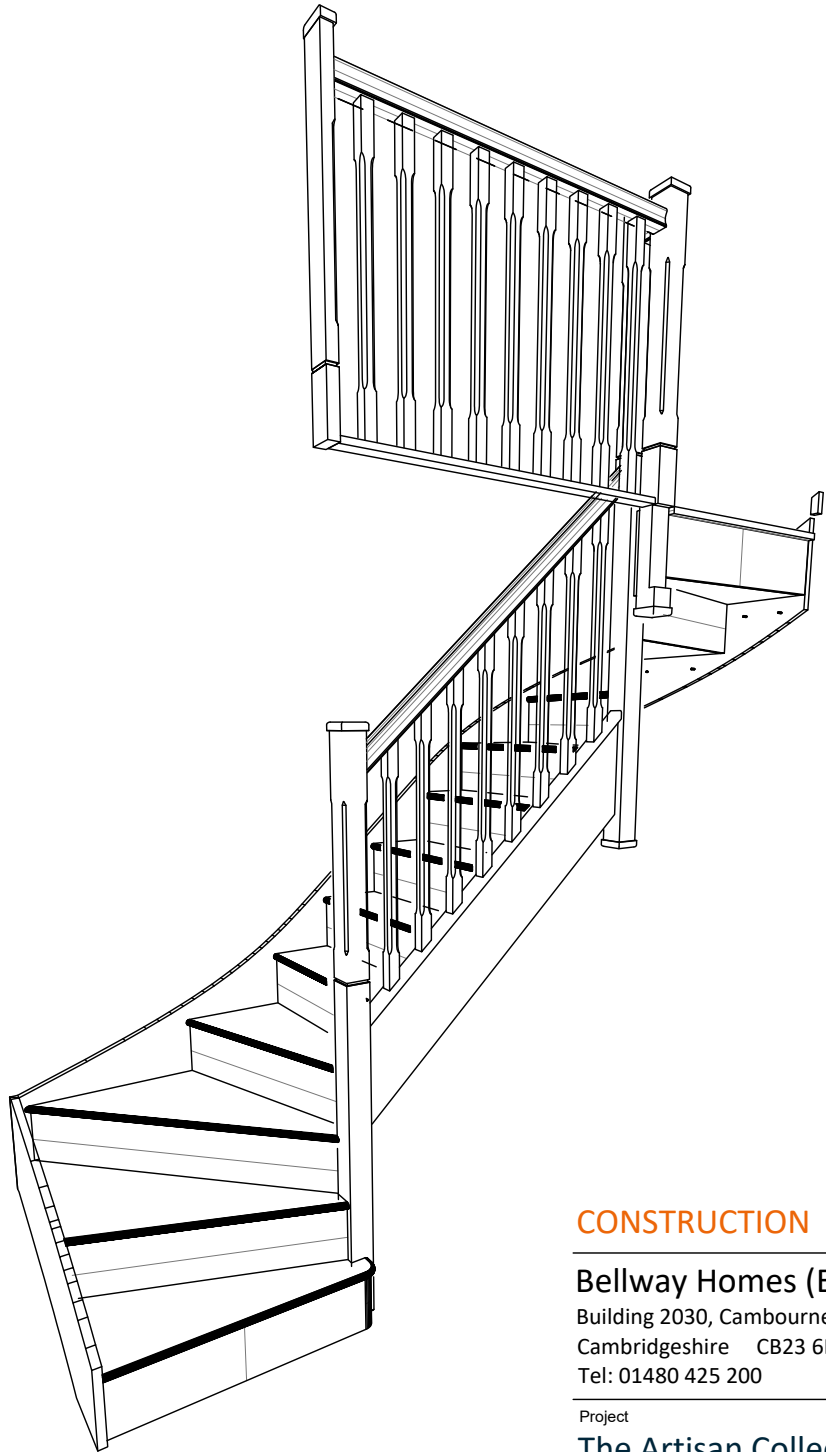

3 Staircase - 3d View

CONSTRUCTION

Bellway
www.bellway.co.uk

Bellway Homes (Eastern Counties)
Building 2030, Cambourne Business Park,
Cambridgeshire CB23 6DW
Tel: 01480 425 200

Project
The Artisan Collection
2020 Issue
Working Drawings

Building Regulations
2013 & 2021
Compliant

Drawing Title
The Hooper-Life
790 ft² | 2b Semi/Terr | All Variants
Staircase Details

HPL-2B-2S-0

Drawing Created By Group	First Issue Date 10 Aug 2020	Scale(s) As indicated
Project No	Drg Status Construction	Revision C1
Drawing No. BI01/790HP/50/0/01		

Do not scale - if in doubt, ask