


Revision Schedule			
Rev	Date	Description	Drn By
C1	01.12.25	Construction Issue	FDL

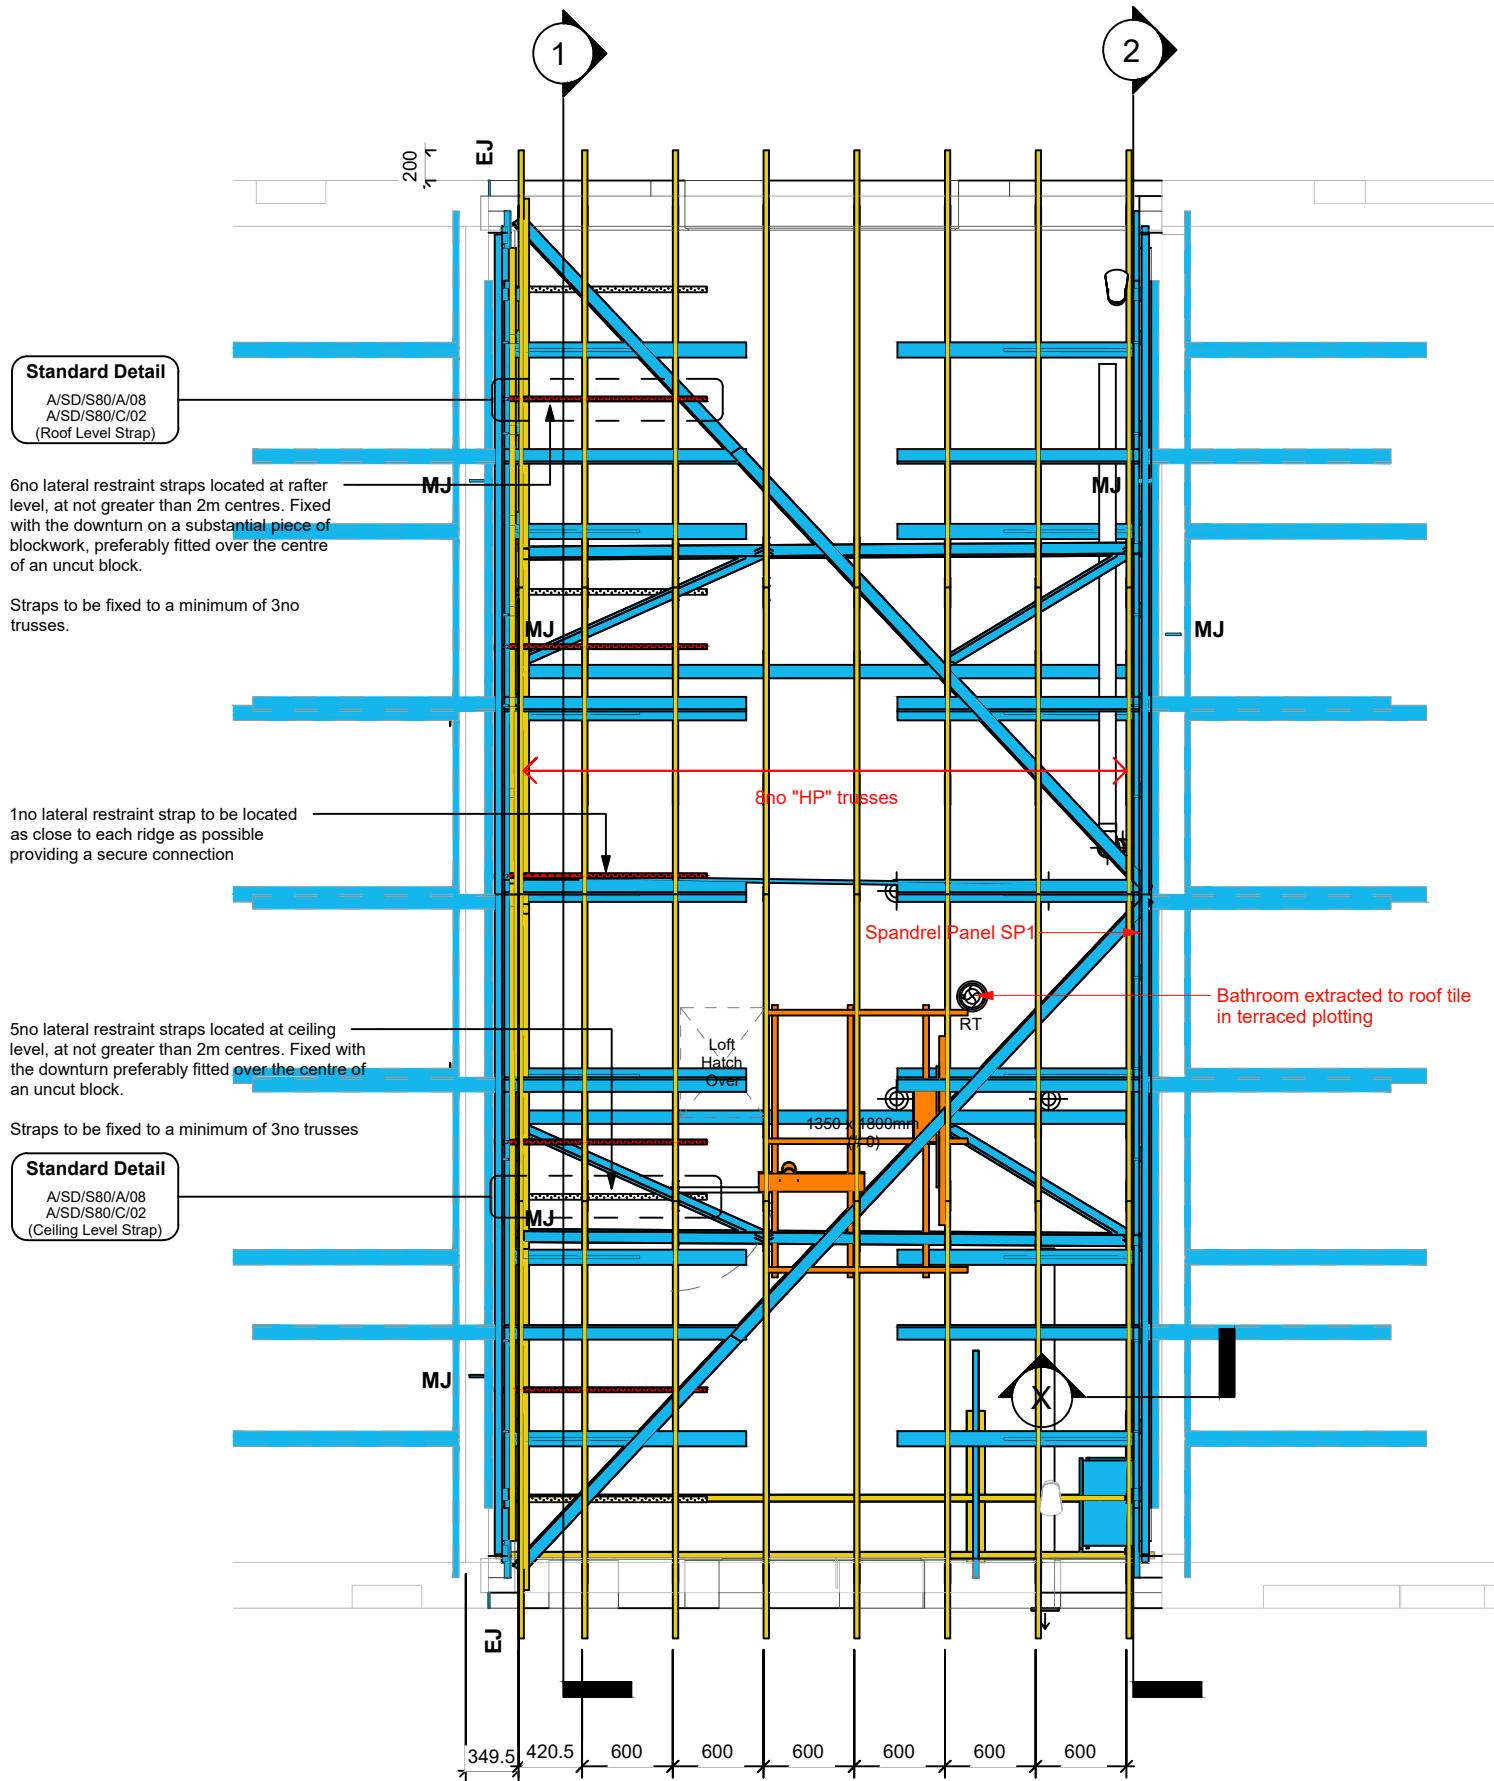

1 Roof Trusses - Terraced (Boxed Eaves) 1-50
1 : 50

CONSTRUCTION


www.bellway.co.uk

Bellway Homes (Eastern Counties)

Building Regulations
2013 & 2021
Compliant

Building 2030, Cambourne Business Park,
Cambridgeshire CB23 6DW
Tel: 01480 425 200

Project

Somersham

St Ives Road

Working Drawings

Drawing Title

The Hooper-Life

790 ft² | 2b Semi/Terr | All Variants

Roof Layout - Terraced

HPL-2B-2S-0

Drawing Created By Group	First Issue Date	Scale(s) 1 : 50
Project No	Drg Status Construction	Revision C1
Drawing No.		BI01/790HP/60/0/02