



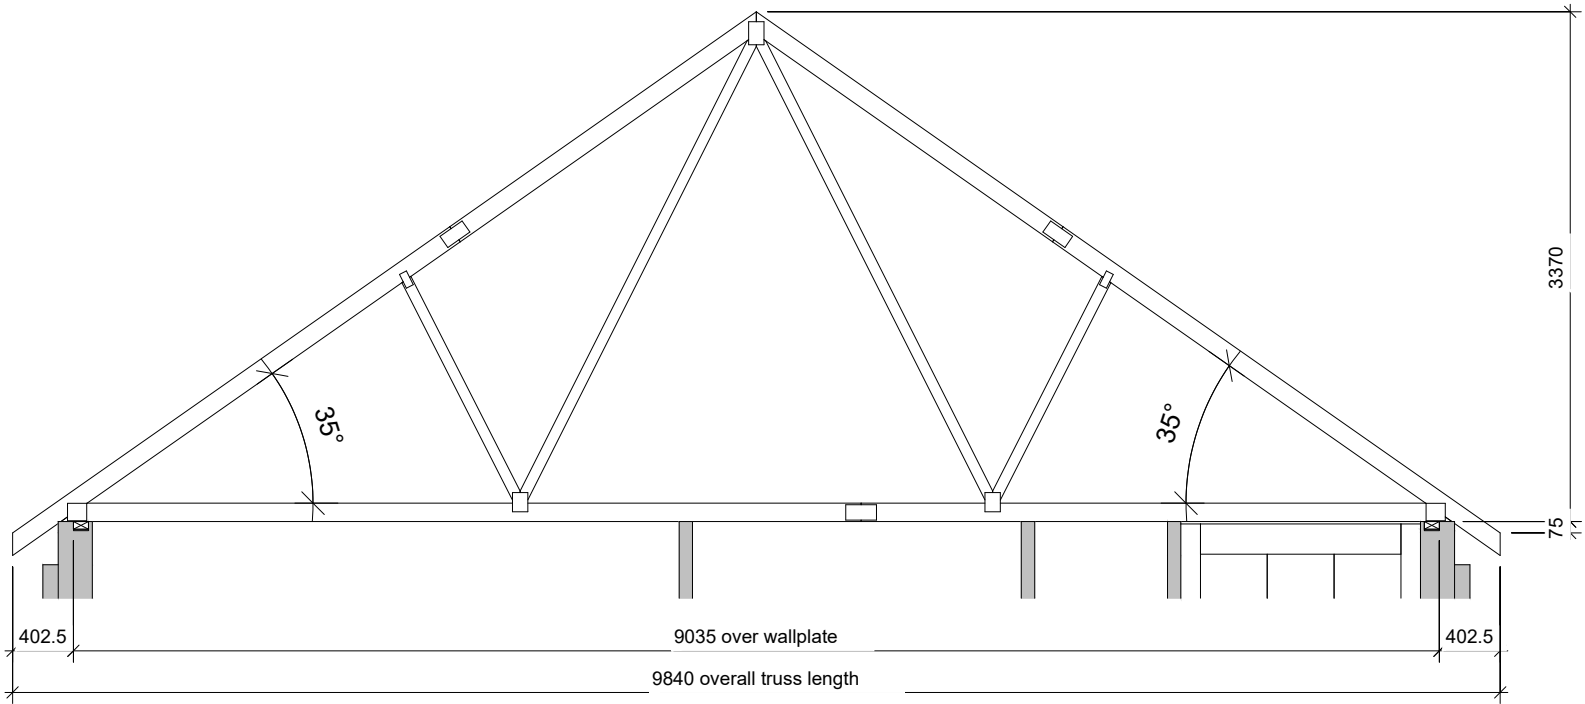


1 Truss "HP" - 8no reqd (1ply, 70kg)
1 : 50

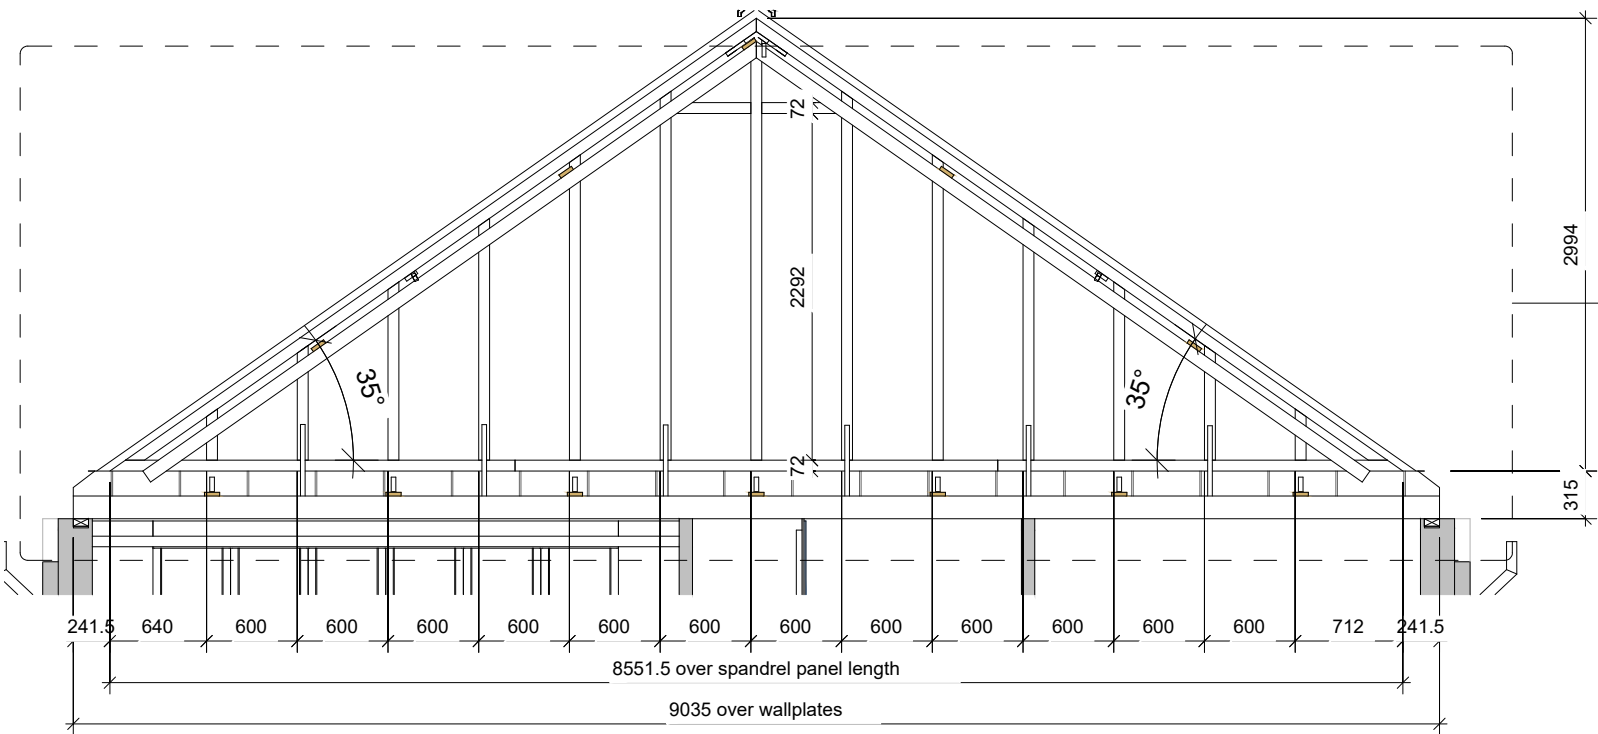

2 Spandrel Panel "SP1" (1ply, 490kg)
1 : 50

Standard Detail
Party Wall
Spandrel Panel
A/SD/S80/A/12-15

Revision Schedule			
Rev	Date	Description	Drn By
C1	01.12.25	Construction Issue	FDL

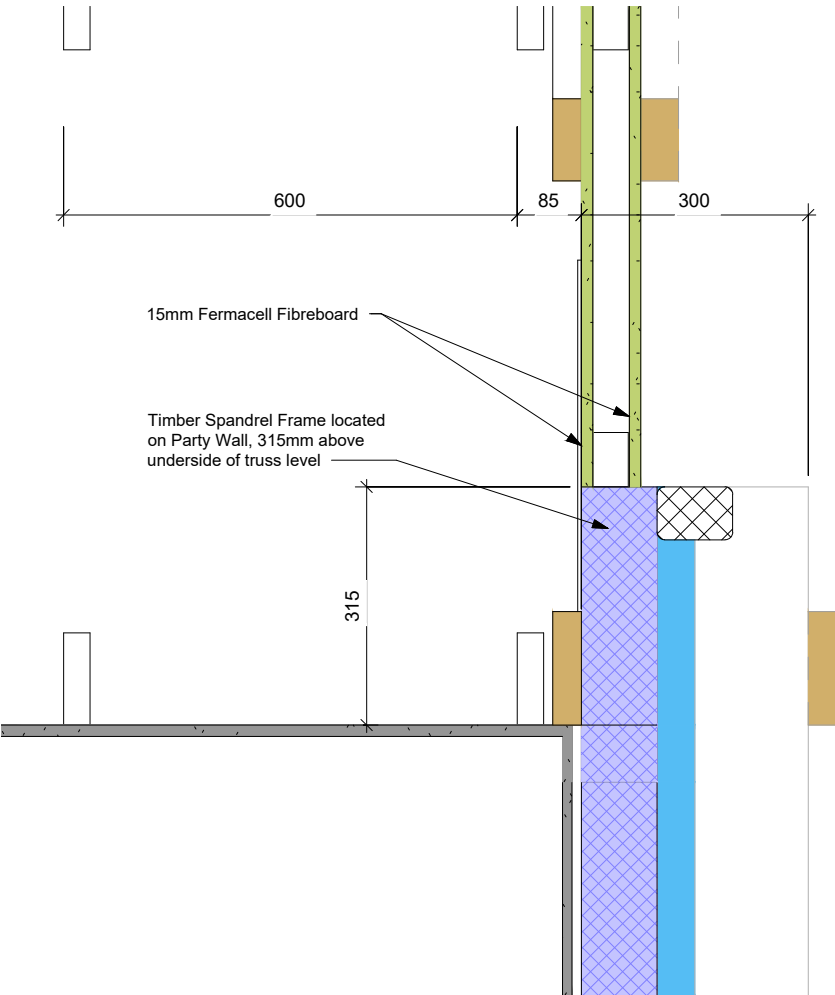

X Section X-X (Spandrel)
1 : 10

CONSTRUCTION

Bellway
www.bellway.co.uk

Bellway Homes (Eastern Counties)
Building 2030, Cambourne Business Park,
Cambridgeshire CB23 6DW
Tel: 01480 425 200

Building Regulations
2013 & 2021
Compliant

Project
Somersham
St Ives Road
Working Drawings

Drawing Title	HPL-2B-2S-0			
The Hooper-Life				
790 ft² 2b Semi/Terr All Variants				
Roof Trusses				

Drawing Created By	First Issue Date	Scale(s)
Group	April '25	As indicated
Project No	Drg Status	Revision
BI01	Construction	C1
Drawing No.	BI01/790HP/60/0/03	