


Revision Schedule			
Rev	Date	Description	Drn By
C1	01.12.25	Construction Issue	FDL

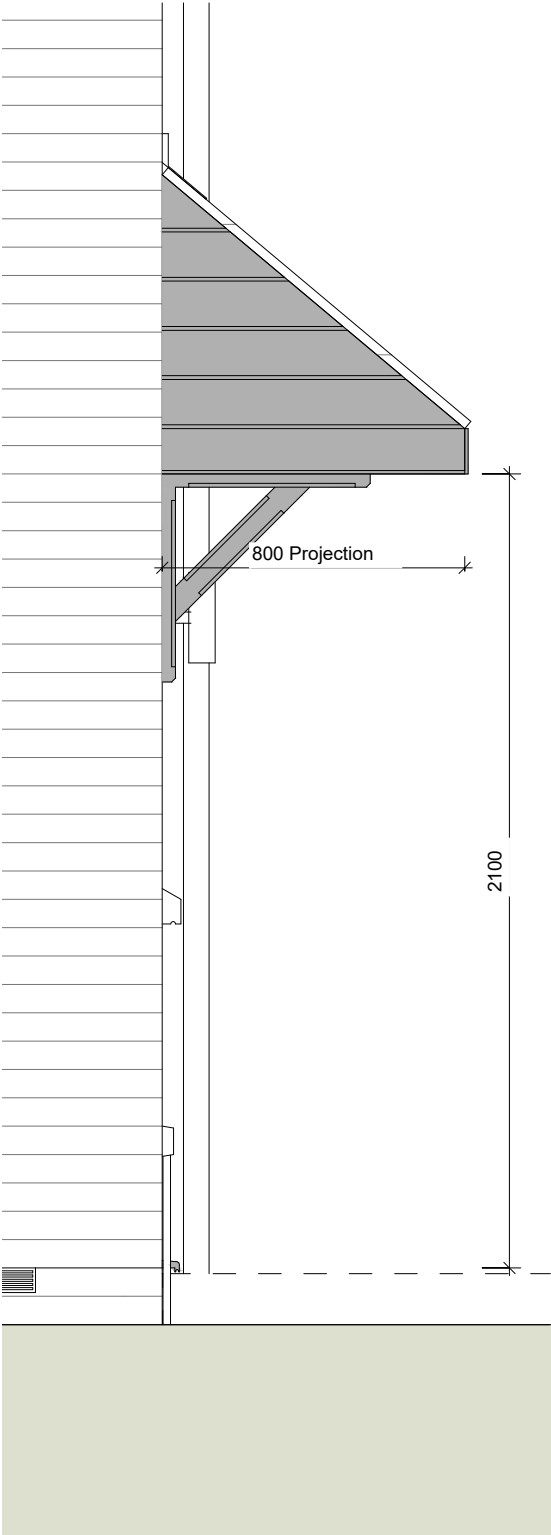

Elevations for dimensional purposes only.
Read with A/SD/S100/A/01 for canopy
fixing and construction details.

Plots 10, 16, 41, 42 (AS) & 11, 17, 43 (OPP)

CONSTRUCTION

Bellway

www.bellway.co.uk

Bellway Homes (Eastern Counties)

Building 2030, Cambourne Business Park,
Cambridgeshire CB23 6DW
Tel: 01480 425 200

Building Regulations
2013 & 2021
Compliant

Project

Somersham
St Ives Road
Working Drawings

Drawing Title
The Hooper-Life
790 ft² | 2b Semi/Terr | Country Brick
Canopy Details

HPL-2B-2S-CB

Drawing Created By Group	First Issue Date April '25	Scale(s) 1 : 20
Project No BI01	Drg Status Construction	Revision C1
Drawing No. BI01/790HP/65/CB/01		

Do not scale - if in doubt, ask